Tenda

sua próxima conquista

Book de Investimento

Regional: GO

Projeto: Presidente

Data Comitê: 11/08/2025

One Page

[1]

Cidade	Goiânia	**Mancha de demanda**	GO - GOS - Goiânia Sul + Aparecida de Goiânia
Regional	GO	**Cluster MPR**	3 - Verde
Cenário de Aprovação	Aprovação	**Tipo de Aprovação**	Consolidado
Fase Anterior	N/A		
Tipo de Comitê	Investimento	**Versão da VF**	Versão 1.0: Ago

Unidades (Fases)	1856 (4)	**CA Máx | Proj**	6,0 | 3,3
Unidades com Vaga (%)	642 (35%)	**Escritura | Lançamento**	nov/26 | jan/27
Unidades com Atributo* (%)	0 (0,0%)	**Tipologia**	F2E - Concreto

[2]

Valor Líquido do Terreno (% VGV)	34.722 (8,4%)	**Un. Perm. Fís (% Ter)**	0 (0,0%)
Cash (Correção)	500 (NA)	**%VGV Perm Fin Líquida (% Ter)**	8,3% (98,6%)
Valor R$/m²	990	**VAR (%VGV)**	500 (0,1%)

[3]

Custo Construção (%VGV)	172.548 (41,7%)	**Indireto Unit.**	17.280
Prazo da Obra (meses)	19	**Torre Unit.**	52.754
Custo Total Unit. (LPU):	92.968 (LPU 93)	**Infra Unit.**	14.081
Início de Obra	jul-27	**Fundação Unit.**	5.367

Preço Nominal Unit.	222.685	**VSO**	26
Preço Raso Unit.	205.334	**Referência**	Vision
Avaliação Unit.	222.159	**Renda (% em RET 1%)**	3.636 (5,8%)

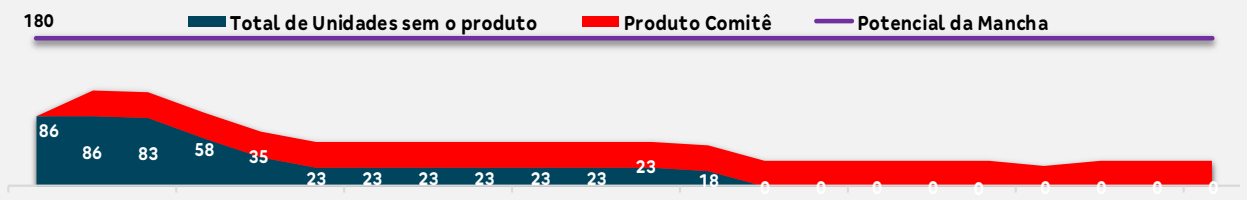

[4]

LI (Régua):	**23,1% (20,0%)**	**Margem Bruta Econômica:**	45,1%
LI Resiliência:	17,0% (N/A)	**Margem Rasa Econômica:**	39,8%
Margem Bruta REF:	48,4%	**Margem Contribuição Econômica:**	31,5%
Margem Rasa REF:	**44,1%**	**Exposição (% VGV):**	14.916 (3,1%)
TIR:	124,0%	**VGV Total:**	**413.304**
Payback Contingente (21 m) :	**19 m/ (-2 m)**	**Ger. Caixa 12 meses (R$):**	(515)
Payback Consolidado:	19	**Ger. Caixa 24 meses (R$):**	(7.940)

***Atributo: Varanda, Garden e Churrasqueira**

Destaques

[1] Apresentação em Comitê de Investimento do projeto **PRESIDENTE**, na Mancha Sul (Capital). Projeto composto por 3 condomínios, sendo os dois primeiros em fase única e o terceiro em duas fases. Trata-se de um terreno vertical prime, **T+18**, sequência do **Faiçalville.**

O Jardim Presidente está situado na região **Sudoeste** de Goiânia e é um bairro consolidado com vocação predominantemente residencial.

A Rua Presidente José Linhares, onde se localiza o imóvel objeto deste Comitê, possui fácil acesso às avenidas **Rio Verde, Ipanema e à avenida Presidente Cleveland** — importantes **eixos** que conectam a região ao restante da cidade. O entorno é composto por diversos comércios locais, como padarias, mercearias, farmácias, salões de beleza, pet shops, distribuidoras e lanchonetes.

A região é atendida por linhas de ônibus. Também há presença de Unidade de Saúde da Família (USF) nas imediações, e da Escola Estadual Professora Sebastião França.

[2] Negócio em permuta financeira com fração bruta de 9% e líquida de 8,03%.

Garantia do vendedor através do aval Tenda e seguro garantia ou hipoteca em favor da Permutante, no ato das escrituras.

[3] Custo de construção consolidado de ~ 92,9 K/UH em tipologia modular.

50% das unidades possuem varanda. O custo dessas varandas já foi incorporado ao orçamento, no entanto, esse valor ainda não foi refletido no preço de venda. Logo, há oportunidade de ganhos financeiros no desenvolvimento do projeto.

[4] Indicadores financeiros do projeto consolidado PRESIDENTE de MB = 45,1% e LI = 23,1%.

- Pareceres
- Análise da Mancha e Implantação
- Prospecção
- Operações
- Inteligência de Mercado
- Financeiro

Pareceres – PRESIDENTE

Área	Riscos Associados	Parecer	Criticidade
Jurídico	Due Diligence em andamento, com previsão de conclusão em 30/08/2025. Pontos de atenção já identificados: (i) os imóveis possuem débitos de IPTU que totalizam aproximadamente 900 mil reais, com parcelamento ativo até 2030. Foi previsto em contrato que a Tenda arcaria, o seu critério, com o valor de 500mil reais sem descontar do permuta (tal valor deverá ser previsto em viabilidade e em caso de rescisão do contrato, esse valor não será devolvido); (ii) os imóveis encontram-se ocupados por terceiros (um canil e uma horta), pendente a assinatura dos contratos de comodato regularizando as ocupações (ponto para baixa); (iii) Passivo judicial e débitos federais e municipais, passivo estimado em R$ 3 milhões.Débitos federais devem ser parcelados antes da ECV. Pendente levantamento patrimonial para avaliação do ativo x passivo, visando mitigar os riscos de fraude à execução (ponto para baixa); (iv) A Prefeitura de Goiânia move execução fiscal contra a permutante relativa à cobrança de ISSQN. Houve determinação de atos expropriatórios (bloqueio de bens), sendo necessário que a permutante formalize acordo para evitar a averbação de indisponibilidade de bens na matrícula dos imóveis (ponto para baixa); (v) Um dos Sócios que detém 50% do capital social da sociedade. De acordo com certidão de casamento, Gustavo casou-se em 07/01/2006, antes da constituição da empresa, e encontra-se divorciado desde 30/09/2014. Consta a Ação de Sobrepartilha, que discute a inclusão das quotas da sociedade na partilha de bens. Está pendente análise para verificar eventual restrição à alienação dos bens da sociedade; (vi) O contrato foi celebrado prevendo o pagamento da permuta a uma empresa terceira. No entanto, diante do histórico de desentendimento entre os sócios (irmãos), do passivo judicial encontrado e da ação de sobrepartilha em curso, que colocam o patrimônio da sociedade em risco, há potencial caracterização de fraude contra credores. Por isso, o pagamento da permuta deverá ser feito diretamente à proprietária dos imóveis, e não à empresa terceira, caso o cenário não se altere até o Comitê de Escritura (opção de pagamento já prevista em aditivo contratual).Resolutivas: O contrato possui cláusula resolutiva master de saída (viabilidade técnica, financeira, comercial e jurídica).	Ok com ressalvas	
Legalização	O IPTU está parcelado e quanto a isso não impede o protocolo e início dos processos. Os outros débitos em aberto e sem negociação além do IPTU podem também atrapalhar a emissão das taxas finais (remembramento, desmembramento e alvará de construção). No levantamento topográfico da matrícula 56.732, foi identificada uma cerca delimitando o terreno não compatível com o documento, a cerca será desconsiderada para não haver retificação de área. No levantamento topográfico da matrícula 134.792 , foi identificado um muro executado pelo vizinho, fora de sua poligonal, aumentando nossa área. Não haverá retificação de área, pois estamos seguindo com a poligonal correta de matrícula nos projetos. Será necessário doação de 15% do terreno, por se tratar de uma área em loteamento não aprovado. Definição de seguir com destinação de pagamento em pecúnia, processo esse precisará iniciar assim que for feita a baixa, pois terá que passar pela anuência do Municipio. Necessário termos o Termo de Compromisso da doação assinado para emissão do alvará de construção. Matrículas passaram por remembramento e posterior desmembramento para doação de sistema viário, conforme uso do solo, e separação em 3 condomínios. Prefeitura passa por um momento de definição de Decreto de arruamento, ainda em discussão e sem minuta prévia. Isso impacta no protocolo do desmembramento. Uso do solo com vencimento para novembro/2025. Importante protocolo do PL antes para não alterar cenário com nova interpretação do Município. Necessário emissão das viabilidades (AVTO Saneago, COMAER) para alvará de construção e licencimento ambiental. IPHAN será iniciado pelo time de LEG após a baixa.	Ok com ressalvas	
Produto		Ok	
GETEC	Atualmente, não há diretrizes para água e esgoto. Conforme indicado pelo projetista, estamos considerando o ponto provável de interligação para a extensão da rede de água. Quanto à rede de esgoto, estamos prevendo a implantação de uma ETE. O custo deverá ser revisado após a emissão da AVTO.	Ok com ressalvas	
Logística	Sem riscos	Ok	
Contratação	NA	Ok	
Inteligência de mercado	IM avalia o Preço Vision como factível	Ok	
Comercial/Ciclo	Ciclo Financeiro avalia Preço como factivel	Ok	
Estudos Econômicos	Ok, sem riscos associados	Ok	

Pareceres

Análise da Mancha e Implantação

Prospecção

Operações

Inteligência de Mercado

Financeiro

Mancha de Demanda

MANCHAS DE DEMANDA
Goiânia Sul + Aparecida

Lançamento

1. Estancia Dourados

LandBank

2. Faiçalville
3. Santa Rita
4. COPAG
5. Videira
6. Presidente

Cluster MPR – (Comitê)

Cluster 3 - Verde

Região

Capital

Lançados *LandBank* *Comitê*

PRODUTO

Empreendimento Presidente - Investimento

Informações Gerais – Todos os Condomínios		
Terreno	Área terreno	35.558,80m²
	Menor poligonal	27.230,96m²
	Reserva Proprietário	500,08m²
	App/fna	Não
	Reserva de calçada/ melhoramento víario	Sim – Diretriz viária (7.827,76m²)
	Área liquida	27.230,96m²
	Zoneamento	AA | AOS
	Ca máximo	6
	Ca projetado	3,29
	Gabarito máximo	T+18
Geral	Total uh	1.856UH
	Total de vagas (1/3)	455 (24,51 %- veículos) + 186 (10%motos)

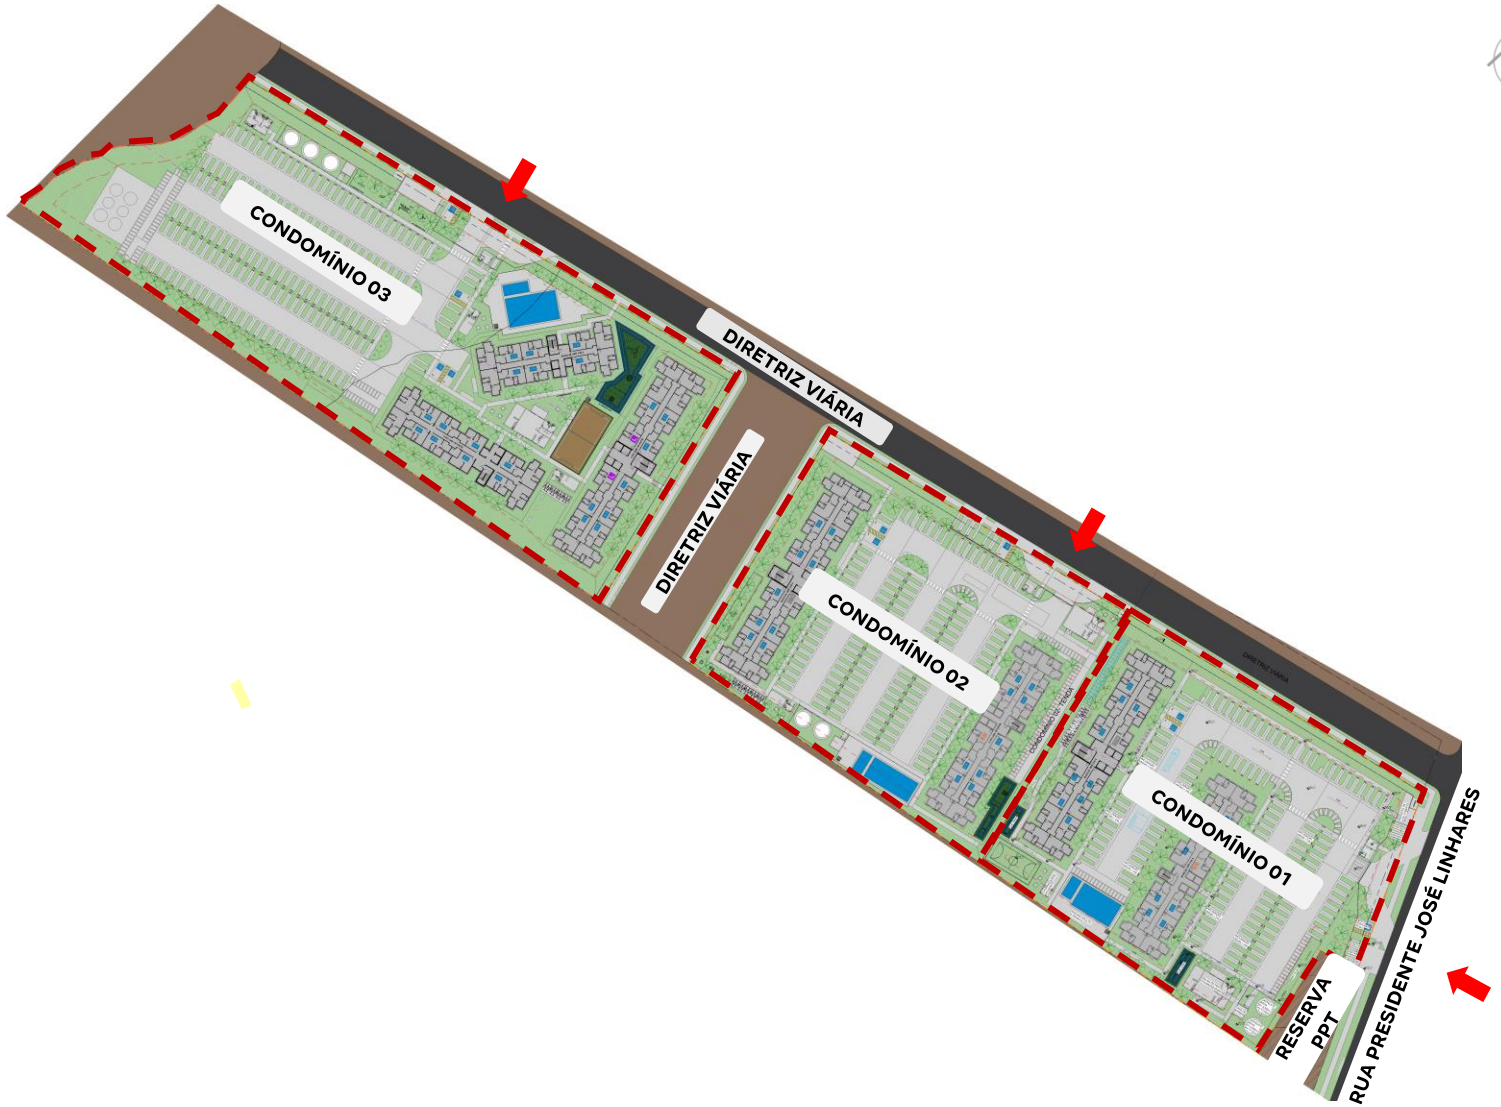

PRODUTO

Empreendimento Presidente - Investimento

Informações Gerais – Condomínio 01		
Terreno	**Área terreno**	7.980,41m²
	Menor poligonal	7.980,41m²
	App/fna	Não
	Reserva Proprietário	500,08m²
	Reserva de calçada/ melhoramento víario	Sim – Diretriz viária (7.827,76m²)
	Zoneamento	AA (sem fração)
	Ca máximo	6
	Ca projetado	2,93
	Gabarito máximo	T+18
Geral	**Total uh**	568
	Total de vagas (1/3)	139 (24,47 %- veículos) + 57 (10%motos
Tipologia	**Tipologia**	Modular com elevador
	Gabarito	T+18
	Lâmina	14PP | 16PP
	Garden	Não
	Varanda	Sim (50%)
	Área privativa	32,00m²
Condomínio	**Unidade pcd**	17
	Unidade lazer|técnica	00 | 02
	Torre	02
	Fase	01
Lazer	**Lazer coberto**	Salão de festas c/churrasqueira, Churrasqueira gourmet
	Lazer descoberto	Piscina,play kids, play baby, quadra gramada, fitness externo ,play pet e praça

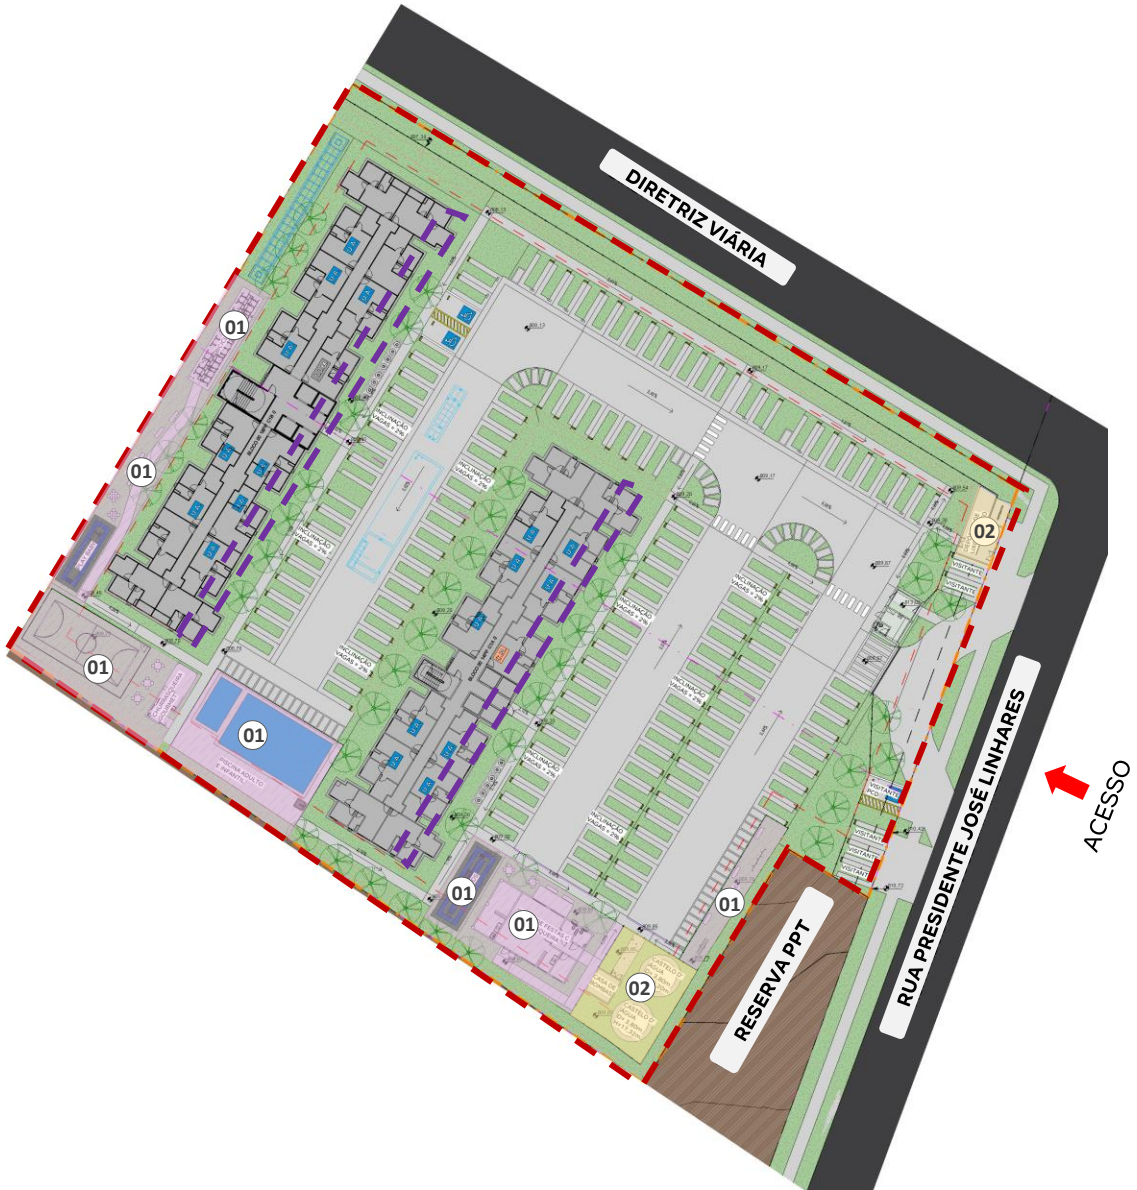

LEGENDA:

Varanda

01 Área de lazer

02 Área técnica

PRODUTO

Empreendimento Presidente - Investimento

Informações Gerais – Condomínio 02		
Terreno	Área terreno	7.446,51m²
	Menor poligonal	7.446,51m²
	App/fna	Não
	Reserva de calçada/ melhoramento víario	Sim – Diretriz viária (7.827,76m²)
	Zoneamento	AA (sem fração)
	Ca máximo	6
	Ca projetado	3,14
	Gabarito máximo	T+18
Geral	Total uh	568
	Total de vagas (1/3)	139 (24,47 %- veículos) + 57 (10%motos
Tipologia	Tipologia	Modular com elevador
	Gabarito	T+18
	Lâmina	14PP | 16PP
	Varanda	Sim (50%)
	Garden	Não
	Área privativa	32,00m²
Condomínio	Unidade pcd	17
	Unidade lazer|técnica	00 | 02
	Torre	02
	Fase	01
Lazer	Lazer coberto	Salão de festas c/churrasqueira, Churrasqueira gourmet
	Lazer descoberto	Piscina,play kids, play baby, quadra gramada, fitness externo ,play pet e praça

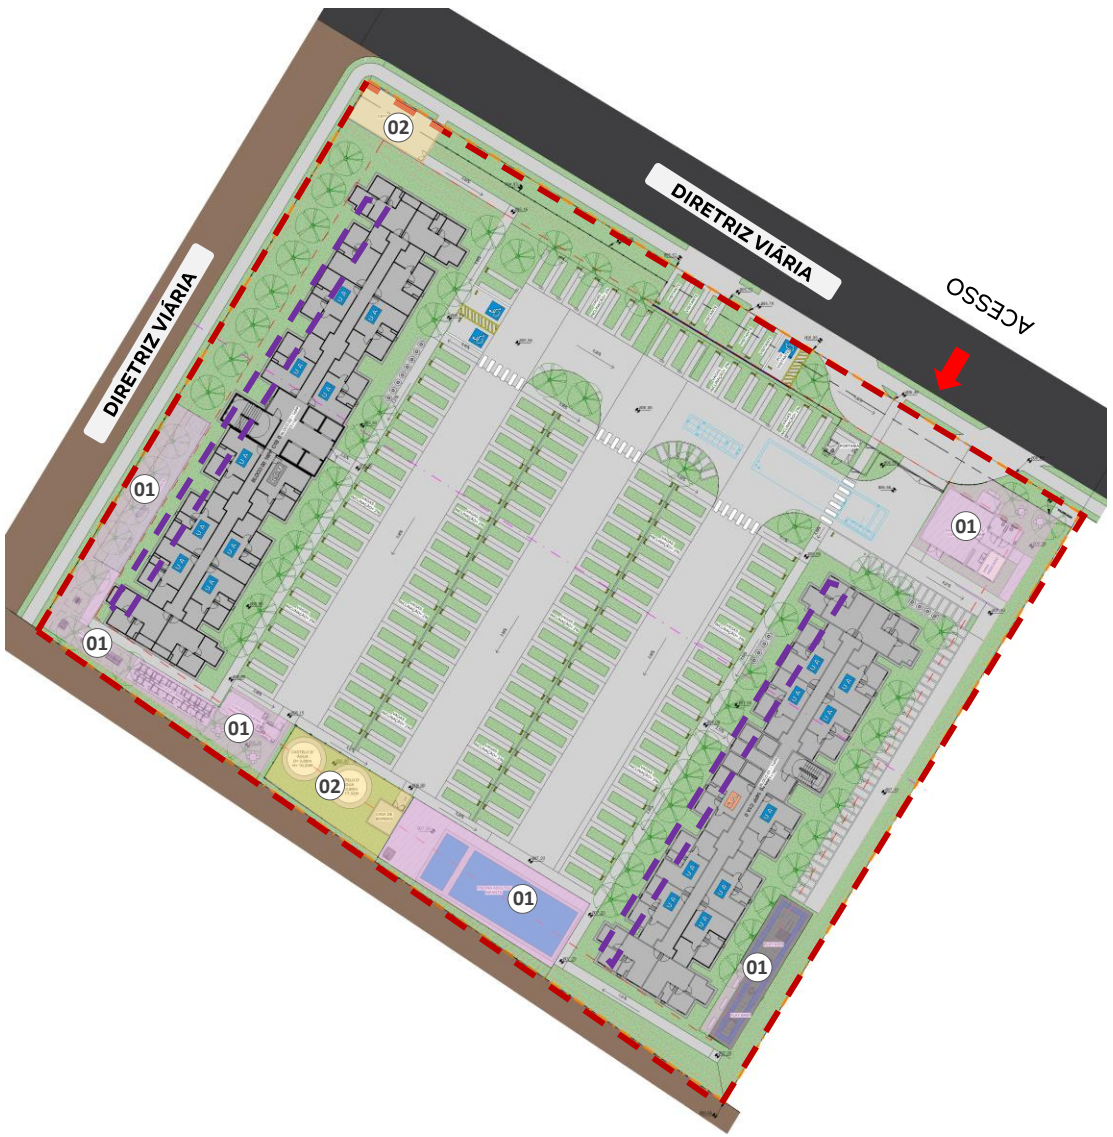

LEGENDA:

Varanda

01 Área de lazer

02 Área técnica

PRODUTO

Empreendimento Presidente - Investimento

Informações Gerais – Condomínio 0		
Terreno	**Área terreno**	11.804,03m²
	Menor poligonal	11.804,03m²
	App/fna	Não
	Reserva de calçada/ melhoramento víario	Sim – Diretriz viária (7.827,76m²)
	Zoneamento	AA (sem fração) | AOS (fração 180)
	Ca máximo	6
	Ca projetado	2,45
	Gabarito máximo	T+18
Geral	**Total uh**	720
	Total de vagas (1/3)	177 (24,58%- veículos) + 72 (10%motos
Tipologia	**Tipologia**	Modular com elevador
	Gabarito	T+18
	Lâmina	10PP | 12PP | 16PP
	Garden	Não
	Varanda	Sim (50%)
	Área privativa	32,00m²
Condomínio	**Unidade pcd**	22
	Unidade lazer|técnica	02 | 00
	Torre	03
	Fase	01
Lazer	**Lazer coberto**	Salão de festas c/churrasqueira, Churrasqueira gourmet
	Lazer descoberto	Piscina,play kids, play baby, quadra street ball, fitness externo ,play pet, quadra de areia

LEGENDA:

Varanda

01 Área de lazer

02 Área técnica

PRODUTO

Empreendimento Presidente - Investimento

	Descrição	Criticidade	Parecer
Usabilidade	Limite supercondomínio		
	Acesso		
	Percurso do pedestre até torre		
Diferencial produto	Atributos Infra	Sim	Quadra gramada, quadra de areia e piscina
	Atributos Torre	Sim	Varanda 50% em todas as torres
	Edifício Garagem	Não	

Perspectiva

Pareceres

Análise da Mancha e Implantação

Prospecção

Operações

Inteligência de Mercado

Financeiro

➢ CONDIÇÕES DO NEGÓCIO

- O negócio será pago em Fluxo em permuta financeira de dois imóveis localizados na Rua Presidente José Linhares (matrículas nº 56.732 e nº 134.792 – 1º CRI Goiânia. Com **fração bruta de 9% e líquida de 8,03% do VGV** (PCV assinada em **maio/25**). O valor do negócio na VF é de R$ 34.721.564,17. Com pagamento de mínimo garantido no contrato de R$ 27.786.240,00.

- Os imóveis serão objeto de parcelamento (remembramento e desmembramento) para criação de novos lotes:

- 1 lote permanecerá com a Permutante (Lote Comercial de 500 m² com vedação de atividades conflitantes com a Tenda)
- 3 lotes serão adquiridos pela Tenda para implantação de 3 empreendimentos residenciais
- Não temos obrigação de adquirir todos os lotes, aquisição de forma parcial e sequencial a critério da Tenda. Ainda, as condições resolutivas são aplicáveis a cada lote individualmente.

- Os imóveis estão ocupados por comodatários: obrigação da permutante de apresentar os contratos de comodatos e de desocupação até 60 dias antes da escritura. A Tenda pode tomar providências diretamente em caso de descumprimento.

- -O IPTU deste terreno está negociado e parcelado. Tal parcelamento deve estar em dias durante o período de aprovação do projeto. O valor é de ~R$ 930 mil. A Tenda pagará R$ 500 mil a critério e momento de nossa escolha, sem descontar do preço. Na VF este custo foi considerado para setembro/25 em parcela única. O restante do valor de R$ 430 k está sendo pago pelo proprietário da área.

- Parcelamento sequencial das escrituras, conforme aprovação e comercialização dos empreendimentos.

- Participação será paga na conta de titularidade da Diogo Oliveira e Souza Sociedade Individual de Advocacia.

- Para o seguro permutante na VF foi considerado uma taxa de 0,70% ao ano, totalizando R$875 k com pagamento no ato da ECV.

- O contrato possui cláusula master de saída;
- Due diligence em andamento;

➢ **OBRIGAÇÕES CONTRATUAIS:**

- ECV: o primeiro lote/empreendimento deverá ser Escriturado em até 12 meses a partir da assinatura da PCV, prorrogável automaticamente por mais 6 meses;
- O lançamento deverá ser realizado em 6 meses após a ECV;

➢ **CORREÇÃO MONETÁRIA**

- Não se aplica.

➢ **GARANTIAS**

- Para os Vendedores:
  - Aval Tenda;
  - Garantia da Tenda via seguro do valor mínimo garantido de R$ 27.786.240,00 ou hipoteca em favor da Permutante, no ato das escrituras. O valor mínimo está associado à cada Condomínio escriturado.

➢ **INTERMEDIAÇÃO IMOBILIÁRIA**

- Contratos de intermediação assinados. O valor da intermediação será no total de 4% divididos entre KLAITON DE SOUSA KOZIEL LTDA , inscrito no CRECI PF n° 40.288 e PODIUM GESTÃO IMOBILIÁRIALTDA, inscrita no CRECI PJ nº 27.295.

- Pareceres
- Análise da Mancha e Implantação
- Prospecção
- Operações
- Inteligência de Mercado
- Financeiro

Custo de Construção

	PRESIDENTE COND. 01 CEN01 | REV00	PRESIDENTE COND. 02 CEN01 | REV00	PRESIDENTE COND. 03 CEN01 | REV00	PRESIDENTE CEN01 | REV00 CONSOLIDADO	FAIÇALVILLE CEN. 01 | R00	JARDIM GRAMADO CEN02 | REV01
Torres	2	2	3	7	2	2
Unidades Construídas	570	570	722	570 | 570 | 722	504	578
Unidades Vendidas	568	568	720	568 | 568 | 720	501	576
Total Unidades Vendidas	568	568	720	1.856	501	576
Unidades com Varanda	270	270	342	882	-	128
Condomínios (qta.)	1	1	1	3	1	1
Cidade	Goiânia - GO	Goiânia - GO	Goiânia - GO	Goiânia - GO	Goiânia - GO	Goiânia - GO
Produto / Selo	F2E MODULAR	F2E MODULAR	F2E MODULAR	F2E MODULAR	F2E MODULAR	F2E MODULAR
Tipologia	1 Torre | T+18 | 14PP | CE1A	1 Torre | T+18 | 14PP | CE1A	1 Torre | T+18 | 10PP | CE1A	1 Torre | T+18 | 10PP | CE1A	1 Torre | T+17 | 12PP | CE1A	1 Torre | T+16 | 16PP | C1A
Tipologia	1 Torre | T+18 | 16PP | CE1B	1 Torre | T+18 | 16PP | CE1B	1 Torre | T+18 | 12PP | CE1A	1 Torre | T+18 | 12PP | CE1A	1 Torre | T+17 | 16PP | CE1B	1 Torre | T+16 | 18PP | C1A
Tipologia	-	-	1 Torre | T+18 | 16PP | CE1B	2 Torres | T+18 | 14PP | CE1A	-	-
Tipologia	-	-	-	2 Torres | T+18 | 16PP | CE1B	-	-
Atributos de Projeto	Varanda e Piscina	Varanda e Piscina	Varanda e Piscina	Varanda e Piscina	-	-
Projeto Infra	AP	AP	AP	AP	AP	AP
Projeto Torre	AP	AP	AP	AP	AP	PR
Mês Base	agosto-25	agosto-25	agosto-25	agosto-25	novembro-24	agosto-24
Incc	1.199,509	1.199,509	1.199,509	1.199,509	1.149,170	1.118,827
LVS	junho-25	junho-25	junho-25	junho-25	outubro-24	junho-24
Indiretos	junho-25	junho-25	junho-25	junho-25	outubro-24	junho-24
Base de Preço	LPU 93	LPU 93	LPU 93	LPU 93	LPU 84	LPU 81
Takt	2x2	2x2	2x2	2x2	2x2	2x2
Prazo (mês)	19	19	21	19 | 19 | 21	19	19
CUSTO TOTAL I	R$ / UND R$ 91.426	R$ / UND R$ 91.003	R$ / UND R$ 91.060	R$ / UND R$ 91.155	R$ / UND R$ 88.776	R$ / UND R$ 83.521
Indireto	R$ 18.153	R$ 17.989	R$ 17.280	R$ 17.764	R$ 18.418	R$ 17.140
Torre	R$ 52.022	R$ 52.022	R$ 52.754	R$ 52.306	R$ 50.332	R$ 46.078
Infra	R$ 14.077	R$ 13.722	R$ 14.081	R$ 13.970	R$ 13.939	R$ 15.014
Fundação	R$ 5.271	R$ 5.271	R$ 5.367	R$ 5.309	R$ 4.772	R$ 4.704
EEE	R$ 454	R$ 454	R$ 358	R$ 417		
ETE	R$ 1.219	R$ 1.219	R$ 962	R$ 1.119	R$ 1.000	
Contenção	R$ 44	R$ 68	R$ 49	R$ 53	R$ 12	
Terraplenagem	R$ 185	R$ 258	R$ 208	R$ 216	R$ 302	R$ 585
CUSTO TOTAL II	R$ 1.813	R$ 1.813	R$ 1.813	R$ 1.813	R$ 1.546	R$ 1.326
Urbanização	R$ 1.085	R$ 1.085	R$ 1.085	R$ 1.085	R$ 384	R$ 209
Drenagem	R$ 302	R$ 302	R$ 302	R$ 302		
Extensão de Rede Elétrica	R$ 167	R$ 167	R$ 167	R$ 167	R$ 130	R$ 110
Extensão de Rede Hidráulica	R$ 259	R$ 259	R$ 259	R$ 259	R$ 1.032	R$ 1.007
CUSTO TOTAL III						
Incorridos						
CUSTO TOTAL IV						
Aprendizado						
CUSTO TOTAL V					R$ 3.957	R$ 6.119
Atualização por INCC					R$ 3.957	R$ 6.119
CUSTO TOTAL I+II	R$ 93.239	R$ 92.817	R$ 92.873	R$ 92.968	R$ 90.321	R$ 84.847
CUSTO TOTAL I AO IV	R$ 93.239	R$ 92.817	R$ 92.873	R$ 92.968	R$ 94.278	R$ 90.965

Custo de Construção

	PRESIDENTE CEN01 | REV00 CONSOLIDADO	FAIÇALVILLE CEN. 01 | R00	
Torres	7	2	
Unidades Construídas	570 | 570 | 722	504	
Unidades Vendidas	568 | 568 | 720	501	
Total Unidades Vendidas	1856	501	
Unidades com Varanda	882	-	
Condomínios (qta.)	3	1	
Cidade	Goiânia - GO	Goiânia - GO	
Produto / Selo	F2E MODULAR	F2E MODULAR	
Tipologia	1 Torre | T+18 | 10PP | CE1A	1 Torre | T+17 | 12PP | CE1A	
Tipologia	1 Torre | T+18 | 12PP | CE1A	1 Torre | T+17 | 16PP | CE1B	
Tipologia	2 Torres | T+18 | 14PP | CE1A	-	
Tipologia	2 Torres | T+18 | 16PP | CE1B	-	
Atributos de Projeto	Varanda e Piscina	-	
Projeto Infra	AP	AP	
Projeto Torre	AP	AP	
Mês Base	agosto-25	novembro-24	
Incc	1199,509	1149,170	
LVS	junho-25	outubro-24	
Indiretos	junho-25	outubro-24	
Base de Preço	LPU 93	LPU 84	
Takt	2x2	2x2	
Prazo (mês)	19 | 19 | 21	19	
CUSTO TOTAL I	R$ / UND R$ 91.155	R$ / UND R$ 88.776	DIF R$ 2.379
INDIRETO	R$ 17.764	R$ 18.418	-R$ 653
TORRE	R$ 52.306	R$ 50.332	R$ 1.974
INFRA	R$ 13.970	R$ 13.939	R$ 30
FUNDAÇÃO	R$ 5.309	R$ 4.772	R$ 537
EEE	R$ 417	R$ 0	R$ 417
ETE	R$ 1.119	R$ 1.000	R$ 119
CONTENÇÃO	R$ 53	R$ 12	R$ 41
TERRAPLENAGEM	R$ 216	R$ 302	-R$ 86
CUSTO TOTAL II	R$ 1.813	R$ 1.546	R$ 267
VIÁRIO	R$ 1.085	R$ 384	R$ 700
DRENAGEM	R$ 302	R$ 0	R$ 302
EXTENSÃO DE REDE ELÉTRICA	R$ 167	R$ 130	R$ 37
EXTENSÃO DE REDE HIDRÁULICA	R$ 259	R$ 1.032	-R$ 772
CUSTO TOTAL III	R$ 0	R$ 0	R$ 0
INCORRIDOS	R$ 0	R$ 0	R$ 0
CUSTO TOTAL IV	R$ 0	R$ 0	R$ 0
APRENDIZADO	R$ 0	R$ 0	R$ 0
CUSTO TOTAL V	R$ 0	R$ 3.957	-R$ 3.957
ATUALIZAÇÃO POR INCC	R$ 0	R$ 3.957	-R$ 3.957
CUSTO TOTAL	R$ 92.968	R$ 94.278	-R$ 1.310

INDIRETOS

-763 | G11 – Serviços Técnicos (Diluição)
+486 | G13 – Pessoal Permanente (Dissídio/Gape)
-279 | G15 – Canteiro (Diluição)

TORRE

+964 | Vertical (LVS 06/25 x LVS 10/24)
+130 | Aço (Projeto)
Presidente: Taxa de aço: 41,2Kg/m³ | **Faiçaville:** Taxa de aço: 40Kg/m³
+313 | Concreto (Preço)
Presidente: R$733,46/m³ | **Faiçaville:** R$711,53/m³
+639 | Esquadria de Alumínio (Presidente tem 47% de apto de Varanda)
+342 | Instalações (LVS 06/25 x LVS 10/24)
+109 | Esquadria de Ferro (Diluição/Varanda)
-567 | Elevador (Projeto)
Presidente: 12PP, 14PP E 16PP - Zoneado | 10PP – Não Zoneado (R$4.596/UH)
Faiçaville: 16PP - Zoneado | 12PP – Não Zoneado (R$5.163/UH)

INFRA

-1.373 | Instalações (LVS Média F2E 06/25 x LVS Pq. dos Sonhos I 10/24)
+1.518 | Anexos (Presidente possui atributos como Portaria com Pórtico, quadras, churrasqueiras e piscinas)

FUNDAÇÃO

+537 | Projeto
Presidente: Hélice Ø 40 cm, Ø 50 cm e Ø 60 cm – 17m
Faiçaville: Hélice Ø 40 cm, Ø 50 cm e Ø 60 cm – 14 a 16m

TERRAPLENAGEM

-86 | Projeto

Operações

SISTEMA DE ABASTECIMENTO DE ÁGUA
Conforme alinhamento entre a regional e o projetista, foi prevista a extensão de rede de 500 metros.

SISTEMA DE ESGOTAMENTO SANITÁRIO
Conforme alinhamento entre a regional e o projetista, o condomínio contará com uma ETE e seu emissário será destinado para o córrego, com extensão de 400m metros.

SISTEMA DE DRENAGEM
Considerado descarte para o córrego ao fundo do terreno.

SISTEMA DE ABASTECIMENTO DE GÁS
Abastecimento por GLP.

SISTEMA DE ABASTECIMENTO ELÉTRICO
Existe viabilidade técnica.

TERRENO

URBANIZAÇÃO
Foi considerado execução da calçada de todo perímetro do empreendimento e viário lateral para acesso aos condomínios.

Operações

Matriz Risco Concessionária	
Água	Nível 5
Esgoto	Nível 5
Drenagem	NA
Elétrica	Nível 3
Gás	NA
Urbanização	NA

LEGENDA		
Nível	Tipo	Status
1	Com Diretriz	Conclusiva
2		Conclusiva com projeto aprovado
3		Conclusiva sem projeto aprovado
4		Não Conclusiva
5	Sem Diretriz	-
NA	-	Não aplicável

Água:
- Sem viabilidade emitida.

Esgoto:
- Sem viabilidade emitida.

Drenagem:
- Não se aplica.

Elétrica:
- Viabilidade emitida em 07/2025.
- No pedido de ligação definitiva a concessionária pode vir a cobrar reformas necessárias, caso a infraestrutura existente não seja suficiente.

Gás:
- Empreendimento com GLP.

Urbanização:
- Foi considerado execução da calçada de todo perímetro do empreendimento e viário lateral para acesso aos condomínios.

Fundação:
- Realizada campanha de sondagem contemplando 26 furos.
- Considerada Estaca Hélice, com diâmetros de 40, 50 e 60cm e profundidade de 17m.

Logística – Cond. 01

MODULAÇÃO CEF E TOMBAMENTO
1 : 700

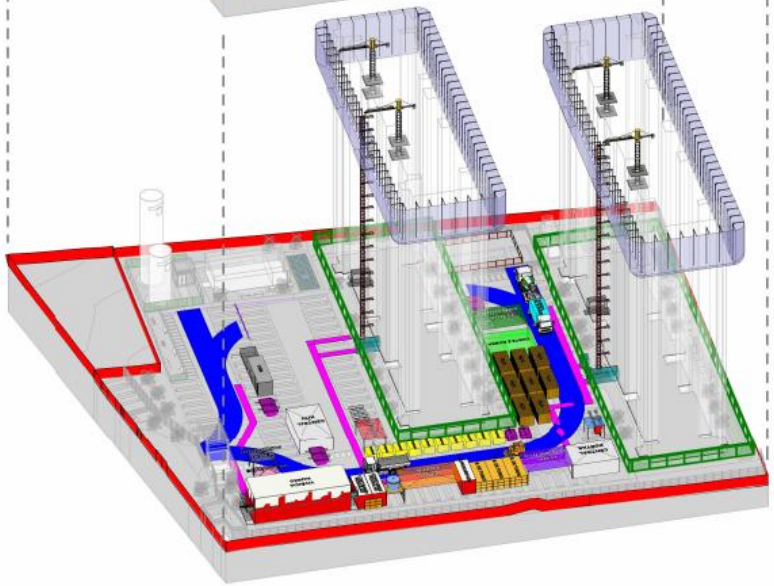

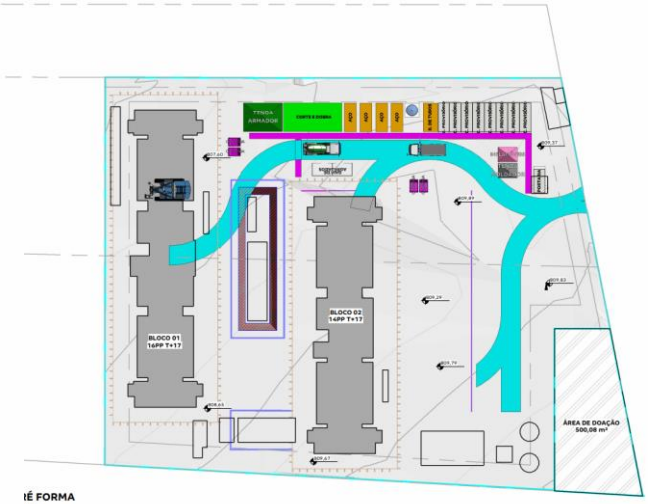

TÉ FORMA
500

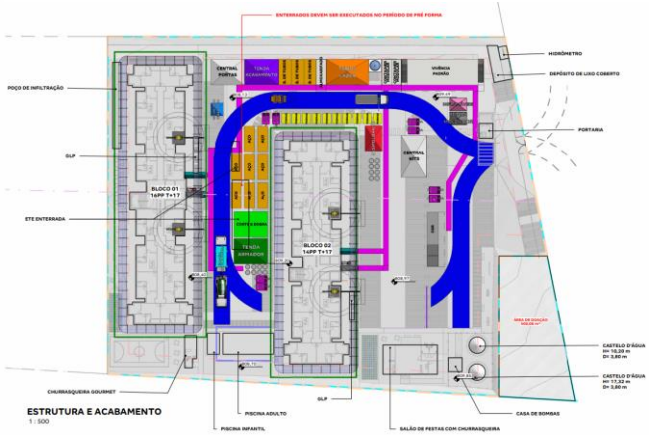

ESTRUTURA E ACABAMENTO
1 : 500

LOG_VIVÊNCIA - CONTAINERS

DESCRIÇÃO	QUANTIDADE	TAMANHO MÓDULOS	MOBILIZAÇÃO	DESMOBILIZAÇÃO	PRÉ FORMA	ESTRUTURA	ACAB.	FASE
CONTAINER ALMOXARIFADO (LOG)	1 MÓDULO DE CONTAINER	2,41 X 6,10 m	1 MOBILIZAÇÃO	1 DESMOBILIZAÇÃO	-	TODO PERÍODO	TODO PERÍODO	ÚNICA
CONTAINER MODULAR (LOG)	1 MÓDULO DE CONTAINER	2,41 X 6,10 m	1 MOBILIZAÇÃO	1 DESMOBILIZAÇÃO	-	TODO PERÍODO	TODO PERÍODO	ÚNICA
CONTAINER PORTARIA (LOG)	CONSIDERAR 1 MÓDULO COM SANITÁRIO E CATRACA	2,41 X 4,90 m	1 MOBILIZAÇÃO	1 DESMOBILIZAÇÃO	TODO PERÍODO	-	TODO PERÍODO	ÚNICA
CONTAINER PROVISÓRIO (LOG)	CONSIDERAR 8 MÓDULOS DE CONTAINER	2,41 X 6,10 m	1 MOBILIZAÇÃO	1 DESMOBILIZAÇÃO	TODO PERÍODO	-	-	ÚNICA
CONTAINER VIVÊNCIA PADRÃO (LOG)	CONSIDERAR 14 MÓDULOS COM 2 ESCADAS (7 MÓDULOS NO PAV. T E 7 MÓDULOS NO PAV SUPERIOR)	2,41 X 6,10 m	1 MOBILIZAÇÃO	1 DESMOBILIZAÇÃO	-	TODO PERÍODO	TODO PERÍODO	ÚNICA

LOG_TENDAS_PERÍODOS

DESCRIÇÃO	QUANTIDADE	LARGURA	COMPRIMENTO	PRÉ FORMA	ESTRUTURA	ACABAMENTO	FASE
GAIOLA DE DESMOLDANTE (LOG)	1	4,00	6,00	-	TODO PERÍODO	-	ÚNICA
GAIOLA DE INFLAMÁVEIS (LOG)	1	3,00	4,00	-	TODO PERÍODO	TODO PERÍODO	ÚNICA
TENDA ACABAMENTO (LOG)	1	6,00	8,00	-	TODO PERÍODO	TODO PERÍODO	ÚNICA
TENDA ARMADOR (LOG)	2	6,00	8,00	TODO PERÍODO	TODO PERÍODO	-	ÚNICA
TENDA BANHEIRO QUÍMICO E BEBEDOURO (LOG)	1	3,00	3,00	-	TODO PERÍODO	TODO PERÍODO	ÚNICA
TENDA CENTRAL DE KITS (LOG)	1	10,00	6,00	-	TODO PERÍODO	TODO PERÍODO	ÚNICA
TENDA CENTRAL DE PORTAS (LOG)	1	6,00	8,00	-	TODO PERÍODO	TODO PERÍODO	ÚNICA
TENDA LAZER (LOG)	1	6,00	10,00	-	TODO PERÍODO	TODO PERÍODO	ÚNICA
TENDA MOLDADOR (LOG)	1	3,00	4,00	TODO PERÍODO	TODO PERÍODO	-	ÚNICA

LOG_EQUIPAMENTOS E MAQUINÁRIOS

EQUIPAMENTO	QUANTIDADE	MOBILIZAÇÃO	DESMOBILIZAÇÃO	PRÉ FORMA	ESTRUTURA	ACABAMENTO	FASE
BETONEIRA (LOG)	VARIÁVEL	-	-	TODO PERÍODO	TODO PERÍODO	-	ÚNICA
BOBCAT (LOG)	1 EQUIPAMENTO	1 MOBILIZAÇÃO	1 DESMOBILIZAÇÃO	-	TODO PERÍODO	CONSIDERAR 15 DIAS DO PERÍODO DE ACABAMENTO	ÚNICA
BOMBA ESTACIONÁRIA PADRÃO (LOG)_R01	VARIÁVEL	-	-	-	TODO PERÍODO	-	ÚNICA
CAMINHÃO MUNCK (LOG)	1 EQUIPAMENTO	1 MOBILIZAÇÃO	1 DESMOBILIZAÇÃO	-	CONSIDERAR MEIO PERÍODO DE ESTRUTURA	-	ÚNICA
CREMALHEIRA PCT (LOG)	2 EQUIPAMENTOS	1 MOB DE CREMALHEIRA POR TORRE (TAKT 2X2)	1 DESMOB DE CREMALHEIRA POR TORRE (TAKT 2X2)	-	TODO PERÍODO	TODO PERÍODO	ÚNICA
MINIGRUA (LOG)	2 EQUIPAMENTOS	1 MOB POR MINIGRUA POR TORRE (TAKT 2X2)	1 DESMOB POR MINIGRUA POR TORRE (TAKT 2X2)	-	TODO PERÍODO	-	ÚNICA
PERFURATRIZ (LOG)	1 EQUIP	1 MOBILIZAÇÃO	1 DESMOBILIZAÇÃO	CONSIDERAR PERÍODO DE ESTACA CONFORME PROJETO.	-	-	ÚNICA

LOG_TELA FACHADEIRA E SLQA

TIPO	BLOCO	ESTRUTURA	ACABAMENTO	PRAZO DE UTILIZAÇÃO	ÁREA	FASE	CÓDIGO ORÇAMENTO
SLQA (LOG)	BLOCO 01	TODO PERÍODO	-	1,5 MESES	883,35 m²	ÚNICA	
SLQA (LOG)	BLOCO 02	TODO PERÍODO	-	1,3 MESES	792,62 m²	ÚNICA	

Logística – Cond. 02

MODULAÇÃO CEF E TOMBAMENTO
1 : 700

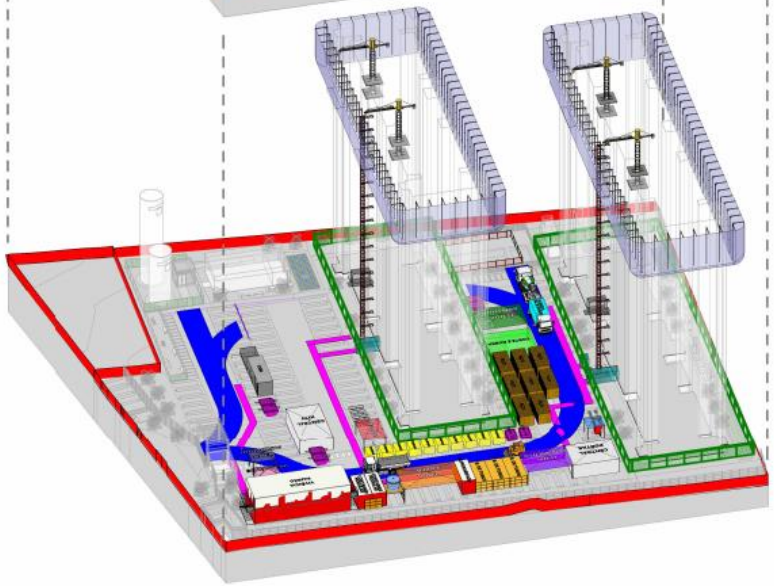

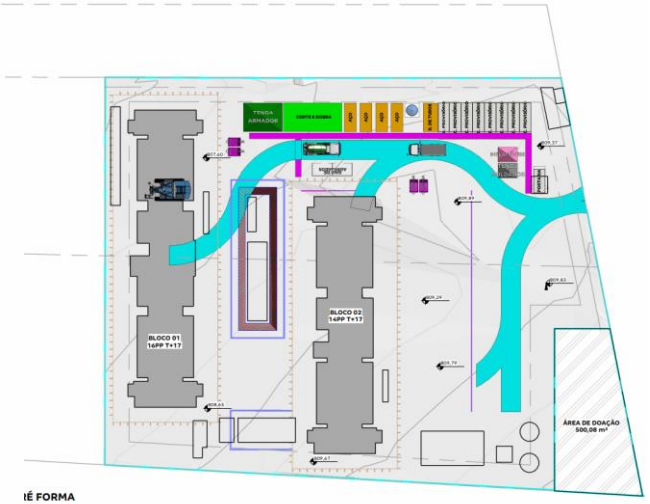

TÉ FORMA
500

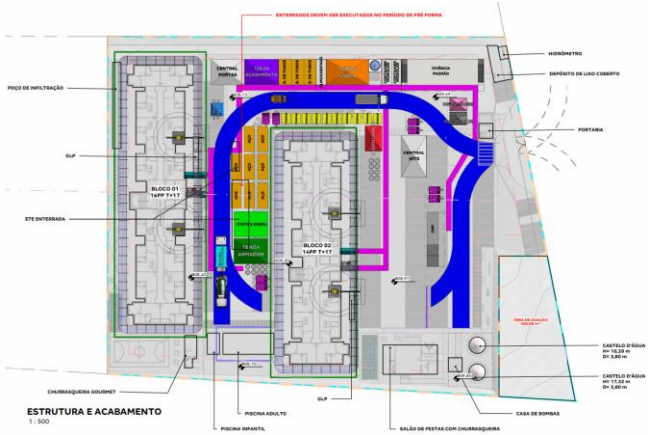

ESTRUTURA E ACABAMENTO
1 : 500

LOG_VIVÊNCIA - CONTAINERS

DESCRIÇÃO	QUANTIDADE	TAMANHO MÓDULOS	MOBILIZAÇÃO	DESMOBILIZAÇÃO	PRÉ FORMA	ESTRUTURA	ACAB.	FASE
CONTAINER ALMOXARIFADO (LOG)	1 MÓDULO DE CONTAINER	2,41 X 6,10 m	1 MOBILIZAÇÃO	1 DESMOBILIZAÇÃO	-	TODO PERÍODO	TODO PERÍODO	ÚNICA
CONTAINER MODULAR (LOG)	1 MÓDULO DE CONTAINER	2,41 X 6,10 m	1 MOBILIZAÇÃO	1 DESMOBILIZAÇÃO	-	TODO PERÍODO	TODO PERÍODO	ÚNICA
CONTAINER PORTARIA (LOG)	CONSIDERAR 1 MÓDULO COM SANITÁRIO E CATRACA	2,41 X 4,90 m	1 MOBILIZAÇÃO	1 DESMOBILIZAÇÃO	TODO PERÍODO	-	TODO PERÍODO	ÚNICA
CONTAINER PROVISÓRIO (LOG)	CONSIDERAR 8 MÓDULOS DE CONTAINER	2,41 X 6,10 m	1 MOBILIZAÇÃO	1 DESMOBILIZAÇÃO	TODO PERÍODO	-	-	ÚNICA
CONTAINER VIVÊNCIA PADRÃO (LOG)	CONSIDERAR 14 MÓDULOS COM 2 ESCADAS (7 MÓDULOS NO PAV. T E 7 MÓDULOS NO PAV SUPERIOR)	2,41 X 6,10 m	1 MOBILIZAÇÃO	1 DESMOBILIZAÇÃO	-	TODO PERÍODO	TODO PERÍODO	ÚNICA

LOG_TENDAS_PERÍODOS

DESCRIÇÃO	QUANTIDADE	LARGURA	COMPRIMENTO	PRÉ FORMA	ESTRUTURA	ACABAMENTO	FASE
GAIOLA DE DESMOLDANTE (LOG)	1	4,00	6,00	-	TODO PERÍODO	-	ÚNICA
GAIOLA DE INFLAMÁVEIS (LOG)	1	3,00	4,00	-	TODO PERÍODO	TODO PERÍODO	ÚNICA
TENDA ACABAMENTO (LOG)	1	6,00	8,00	-	TODO PERÍODO	TODO PERÍODO	ÚNICA
TENDA ARMADOR (LOG)	2	6,00	8,00	TODO PERÍODO	TODO PERÍODO	-	ÚNICA
TENDA BANHEIRO QUÍMICO E BEBEDOURO (LOG)	1	3,00	3,00	-	TODO PERÍODO	TODO PERÍODO	ÚNICA
TENDA CENTRAL DE KITS (LOG)	1	10,00	6,00	-	TODO PERÍODO	TODO PERÍODO	ÚNICA
TENDA CENTRAL DE PORTAS (LOG)	1	6,00	8,00	-	TODO PERÍODO	TODO PERÍODO	ÚNICA
TENDA LAZER (LOG)	1	6,00	10,00	-	TODO PERÍODO	TODO PERÍODO	ÚNICA
TENDA MOLDADOR (LOG)	1	3,00	4,00	TODO PERÍODO	TODO PERÍODO	-	ÚNICA

LOG_EQUIPAMENTOS E MAQUINÁRIOS

EQUIPAMENTO	QUANTIDADE	MOBILIZAÇÃO	DESMOBILIZAÇÃO	PRÉ FORMA	ESTRUTURA	ACABAMENTO	FASE
BETONEIRA (LOG)	VARIÁVEL	-	-	TODO PERÍODO	TODO PERÍODO	-	ÚNICA
BOBCAT (LOG)	1 EQUIPAMENTO	1 MOBILIZAÇÃO	1 DESMOBILIZAÇÃO	-	TODO PERÍODO	CONSIDERAR 15 DIAS DO PERÍODO DE ACABAMENTO	ÚNICA
BOMBA ESTACIONÁRIA PADRÃO (LOG)_R01	VARIÁVEL	-	-	-	TODO PERÍODO	-	ÚNICA
CAMINHÃO MUNCK (LOG)	1 EQUIPAMENTO	1 MOBILIZAÇÃO	1 DESMOBILIZAÇÃO	-	CONSIDERAR MEIO PERÍODO DE ESTRUTURA	-	ÚNICA
CREMALHEIRA PCT (LOG)	2 EQUIPAMENTOS	1 MOB DE CREMALHEIRA POR TORRE (TAKT 2X2)	1 DESMOB DE CREMALHEIRA POR TORRE (TAKT 2X2)	-	TODO PERÍODO	TODO PERÍODO	ÚNICA
MINIGRUA (LOG)	2 EQUIPAMENTOS	1 MOB POR MINIGRUA POR TORRE (TAKT 2X2)	1 DESMOB POR MINIGRUA POR TORRE (TAKT 2X2)	-	TODO PERÍODO	-	ÚNICA
PERFURATRIZ (LOG)	1 EQUIP	1 MOBILIZAÇÃO	1 DESMOBILIZAÇÃO	CONSIDERAR PERÍODO DE ESTACA CONFORME PROJETO.	-	-	ÚNICA

LOG_TELA FACHADEIRA E SLQA

TIPO	BLOCO	ESTRUTURA	ACABAMENTO	PRAZO DE UTILIZAÇÃO	ÁREA	FASE	CÓDIGO ORÇAMENTO
SLQA (LOG)	BLOCO 01	TODO PERÍODO	-	1,5 MESES	883,35 m²	ÚNICA	
SLQA (LOG)	BLOCO 02	TODO PERÍODO	-	1,3 MESES	792,62 m²	ÚNICA	

Logística – Cond. 03

MODULAÇÃO CEF E TOMBAMENTO
1 : 700

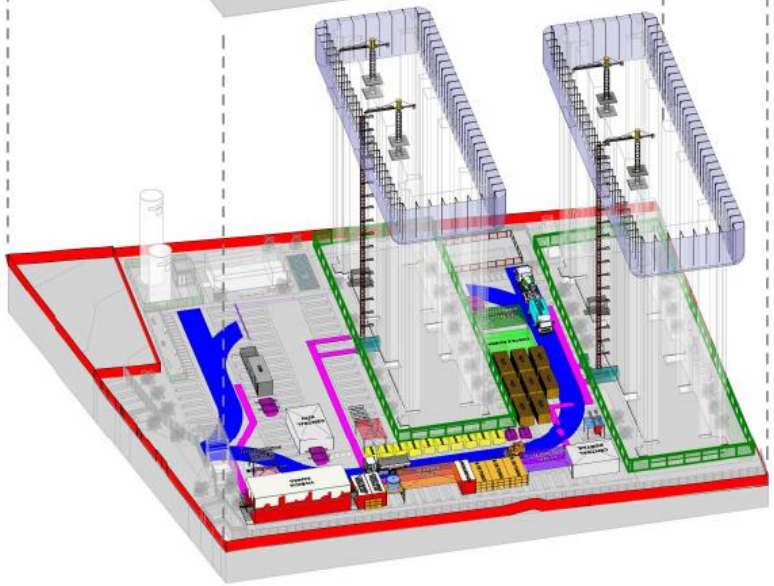

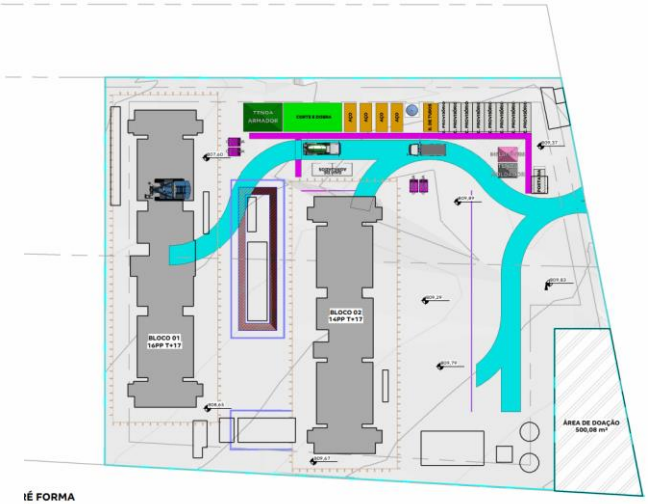

TÉ FORMA
500

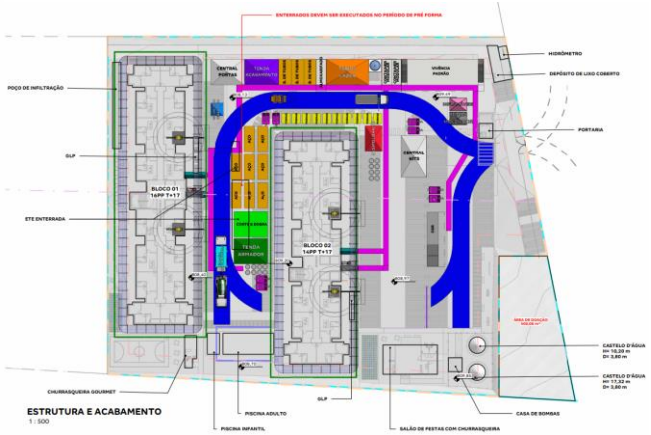

ESTRUTURA E ACABAMENTO
1 : 500

LOG_VIVÊNCIA - CONTAINERS

DESCRIÇÃO	QUANTIDADE	TAMANHO MÓDULOS	MOBILIZAÇÃO	DESMOBILIZAÇÃO	PRÉ FORMA	ESTRUTURA	ACAB.	FASE
CONTAINER ALMOXARIFADO (LOG)	1 MÓDULO DE CONTAINER	2,41 X 6,10 m	1 MOBILIZAÇÃO	1 DESMOBILIZAÇÃO	-	TODO PERÍODO	TODO PERÍODO	ÚNICA
CONTAINER MODULAR (LOG)	1 MÓDULO DE CONTAINER	2,41 X 6,10 m	1 MOBILIZAÇÃO	1 DESMOBILIZAÇÃO	-	TODO PERÍODO	TODO PERÍODO	ÚNICA
CONTAINER PORTARIA (LOG)	CONSIDERAR 1 MÓDULO COM SANITÁRIO E CATRACA	2,41 X 4,90 m	1 MOBILIZAÇÃO	1 DESMOBILIZAÇÃO	TODO PERÍODO	-	TODO PERÍODO	ÚNICA
CONTAINER PROVISÓRIO (LOG)	CONSIDERAR 8 MÓDULOS DE CONTAINER	2,41 X 6,10 m	1 MOBILIZAÇÃO	1 DESMOBILIZAÇÃO	TODO PERÍODO	-	-	ÚNICA
CONTAINER VIVÊNCIA PADRÃO (LOG)	CONSIDERAR 14 MÓDULOS COM 2 ESCADAS (7 MÓDULOS NO PAV. T E 7 MÓDULOS NO PAV SUPERIOR)	2,41 X 6,10 m	1 MOBILIZAÇÃO	1 DESMOBILIZAÇÃO	-	TODO PERÍODO	TODO PERÍODO	ÚNICA

LOG_TENDAS_PERÍODOS

DESCRIÇÃO	QUANTIDADE	LARGURA	COMPRIMENTO	PRÉ FORMA	ESTRUTURA	ACABAMENTO	FASE
GAIOLA DE DESMOLDANTE (LOG)	1	4,00	6,00	-	TODO PERÍODO	-	ÚNICA
GAIOLA DE INFLAMÁVEIS (LOG)	1	3,00	4,00	-	TODO PERÍODO	TODO PERÍODO	ÚNICA
TENDA ACABAMENTO (LOG)	1	6,00	8,00	-	TODO PERÍODO	TODO PERÍODO	ÚNICA
TENDA ARMADOR (LOG)	2	6,00	8,00	TODO PERÍODO	TODO PERÍODO	-	ÚNICA
TENDA BANHEIRO QUÍMICO E BEBEDOURO (LOG)	1	3,00	3,00	-	TODO PERÍODO	TODO PERÍODO	ÚNICA
TENDA CENTRAL DE KITS (LOG)	1	10,00	6,00	-	TODO PERÍODO	TODO PERÍODO	ÚNICA
TENDA CENTRAL DE PORTAS (LOG)	1	6,00	8,00	-	TODO PERÍODO	TODO PERÍODO	ÚNICA
TENDA LAZER (LOG)	1	6,00	10,00	-	TODO PERÍODO	TODO PERÍODO	ÚNICA
TENDA MOLDADOR (LOG)	1	3,00	4,00	TODO PERÍODO	TODO PERÍODO	-	ÚNICA

LOG_EQUIPAMENTOS E MAQUINÁRIOS

EQUIPAMENTO	QUANTIDADE	MOBILIZAÇÃO	DESMOBILIZAÇÃO	PRÉ FORMA	ESTRUTURA	ACABAMENTO	FASE
BETONEIRA (LOG)	VARIÁVEL	-	-	TODO PERÍODO	TODO PERÍODO	-	ÚNICA
BOBCAT (LOG)	1 EQUIPAMENTO	1 MOBILIZAÇÃO	1 DESMOBILIZAÇÃO	-	TODO PERÍODO	CONSIDERAR 15 DIAS DO PERÍODO DE ACABAMENTO	ÚNICA
BOMBA ESTACIONÁRIA PADRÃO (LOG)_R01	VARIÁVEL	-	-	-	TODO PERÍODO	-	ÚNICA
CAMINHÃO MUNCK (LOG)	1 EQUIPAMENTO	1 MOBILIZAÇÃO	1 DESMOBILIZAÇÃO	-	CONSIDERAR MEIO PERÍODO DE ESTRUTURA	-	ÚNICA
CREMALHEIRA PCT (LOG)	2 EQUIPAMENTOS	1 MOB DE CREMALHEIRA POR TORRE (TAKT 2X2)	1 DESMOB DE CREMALHEIRA POR TORRE (TAKT 2X2)	-	TODO PERÍODO	TODO PERÍODO	ÚNICA
MINIGRUA (LOG)	2 EQUIPAMENTOS	1 MOB POR MINIGRUA POR TORRE (TAKT 2X2)	1 DESMOB POR MINIGRUA POR TORRE (TAKT 2X2)	-	TODO PERÍODO	-	ÚNICA
PERFURATRIZ (LOG)	1 EQUIP	1 MOBILIZAÇÃO	1 DESMOBILIZAÇÃO	CONSIDERAR PERÍODO DE ESTACA CONFORME PROJETO.	-	-	ÚNICA

LOG_TELA FACHADEIRA E SLQA

TIPO	BLOCO	ESTRUTURA	ACABAMENTO	PRAZO DE UTILIZAÇÃO	ÁREA	FASE	CÓDIGO ORÇAMENTO
SLQA (LOG)	BLOCO 01	TODO PERÍODO	-	1,5 MESES	883,35 m²	ÚNICA	
SLQA (LOG)	BLOCO 02	TODO PERÍODO	-	1,3 MESES	792,62 m²	ÚNICA	

Pareceres

Análise da Mancha e Implantação

Prospecção

Operações

Inteligência de Mercado

Financeiro

Demanda e Distribuição da Mancha

Potencial de Demanda			Lançados		Lançados + Landbank	
Mancha	CÓD.	Shr.	ANO	MÊS	ANO	MÊS
Goiânia Sul + Aparecida	GOS	36%	1.805	150	2.165	180

Empreendimento	Renda	Lançamento	jan/27	fev/27	mar/27	abr/27	mai/27	jun/27	jul/27	ago/27	set/27	out/27	nov/27	dez/27	jan/28	fev/28	mar/28	abr/28	mai/28	jun/28	jul/28	ago/28	set/28	out/28
FaiçalVille	3.464	set-25	28	28	25																			
Estância Dourados II	2.437	mar-26	35	35	35	35	12																	
Videira	2.424	dez-26	23	23	23	23	23	23	23	23	23	23	23	23	18									
Presidente I	**3.654**	**jan-27**		**32**	**32**	**32**	**32**	**32**	**32**	**32**	**32**	**32**	**32**	**32**	**32**	**32**	**32**	**32**	**32**	**32**	**24**			
Presidente II	**3.654**	**jul-28**																				**32**	**32**	**32**
Presidente III - F1 e F2	**3.654**	**jan-30**																						
Total de Vendas Lançados			**0**	**0**	**0**	**0**	**0**	**0**	**0**	**0**	**0**	**0**	**0**	**0**	**0**	**0**	**0**	**0**	**0**	**0**	**0**	**0**	**0**	**0**
Total de Vendas Lançados + Landbank			**86**	**118**	**115**	**90**	**67**	**55**	**55**	**55**	**55**	**55**	**55**	**55**	**50**	**32**	**32**	**32**	**32**	**32**	**24**	**32**	**32**	**32**

Parecer de I.M sobre a mancha:

O projeto analisado em comitê está em linha com o potencial teórico de demanda calculado para a mancha. (Total Lanç + Landbank)

Canibalização:

Sem Risco de Canibalização

Presidente I | Mapa Concorrência

		Presidente I	Gran Paris	Rni Porto Ravena
		TENDA	MRV	RNI
	Distância Tenda (km)		2,37Km	2,64Km
Região 1 Km	População	11.621	8.420	14.550
	Dens. Demográfica	3.723	2.697	4.661
	Renda (R$)	6.462	7.051	13.259
	Classe Social	B2 (4.6k a 8.1k)	B2 (4.6k a 8.1k)	B1 (8.1k a 16k)
	PEA Dia	8.147	9.551	7.177
Quantitativo	Lançamento	jan/27	04/2023	06/2024
	Unidades	568	224	480
	Estoque	568	0	134
	VSO	32	16	29
	Stockout	18	0	5
Qualitativo	Condomínios	1	1	1
	Torres	2	1	1
	Gabarito	T+18	T+13	T+19
	Plantas (m²)	38m²	35,78m² e 44,7m² e 35,8m² e 42,6m² e 44,9m²	48,86m² e 46,86m² e 48,86m² e 46,86m²
	Tipologia	2 Dorms	1 e 2 Dorms	2 Dorms
	Opções	Não	Garden	Garden
	Varanda	Não	Sim	Sim
	Vagas	35% de Vagas	Com vaga	Com vaga
	Lazer	Play Kids, play baby, Play pet, piscina tamanho G. Fitness externo, churrasqueira gourmet , mini mercado.	Bosque, Fireplace, Piscina, Piscina Aquecida, Piso Elevado, Praça, Salão de Jogos,	Tem Sacada, Tem Garden, Bosque, Capela, Cinema, Lago, Pet Place, Piscina Aquecida, Piso Elevado, Praça, Quadra, Quadra de Tênis, Sala de Reuniões / Treinamentos, Salão de Jogos,

Diagnóstico Concorrência

- O empreendimento da RNI está performando preço e renda acima do estimado no parecer e possuí um produto diferente do ofertado pela Tenda, contendo opções com Varanda, Garden e Unidades com espaço para Closet.
- O empreendimento Gran Paris, já performou na região com preço e renda acima do estimado para o produto Tenda.

-	Presidente I				Gran Paris					Rni Porto Ravena				
Tipologias	Preço Nominal	CEF	Renda	% Unidades	Preço Nominal	CEF	Renda	% Unidades	Farol	Preço Nominal	CEF	Renda	% Unidades	Farol
Sem vaga	216.968	174.105	3.580	65%	254.990	203.992	4.090	-	●	-	-	-	-	-
Vg Moto	220.158	177.007	3.648	10%	-	-	-	-	-	-	-	-	-	-
Vg Carro	230.470	185.634	3.853	24%	-	-	-	-	-	-	-	-	-	-
Varanda	-	-	-	-	273.990	219.192	-	-	-	296.018	236.814	5.800	-	-
Varanda | Closet	-	-	-	-	-	-	-	-	-	330.584	264.467	6.400	-	-
Garden	-	-	-	-	269.990	215.992	-	-	-	296.018	236.814	5.800	-	-

Farol Renda
● Acima de 300
● Entre 0 e 300
● Abaixo de 0

Simulação de Preço

Informações Viabilidade

Projeto:	Presidente I					
Tipo:	**Sem vaga**		**Vaga moto**		**Vaga carro**	
Método	**Vision**		**Vision**		**Vision**	
Avaliação	216.900		220.800		236.800	
Renda Inicial (VF)	3.580		3.648		3.853	
Renda Final*	-		-		-	
% RET1	25%		25%		0%	
Tipo:	**VF**	**R$**	**VF**	**R$**	**VF**	**R$**
Ato	0,62	2.176	0,61	2.176	0,83	3.114
FGTS	0,62	2.182	0,61	2.182	1,03	3.858
Financiamento	99,40%	168.372	99,40%	171.400	96,77%	178.416
Subsídio	146,87%	3.551	152,98%	3.426	165,81%	3.360
Prazo de Pró-soluto	24	24	24	24	24	24
Pró-Soluto	74,45%	23.241	74,53%	23.710	73,71%	24.764
Preço Raso (RS)	199.522	199.522	202.893	202.893	213.512	213.512
TCD	48,34%	17.446	46,95%	17.265	43,66%	16.958
VSO	21	21	3	3	8	8
Preço de Venda	**222.260**	**222.260**	**225.527**	**225.527**	**236.092**	**236.092**
Elasticidade	-2,381%	-2,381%	-2,381%	-2,381%	-2,381%	-2,381%
Preço de Venda Final	**216.968**	**216.968**	**220.158**	**220.158**	**230.470**	**230.470**
Preço Raso (R$)	**199.522**		**202.893**		**213.512**	
% de Raso	**91,96%**		**92,16%**		**92,64%**	
BP25 - Não Inflacionado	-		-		-	
BP25 - Inflacionado	-		-		-	

Análise de Preço

Informações Viabilidade

Projeto:	Presidente I
Tipo:	**Faixa 2**
Método	**Vision**
Avaliação	222.161
Renda Inicial (VF)	3.654
Renda Final*	-

Tipo:	VF	R$
Ato	0,67	2.406
FGTS	0,72	2.592
Financiamento	98,76%	171.134
Subsídio	152,12%	3.492
Prazo de Pró-soluto	24	24
Pró-Soluto	74,28%	23.661
Preço Raso (RS)	203.284	203.284
TCD	47,06%	17.308
VSO	32	32
Preço de Venda	**225.845**	**225.845**
Elasticidade	-2,381%	-2,381%
Preço de Venda Final	**220.592**	**220.592**
Preço Raso (R$)	**203.284**	
% de Raso	**92,15%**	
Raso Todas as Fases	**205.281**	
Nominal Todas as Fases	**222.693**	

1

Análise de Riscos | Farol IM

IM avalia o Preço Vision como **factível**.

1) I.M está de acordo com o preço Vision, tendo em vista que, o projeto está em uma região com bons indicadores sociodemográficos, como renda e PEA/Dia. A diferença de preço e renda entre o Presidente e o Estância Dourados, produto referência da região, se justifica pelo incremento da piscina, verticalização e melhor localização.

Conforme consta no slide "Panorama de Concorrência", os concorrentes mapeados atuam com preços superiores ao projetado para o produto Tenda.

	Preço Real					Preço Normalizado (24m)	
	Avaliação	Preço Raso	Renda Média	VSO	PSOL	Δ PSOL	Preço Raso
Estância Dourado	**211.155**	**189.082**	**2.799**	**52**	**17**	**7.196**	**196.278**
Presidente I	**222.161**	**203.284**	**3.654**	**32**	**24**	**-**	**203.284**

Simulação de Preço – Fases Futuras

Vision

Nome Fase	Tipologia	Renda	Ato	FGTS	Cond.	Subsídio	PSOL	TCD	VSO	Nom. Pré	Avali.	Elast.	Nom. Pós	Raso Pós	PSOL (m)	RET1
Presidente II	Vaga carro	3.964	0,80	1,00	96,8%	166,7%	71,6%	42,4%	8	236.092	236.800	-2,3810%	230.470	213.512	24	0%
Presidente II	Sem vaga	3.580	0,62	0,62	99,4%	146,9%	74,4%	48,3%	21	222.260	216.900	-2,3810%	216.968	199.522	24	25%
Presidente II	Vaga moto	3.648	0,61	0,61	99,4%	153,0%	74,5%	47,0%	3	225.527	220.800	-2,3810%	220.158	202.893	24	25%
Presidente III - F1	Vaga carro	3.580	0,89	1,10	96,8%	139,0%	80,5%	47,7%	5	238.206	236.800	-0,8772%	236.116	218.896	26	25%
Presidente III - F1	Sem vaga	3.580	0,62	0,62	99,4%	146,9%	75,6%	49,1%	13	224.244	216.900	-0,8772%	222.277	204.563	26	25%
Presidente III - F1	Vaga moto	3.648	0,61	0,61	99,4%	153,0%	75,7%	47,7%	2	227.551	220.800	-0,8772%	225.555	208.024	26	25%
Presidente III - F2	Vaga carro	3.580	0,89	1,10	96,8%	139,0%	80,5%	47,7%	5	238.206	236.800	-0,8772%	236.116	218.896	26	25%
Presidente III - F2	Sem vaga	3.580	0,62	0,62	99,4%	146,9%	75,6%	49,1%	13	224.244	216.900	-0,8772%	222.277	204.563	26	25%
Presidente III - F2	Vaga moto	3.648	0,61	0,61	99,4%	153,0%	75,7%	47,7%	2	227.551	220.800	-0,8772%	225.555	208.024	26	25%

PRESIDENTE

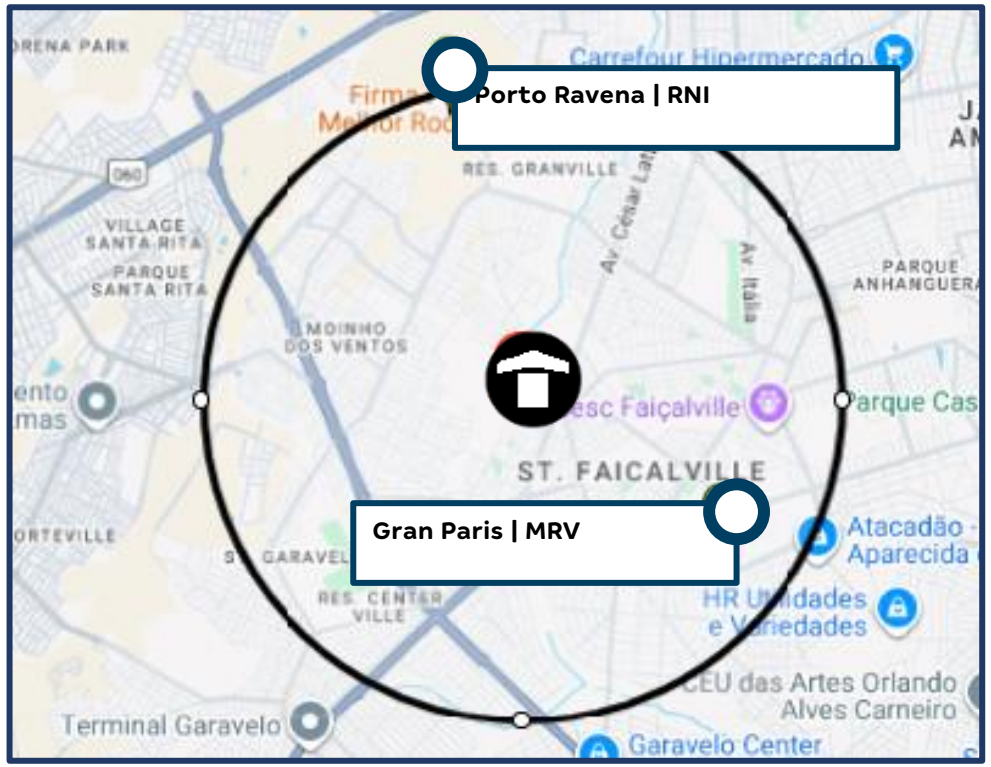

Análise de Riscos	Farol IM
Ciclo Financeiro avalia o Preço Referência como **factível**.	

1) O Ciclo Financeiro está de acordo com a precificação de referência.

2) Temos concorrência direta da MRV e RNI na região do produto, contudo ambos os produtos estão em final de estoque.

*São considerados apenas as unidades dos concorrentes que estão alinhadas com o produto Tenda

Pareceres

Análise da Mancha e Implantação

Prospecção

Operações

Inteligência de Mercado

Financeiro

Informações Gerais – PRESIDENTE

Presidente - GO - Goiânia Capital

Datas e Prazos

	Compra	Lançamento	Início Obra	Término Obra	LÇTO até IO	IO até TO	Chaves	LÇTO até Chaves
Consolidado	mai-25							
Presidente 1 c/ vaga carro		jan-27	jul-27	fev-29	6 meses	19 meses	jan-30	36 meses
Presidente 1 s/ vaga		jan-27	jul-27	fev-29	6 meses	19 meses	jan-30	36 meses
Presidente 1 c/ vaga moto		jan-27	jul-27	fev-29	6 meses	19 meses	jan-30	36 meses
Presidente 2 c/ vaga carro		jul-28	jan-29	ago-30	6 meses	19 meses	jul-31	36 meses
Presidente 2 s/ vaga		jul-28	jan-29	ago-30	6 meses	19 meses	jul-31	36 meses
Presidente 2 c/ vaga moto		jul-28	jan-29	out-30	6 meses	21 meses	jul-31	36 meses
Presidente 3 c/ vaga carro - F1		jan-30	jul-30	abr-32	6 meses	21 meses	jan-33	36 meses
Presidente 3 s/ vaga - F1		jan-30	jul-30	abr-32	6 meses	21 meses	jan-33	36 meses
Presidente 3 c/ vaga moto -F1		jan-30	jul-30	abr-32	6 meses	21 meses	jan-33	36 meses
Presidente 3 c/ vaga carro - F2		jul-31	jan-32	out-33	6 meses	21 meses	jul-34	36 meses
Presidente 3 s/ vaga -F2		jul-31	jan-32	out-33	6 meses	21 meses	jul-34	36 meses
Presidente 3 c/ vaga moto- F2		jul-31	jan-32	out-33	6 meses	21 meses	jul-34	36 meses

Terreno e Incorridos

TOTAL (R$ + Perm.):	34,72 MM	**Incorrido Terreno:**	0,00 MM	**Área do Terreno (100%):**	35.059 m²	**Área Líquida do Terreno:**	35.059 m²
Cash:	0,50 MM	**Nº de Parcelas Cash :**	1	**Custo de terreno m²:**	990,4	**Custo de terreno m² Área Líquida:**	990,4
Permuta Financeira:	34,22 MM (8,28%)			**VaR 25 (R$ mil):**	500	**Fração Terreno/Terreno + Custo Obra (%VGV):**	8,4% / 50,1%
Permuta Física:	0,00 MM (0,00%)			**VaR 26 (R$ mil):**	500	**CA Máx/Proj.**	6,0 / 3,3
Ato / %VGV:	0,00 MM / 0,0%			**Incorrido de Construção:**	0,00 MM	**Incorridos de Incorporação:**	0,00 MM

Vendas

Fases	Nº Pavimentos	Preço Raso Unit.	Qtde	Preço Unit.	Aval. CEF	Cond. Parcela	% Pró-soluto	% TCD
Presidente 1 c/ vaga carro	T+18	213.512	139	230.470	236.800	96,8%	73,7%	43,7%
Presidente 1 s/ vaga	T+18	199.522	372	216.968	216.900	99,4%	74,4%	48,3%
Presidente 1 c/ vaga moto	T+18	202.893	57	220.158	220.800	99,4%	74,5%	47,0%
Presidente 2 c/ vaga carro	T+18	213.512	139	230.470	236.800	96,8%	71,6%	42,4%
Presidente 2 s/ vaga	T+18	199.522	372	216.968	216.900	99,4%	74,4%	48,3%
Presidente 2 c/ vaga moto	T+18	204.869	57	220.158	220.800	99,4%	74,5%	47,0%
Presidente 3 c/ vaga carro - F1	T+18	218.896	88	236.116	236.800	96,8%	80,5%	47,7%
Presidente 3 s/ vaga - F1	T+18	204.563	236	222.277	216.900	99,4%	75,6%	49,1%
Presidente 3 c/ vaga moto -F1	T+18	208.024	36	225.555	220.800	99,4%	75,7%	47,7%
Presidente 3 c/ vaga carro - F2	T+18	218.896	88	236.116	236.800	96,8%	80,5%	47,7%
Presidente 3 s/ vaga -F2	T+18	204.563	236	222.277	216.900	99,4%	75,6%	49,1%
Presidente 3 c/ vaga moto- F2	T+18	208.024	36	225.555	220.800	99,4%	75,7%	47,7%

Unidades Totais:	1.856	**Preço Médio:**	222.685	**Renda Média:**	3.636	**ITBI+Emol. Unit. Médio:**	7.938
Unidades Tenda:	1.856	**Avaliação Média:**	222.159	**Ato:**	2.458 (0,68 Salários)	**Custo do Ciclo Unit.:**	14.585
VSO:	26 Unidades	**VGV Total:**	413.303.915	**FGTS:**	2.642 (0,73 Salários)	**Preço Raso Médio:**	205.334
RET Médio:	3,8%	**VGV Tenda:**	413.303.915	**% em RET 1%:**	6%	**Adc. Tx. de Aceleração Médio:**	774

Construção

Custo Total Unit.:	92.968	**Eventuais:**	4,00%	**Área priv (m²):**	32,00	**Gape / Mês Unit.:**	11,08

Resultado

LI (R$):	**46.918.735**	**LI:**	**23,07%**	**Exposição de Caixa (R$):**	**14.916.412**	**Margem Bruta Econômica:**	**45,06%**
TIR:	**123,98%**	**LI Aprovação:**	**20,00%**	**Ger. Caixa 12 meses (R$):**	**(514.960)**	**Margem Bruta REF:**	**48,44%**
Exposição de Caixa:	**3,08%**	**Δ LI:**	**3,07%**	**Ger. Caixa 24 meses (R$):**	**(7.939.554)**	**Margem Rasa Econômica:**	**39,85%**
Payback Contingente (21 m):	**19 m/ (-2 m)**	**LI Resiliência:**	**17,05%**	**Ger. Caixa Marginal (R$):**	**141.347.236**	**Margem Rasa REF:**	**44,09%**
Payback Consolidado:	**19 meses**					**Margem de Contribuição Econômica:**	**31,54%**

DRE

R$ Mil - Valores Nominais - Compra	Presidente		Presidente 1 c/ vaga carro		Presidente 1 s/ vaga		Presidente 1 c/ vaga moto		Presidente 2 c/ vaga carro		Presidente 2 s/ vaga		Presidente 2 c/ vaga moto		Presidente 3 c/ vaga carro - F1		Presidente 3 s/ vaga - F1		Presidente 3 c/ vaga moto - F1		Presidente 3 c/ vaga carro - F2		Presidente 3 s/ vaga -F2		Presidente 3 c/ vaga moto- F2	
	Nominal	%	Nominal	%	Nominal	%	Nominal	%	Nominal	%	Nominal	%	Nominal	%	Nominal	%	Nominal	%	Nominal	%	Nominal	%	Nominal	%	Nominal	%
Receita	484.793	100,0%	34.084	100,0%	85.880	100,0%	13.317	100,0%	36.672	100,0%	92.401	100,0%	14.329	100,0%	25.603	100,0%	64.641	100,0%	10.005	100,0%	27.547	100,0%	69.549	100,0%	10.765	100,0%
PIS/COFINS	(10.210)	2,1%	(746)	2,2%	(1.528)	1,8%	(237)	1,8%	(803)	2,2%	(2.024)	2,2%	(314)	2,2%	(561)	2,2%	(1.416)	2,2%	(219)	2,2%	(603)	2,2%	(1.523)	2,2%	(236)	2,2%
Custo Total	(260.740)	54,9%	(19.561)	58,7%	(51.692)	61,3%	(7.966)	60,9%	(18.945)	52,8%	(50.293)	55,6%	(7.711)	55,0%	(12.348)	49,3%	(32.954)	52,1%	(5.070)	51,8%	(13.286)	49,3%	(35.462)	52,1%	(5.453)	51,8%
Custo Terreno	(28.286)	6,0%	(3.669)	11,0%	(9.203)	10,9%	(1.430)	10,9%	(1.999)	5,6%	(4.969)	5,5%	(707)	5,0%	(776)	3,1%	(1.963)	3,1%	(304)	3,1%	(833)	3,1%	(2.107)	3,1%	(326)	3,1%
Custo Relacionados a Terreno	(2.648)	0,6%	(275)	0,8%	(698)	0,8%	(108)	0,8%	(210)	0,6%	(533)	0,6%	(83)	0,6%	(93)	0,4%	(238)	0,4%	(37)	0,4%	(94)	0,4%	(242)	0,4%	(37)	0,4%
Custos de Incorporação	(5.390)	1,1%	(333)	1,0%	(893)	1,1%	(159)	1,2%	(376)	1,0%	(1.008)	1,1%	(180)	1,3%	(280)	1,1%	(724)	1,1%	(147)	1,5%	(314)	1,2%	(816)	1,2%	(161)	1,5%
Custo de Construção	(224.415)	47,3%	(15.283)	45,8%	(40.898)	48,5%	(6.269)	47,9%	(16.361)	45,6%	(43.783)	48,4%	(6.741)	48,1%	(11.199)	44,7%	(30.029)	47,5%	(4.583)	46,8%	(12.044)	44,7%	(32.297)	47,5%	(4.928)	46,8%
Lucro Bruto Econômico	213.843	45,1%	13.776	41,3%	32.660	38,7%	5.115	39,1%	16.923	47,2%	40.084	44,4%	6.304	45,0%	12.694	50,7%	30.272	47,9%	4.717	48,2%	13.657	50,7%	32.564	47,9%	5.077	48,2%
Custo para Rateio	-	0,0%	-	0,0%	-	0,0%	-	0,0%	-	0,0%	-	0,0%	-	0,0%	-	0,0%	-	0,0%	-	0,0%	-	0,0%	-	0,0%	-	0,0%
Lucro Bruto Contábil	213.843	45,1%	13.776	41,3%	32.660	38,7%	5.115	39,1%	16.923	47,2%	40.084	44,4%	6.304	45,0%	12.694	50,7%	30.272	47,9%	4.717	48,2%	13.657	50,7%	32.564	47,9%	5.077	48,2%
Despesas de Selling	(52.991)	11,2%	(3.719)	11,2%	(9.425)	11,2%	(1.464)	11,2%	(4.002)	11,2%	(10.140)	11,2%	(1.575)	11,2%	(2.768)	11,1%	(7.060)	11,2%	(1.090)	11,1%	(2.979)	11,1%	(7.597)	11,2%	(1.173)	11,1%
Contingência	(11.150)	2,3%	(784)	2,4%	(1.975)	2,3%	(306)	2,3%	(843)	2,4%	(2.125)	2,4%	(330)	2,4%	(589)	2,4%	(1.487)	2,4%	(230)	2,4%	(634)	2,4%	(1.600)	2,4%	(248)	2,4%
Margem de Contribuição	149.701	31,5%	9.273	27,8%	21.260	25,2%	3.345	25,6%	12.078	33,7%	27.819	30,8%	4.400	31,4%	9.337	37,3%	21.724	34,4%	3.397	34,7%	10.045	37,3%	23.367	34,4%	3.656	34,7%
IR e CSLL	(8.354)	1,7%	(611)	1,8%	(1.250)	1,5%	(194)	1,5%	(657)	1,8%	(1.656)	1,8%	(257)	1,8%	(459)	1,8%	(1.158)	1,8%	(179)	1,8%	(494)	1,8%	(1.246)	1,8%	(193)	1,8%
Margem Líquida	141.347	29,8%	8.662	26,0%	20.010	23,7%	3.151	24,1%	11.421	31,8%	26.163	28,9%	4.143	29,6%	8.878	35,5%	20.566	32,5%	3.217	32,9%	9.551	35,4%	22.121	32,5%	3.464	32,9%
Lucro Bruto REF Unit.	130.615	48,4%	113.582	44,9%	100.719	42,3%	104.265	43,1%	137.223	50,4%	122.573	47,8%	127.172	48,8%	161.431	53,8%	144.443	51,1%	148.450	51,8%	173.558	53,7%	155.282	51,0%	159.591	51,7%
Lucro Raso REF Unit.	109.640	44,1%	94.997	40,5%	81.588	37,2%	85.292	38,2%	117.226	46,5%	101.989	43,3%	109.097	45,0%	139.567	50,1%	121.942	46,9%	126.191	47,7%	150.034	50,1%	131.072	46,8%	135.642	47,6%

R$ Mil - VPL - Compra	Presidente		Presidente 1 c/ vaga carro		Presidente 1 s/ vaga		Presidente 1 c/ vaga moto		Presidente 2 c/ vaga carro		Presidente 2 s/ vaga		Presidente 2 c/ vaga moto		Presidente 3 c/ vaga carro - F1		Presidente 3 s/ vaga - F1		Presidente 3 c/ vaga moto - F1		Presidente 3 c/ vaga carro - F2		Presidente 3 s/ vaga -F2		Presidente 3 c/ vaga moto- F2	
	VP	%	VP	%	VP	%	VP	%	VP	%	VP	%	VP	%	VP	%	VP	%	VP	%	VP	%	VP	%	VP	%
Receitas	203.332	100,0%	19.876	100,0%	49.819	100,0%	7.660	100,0%	16.449	100,0%	41.230	100,0%	6.292	100,0%	8.698	100,0%	21.853	100,0%	3.376	100,0%	7.198	100,0%	18.085	100,0%	2.794	100,0%
PIS/COFINS	(4.153)	2,0%	(429)	2,2%	(873)	1,8%	(134)	1,8%	(355)	2,2%	(889)	2,2%	(136)	2,2%	(188)	2,2%	(471)	2,2%	(73)	2,2%	(155)	2,2%	(390)	2,2%	(60)	2,2%
Custos e Despesas Totais	(152.260)	74,9%	(15.094)	75,9%	(39.369)	79,0%	(6.058)	79,1%	(11.725)	71,3%	(30.778)	74,6%	(4.667)	74,2%	(5.968)	68,6%	(15.738)	72,0%	(2.425)	71,8%	(5.057)	70,3%	(13.328)	73,7%	(2.053)	73,5%
Custo Terreno	(14.585)	7,2%	(2.022)	10,2%	(5.065)	10,2%	(781)	10,2%	(962)	5,9%	(2.395)	5,8%	(341)	5,4%	(371)	4,3%	(941)	4,3%	(145)	4,3%	(398)	5,5%	(1.008)	5,6%	(156)	5,6%
Custo Relacionados a Terreno	(1.789)	0,9%	(216)	1,1%	(547)	1,1%	(85)	1,1%	(142)	0,9%	(362)	0,9%	(56)	0,9%	(48)	0,5%	(122)	0,6%	(19)	0,6%	(48)	0,7%	(124)	0,7%	(19)	0,7%
Custos de Incorporação	(2.898)	1,4%	(243)	1,2%	(638)	1,3%	(114)	1,5%	(215)	1,3%	(566)	1,4%	(101)	1,6%	(126)	1,5%	(327)	1,5%	(65)	1,9%	(122)	1,7%	(319)	1,8%	(60)	2,2%
Custo de Construção	(101.077)	49,7%	(9.497)	47,8%	(25.414)	51,0%	(3.895)	50,9%	(7.825)	47,6%	(20.939)	50,8%	(3.173)	50,4%	(4.057)	46,6%	(10.878)	49,8%	(1.660)	49,2%	(3.358)	46,7%	(9.004)	49,8%	(1.375)	49,2%
Despesas de Selling	(26.059)	12,8%	(2.525)	12,7%	(6.386)	12,8%	(979)	12,8%	(2.091)	12,7%	(5.287)	12,8%	(810)	12,9%	(1.109)	12,7%	(2.823)	12,9%	(435)	12,9%	(918)	12,8%	(2.337)	12,9%	(360)	12,9%
Contingência	(2.455)	1,2%	(240)	1,2%	(605)	1,2%	(94)	1,2%	(199)	1,2%	(501)	1,2%	(75)	1,2%	(104)	1,2%	(262)	1,2%	(41)	1,2%	(86)	1,2%	(217)	1,2%	(34)	1,2%
IR e CSLL	(3.398)	1,7%	(351)	1,8%	(714)	1,4%	(110)	1,4%	(290)	1,8%	(728)	1,8%	(111)	1,8%	(153)	1,8%	(386)	1,8%	(60)	1,8%	(127)	1,8%	(319)	1,8%	(49)	1,8%
Lucro Imobiliário	46.919	23,1%	4.354	21,9%	9.577	19,2%	1.468	19,2%	4.370	26,6%	9.563	23,2%	1.489	23,7%	2.543	29,2%	5.644	25,8%	878	26,0%	1.986	27,6%	4.367	24,1%	681	24,4%

DRE

R$ Mil - Valores Nominais - Compra	Presidente		Primeira Fase		Demais Fases	
	Nominal	%	Nominal	%	Nominal	%
Receita	484.793	100,0%	133.281	100,0%	351.512	100,0%
PIS/COFINS	(10.210)	2,1%	(2.512)	1,9%	(7.699)	2,2%
Custo Total	(260.740)	54,9%	(79.218)	60,6%	(181.521)	52,8%
Custo Terreno	(28.286)	6,0%	(14.302)	10,9%	(13.984)	4,1%
Custo Relacionados a Terreno	(2.648)	0,6%	(1.082)	0,8%	(1.566)	0,5%
Custos de Incorporação	(5.390)	1,1%	(1.384)	1,1%	(4.006)	1,2%
Custo de Construção	(224.415)	47,3%	(62.450)	47,8%	(161.965)	47,1%
Lucro Bruto Econômico	213.843	45,1%	51.551	39,4%	162.292	47,2%
Custo para Rateio	-	0,0%	-	0,0%	-	0,0%
Lucro Bruto Contábil	213.843	45,1%	51.551	39,4%	162.292	47,2%
Despesas de Selling	(52.991)	11,2%	(14.608)	11,2%	(38.383)	11,2%
Contingência	(11.150)	2,3%	(3.065)	2,3%	(8.085)	2,4%
Margem de Contribuição	149.701	31,5%	33.878	25,9%	115.823	33,7%
IR e CSLL	(8.354)	1,7%	(2.055)	1,6%	(6.299)	1,8%
Margem Líquida	141.347	29,8%	31.823	24,3%	109.524	31,9%
Lucro Bruto REF Unit.	130.615	48,4%	104.223	43,0%		
Lucro Raso REF Unit.	109.640	44,1%	85.241	38,2%		

R$ Mil - VPL - Compra	Presidente		Primeira Fase		Demais Fases	
	VP	%	VP	%	VP	%
Receitas	203.332	100,0%	77.356	100,0%	125.976	100,0%
PIS/COFINS	(4.153)	2,0%	(1.436)	1,9%	(2.717)	2,2%
Custos e Despesas Totais	(152.260)	74,9%	(60.521)	78,2%	(91.739)	72,8%
Custo Terreno	(14.585)	7,2%	(7.868)	10,2%	(6.717)	5,3%
Custo Relacionados a Terreno	(1.789)	0,9%	(848)	1,1%	(941)	0,7%
Custos de Incorporação	(2.898)	1,4%	(996)	1,3%	(1.902)	1,5%
Custo de Construção	(101.077)	49,7%	(38.807)	50,2%	(62.270)	49,4%
Despesas de Selling	(26.059)	12,8%	(9.890)	12,8%	(16.169)	12,8%
Contingência	(2.455)	1,2%	(938)	1,2%	(1.516)	1,2%
IR e CSLL	(3.398)	1,7%	(1.175)	1,5%	(2.223)	1,8%
Lucro Imobiliário	46.919	23,1%	15.399	19,9%	31.520	25,0%

Obrigado