Tenda

sua próxima conquista

Book de Lançamento

Regional: RJ

Projeto: Porto Lima & Porto Seleta

Data Comitê: 16/03/2026

One Page Aprovação – Porto Lima

[1]

Cidade	Rio de Janeiro	Mancha de demanda	RJ - RZO3/4 - Campo Grande
Regional	RJ	Cluster MPR	1 - Vermelho
Cenário de Aprovação	Aprovação	Tipo de Aprovação	Consolidado
Fase Anterior	N/A		
Tipo de Comitê	Lançamento	Versão da VF	Versão 1.0: Mar

[2]

Unidades (Fases)	907 (2)	CA Máx | Proj	3,0 | 1,6
Unidades com Vaga (%)	104 (11%)	Escritura | Lançamento	mar/26 | mar/26
Unidades com Varandas (%)	0 (0%)	Tipologia	F2 - Concreto

[3]

Valor Líquido do Terreno (% VGV)	8.500 (4,4%)	Un. Perm. Fís (% Ter)	0 (0,0%)
Cash (Correção)	8.500 (IPCA)	%VGV Perm Fin Líquida (% Ter)	0,0% (0,0%)

[4]

Valor R$/m²	371	VAR (%VGV)	1334 (0,7%)

Custo Construção (%VGV)	88.708 (46,4%)	Indireto Unit.	17.998
Prazo da Obra (meses)	12	Torre Unit.	45.017
Custo Total Unit. (LPU):	97.804 (100)	Infra Unit.	20.345
Início de Obra	set-26	Fundação Unit.	7.234
Custo Adc. de Equip. e Amb. (# de Amb.):	32.314 (3)	Custo Adc. Selling:	-0,4%

Preço Nominal Unit.	210.643	VSO	35
Preço Raso Unit.	185.785	Referência	Referência
Avaliação Unit.	206.720	Renda (% em RET 1%)	2.535 (72,1%)

[5]

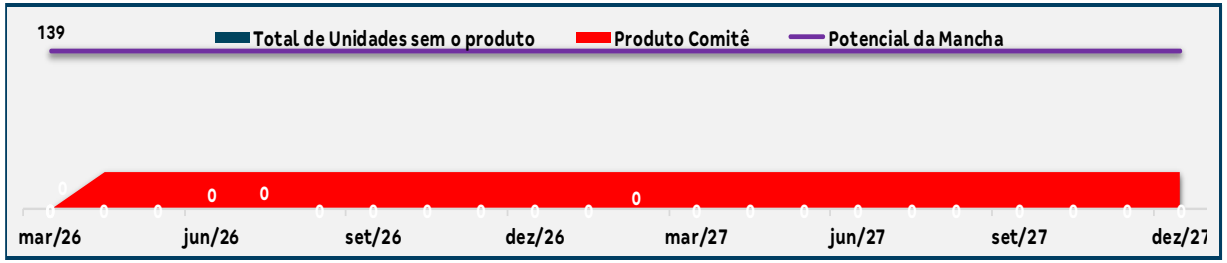

LI (Régua):	23,0% (22,0%)	Margem Bruta Econômica:	41,2%
LI Marginal:	24,4%	Margem Rasa Econômica:	32,4%
Margem Bruta REF:	43,0%	Margem Contribuição Econômica:	30,5%
Margem Rasa REF:	35,4%	Exposição (% VGV):	19.649 (10,0%)
TIR:	93,4%	VGV Total:	191.053
Payback Contingente (21 m) :	16 m/ (-5 m)	Ger. Caixa 12 meses (R$):	(18.086)
Payback Consolidado:	16	Ger. Caixa 24 meses (R$):	2.162

Destaques

[1] Imóvel fica localizado na mancha RZO3/4, faz divisa com os condomínios já lançados Porto Barão (300 uh's) e Porto Valência (480 uh's), próximo à Av. Brasil (principal via de acesso entre a Zona Central e Zona Oeste) e à Est. Do Mendanha (uma das principais vias de acesso de Campo Grande).

[2] O lançamento do projeto proposto é sequencial ao Porto Valência, com os condomínios Porto Lima I (434 uh's) e Porto Seleta (473 uh's), totalizando 907 uh's desenvolvidas de forma sequencial. O Porto Seleta ainda não entrou na esteira de Getec, o projeto foi parametrizado com o AP

[3] Condição do négocio: R$ 8,5 MM em cash (Fração de 4,4%), com sinal pago de R$ 350 mil em out/23 e novo sinal de R$ 350 mil pago em mai/25 e o saldo restante de R$ 7,8 MM a ser pago em 42 parcelas corrigidas pelo índice IPCA a partir da assinatura da ECV.

[4] Projeto contará com urbanização da via lateral projetada, garantindo testada e acesso para o condomínio II, devido a longa extensão dessa urbanização o custo II está maior que a média.

[5] Projeto atende critérios de LI e Payback no cenário aprovação.

One Page Real – Porto Lima

[1]

Cidade	Rio de Janeiro	**Mancha de demanda**	RJ - RZO3/4 - Campo Grande
Regional	RJ	**Cluster MPR**	1 - Vermelho
Cenário de Aprovação	Real	**Tipo de Aprovação**	Consolidado
Fase Anterior	N/A		
Tipo de Comitê	Lançamento	**Versão da VF**	Versão 1.0: Mar

[2]

Unidades (Fases)	907 (2)	**CA Máx | Proj**	3,0 | 1,6
Unidades com Vaga (%)	104 (11%)	**Escritura | Lançamento**	mar/26 | mar/26
Unidades com Varandas (%)	0 (0%)	**Tipologia**	F2 - Concreto

[3]

Valor Líquido do Terreno (% VGV)	8.500 (4,5%)	**Un. Perm. Fís (% Ter)**	0 (0,0%)
Cash (Correção)	8.500 (IPCA)	**%VGV Perm Fin Líquida (% Ter)**	0,0% (0,0%)
Valor R$/m²	371	**VAR (%VGV)**	1334 (0,7%)

[4]

Custo Construção (%VGV)	88.876 (47,6%)	**Indireto Unit.**	17.998
Prazo da Obra (meses)	12	**Torre Unit.**	45.017
Custo Total Unit. (LPU):	97.989 (100)	**Infra Unit.**	20.345
Início de Obra	nov-26	**Fundação Unit.**	7.234
Custo Adc. de Equip. e Amb. (# de Amb.):	32.314 (3)	**Custo Adc. Selling:**	-0,4%

Preço Nominal Unit.	206.061	**VSO**	45
Preço Raso Unit.	181.743	**Referência**	Referência
Avaliação Unit.	206.720	**Renda (% em RET 1%)**	2.535 (72,1%)

Fase de Lançamento - Margens Novas Vendas		**Preço Raso Inf. Médio Unit.**	123.227
Preço Inf. Médio Unit.	203.743	**Margem Bruta REF (%)**	39,9%
Custo Inf. Médio Unit.	122.406	**Margem Rasa REF (%)**	0,7%

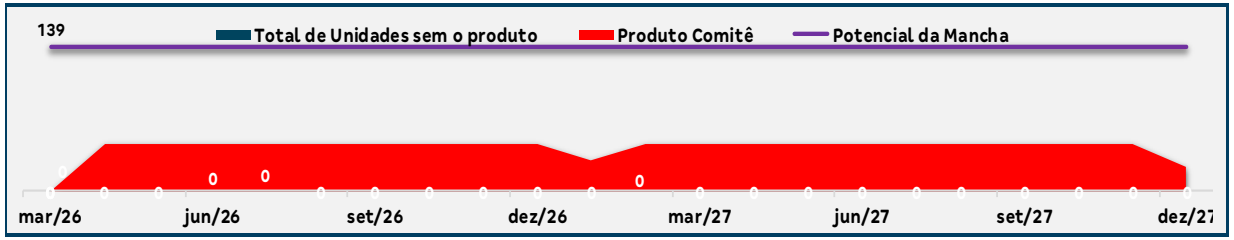

LI (Régua):	**20,5% (22,0%)**	**Margem Bruta Econômica:**	39,0%
LI Marginal:	22,0%	**Margem Rasa Econômica:**	29,6%
Margem Bruta REF:	40,1%	**Margem Contribuição Econômica:**	28,3%
Margem Rasa REF:	**32,2%**	**Exposição (% VGV):**	16.217 (8,4%)
TIR:	82,2%	**VGV Total:**	**186.897**
Payback Contingente (21 m) :	**16 m/ (-5 m)**	**Ger. Caixa 12 meses (R$):**	(13.258)
Payback Consolidado:	18	**Ger. Caixa 24 meses (R$):**	8.190

Destaques

[1] Imóvel fica localizado na mancha RZO3/4, faz divisa com os condomínios já lançados Porto Barão (300 uh's) e Porto Valência (480 uh's), próximo à Av. Brasil (principal via de acesso entre a Zona Central e Zona Oeste) e à Est. Do Mendanha (uma das principais vias de acesso de Campo Grande).

[2] O lançamento do projeto proposto é sequencial ao Porto Valência, com os condomínios Porto Lima I (434 uh's) e Porto Seleta (473 uh's), totalizando 907 uh's desenvolvidas de forma sequencial. O Porto Seleta ainda não entrou na esteira de Getec, o projeto foi parametrizado com o AP

[3] Condição do négocio: R$ 8,5 MM em cash (Fração de 4,4%), com sinal pago de R$ 350 mil em out/23 e novo sinal de R$ 350 mil pago em mai/25 e o saldo restante de R$ 7,8 MM a ser pago em 42 parcelas corrigidas pelo índice IPCA a partir da assinatura da ECV.

[4] Projeto contará com urbanização da via lateral projetada, garantindo testada e acesso para o condomínio II, devido a longa extensão dessa urbanização o custo II está maior que a média.

- Pareceres
- Análise da Mancha e Implantação
- Prospecção
- Operações
- Inteligência de Mercado
- Financeiro

Farol Pareceres – Porto Lima

Área	Riscos Associados	Parecer	Criticidade
Jurídico	A ECV foi assinada em 06/03/2026 e encontra-se em fase de registro, com previsão de conclusão para 30/03/2026. O parcelamento foi aprovado na mesma data e, juntamente com o registro da incorporação, encontra-se em fase de registro, com a mesma previsão de conclusão. **Conclusão:** Concluídos os registros da ECV, do parcelamento e da incorporação, o empreendimento estará apto para lançamento.	Ok com ressalvas	
Legalização	Projeto Legal aprovado e Licença de Obras expedida. Desmembramento aprovado. Licenciamento Ambiental encontra-se em fase final para emissão da Licença de Instalação. Licença de Recuperação Ambiental emitida. O laudo ambiental aponta a presença de benzeno em concentrações baixas e sem indícios de risco à saúde, o que deverá ser comprovado após a realização de duas campanhas de monitoramento ambiental em fev/26 e mai/26.	Ok com ressalvas	
Produto	Sem comentários.	Ok	
GETEC	Consultrix solicitou 3º campanha de sondagem para confirmação, em alguns pontos tivemos divergência entre informações comparando resultado das campanhas. Cond. 2 desenvolvido com AP, ainda não iniciou na esteira.	Ok com ressalvas	
Logística	Obrigatório uso de parte do condomínio 2 como área de apoio operacional, sem essa área não é possível realizar a obra.	Ok com ressalvas	
Contratação	**Laudo de engenharia**: Não há Laudo de engenharia, entramos com a análise definitiva em 05/03. Tempo de resposta de 20 dias corridos. **Risco: *Pendente*** *- Dependente do Laudo de Engenharia .* **Jurídico: *Pendente RI*** *- Previsão de emissão em 30/03.* Com base nessa data, a conclusão da análise jurídica está estimada para 09/04/2026.	Ok com ressalvas	
Inteligência de mercado	IM avalia o Preço Referência como **factível.**	Ok	
Comercial/Ciclo	Ciclo avalia o Preço Referência como **factível.**	Ok	
Estudos Econômicos	Ok, sem riscos associados.	Ok	

Pareceres

Análise da Mancha e Implantação

Prospecção

Operações

Inteligência de Mercado

Financeiro

Mancha de Demanda

MANCHAS DE DEMANDA

- RZO 1/6 – Rio de Janeiro Oeste

Lançamento

1. Jardim Margarida | Peônia
2. Parque Iris | Hortênsia | Orquídea
3. Porto Barão | P. Valencia
4. Reserva Carioca

LandBank

5. Vista Senna
6. Porto Lima
7. Belo Oeste

Cluster MPR – (Comitê)

Cluster 1 - Vermelho

Região

Capital

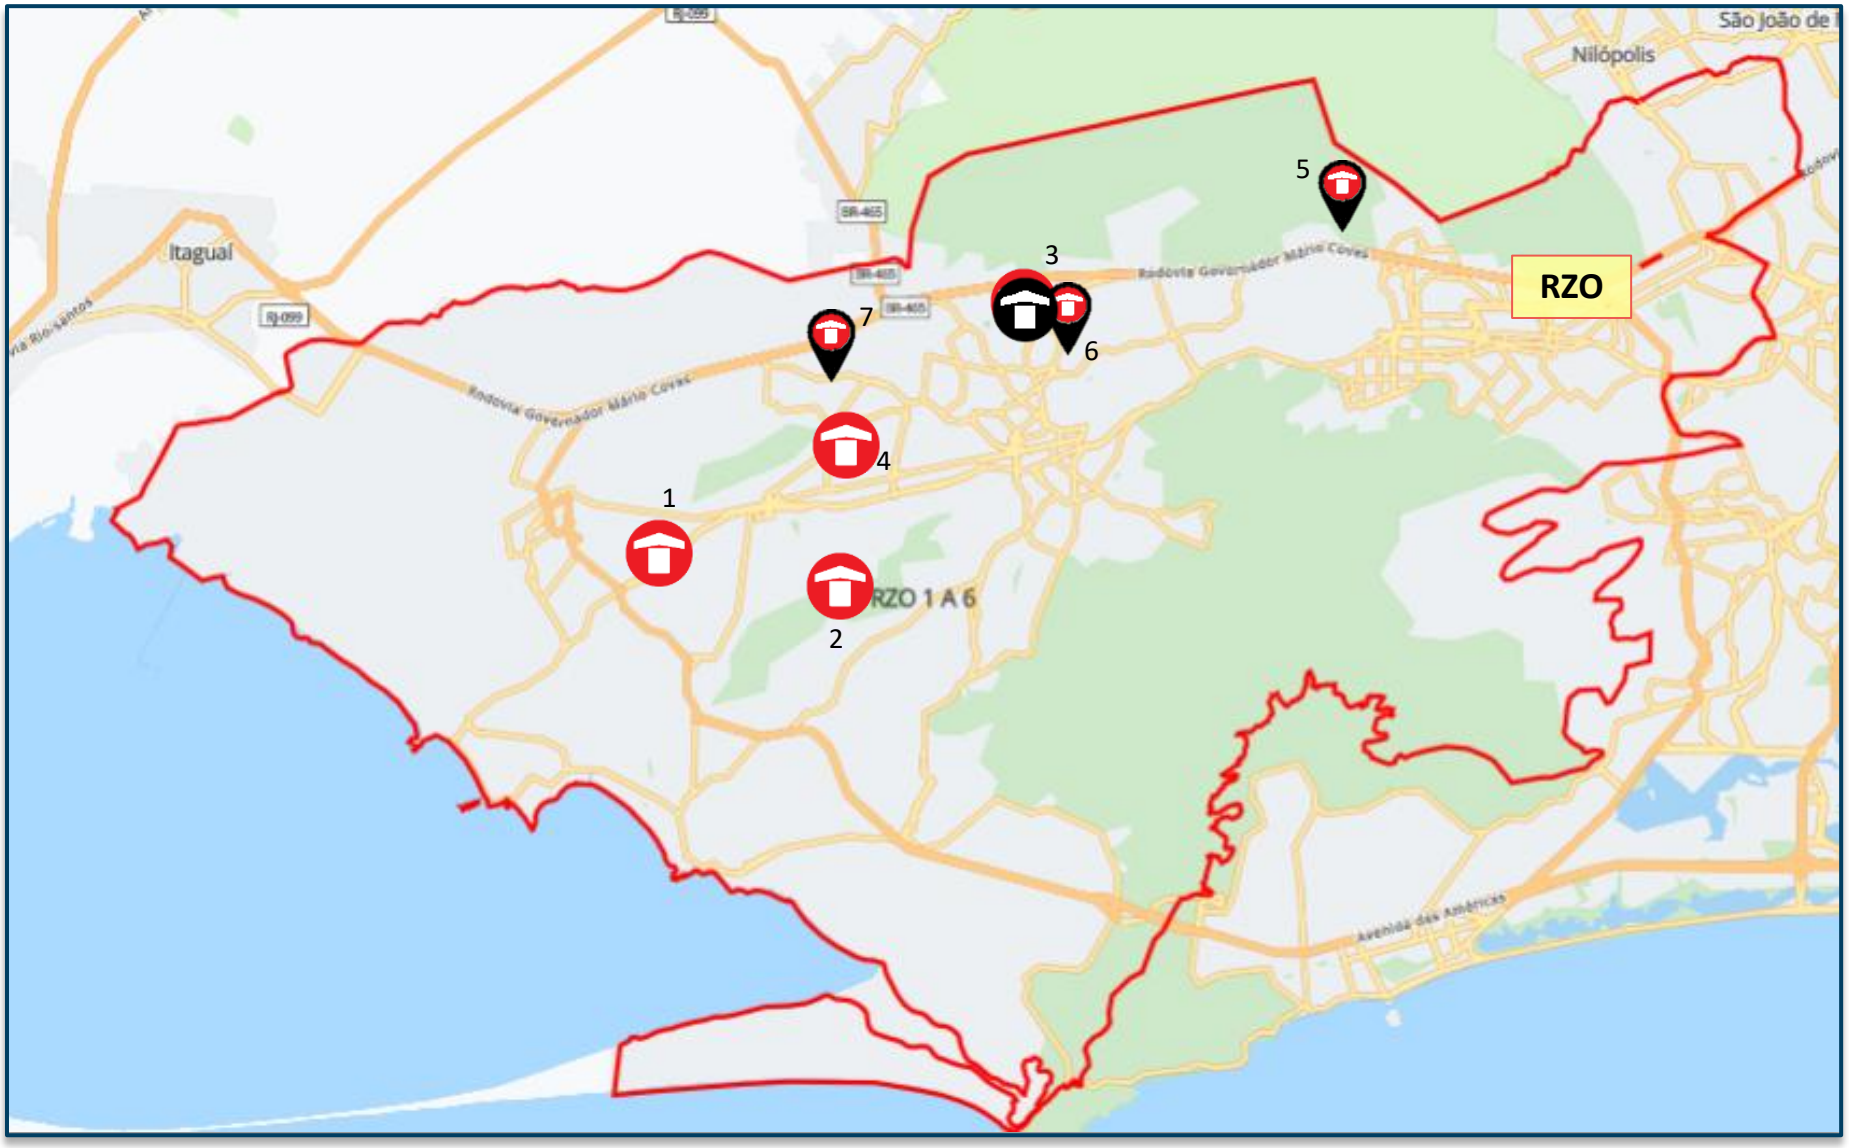

Lançados LandBank Comitê

PRODUTO

Empreendimento Porto Lima
Lançamento

	Informações Gerais	
Terreno	**Área terreno**	23.010,36m²
	Menor poligonal	22.905,483m²
	App/fna	Sim
	Reserva de calçada/ melhoramento viário	Sim
	Área liquida	22.905,483m²
	Zoneamento	ZUPI C AP5
	Ca máximo	3,0
	Ca básico	1,0
	Ca projetado	Cond.01: 1,60 Cond.02: 1,58
	Gabarito máximo	T+4
Geral	**Total uh**	Cond.01: 434 Cond.02: 473 Total: 907
	Total de vagas	Cond.01: 54 (12,44%) Cond.02: 53 (11,21%) Total: 107 (11,80%)

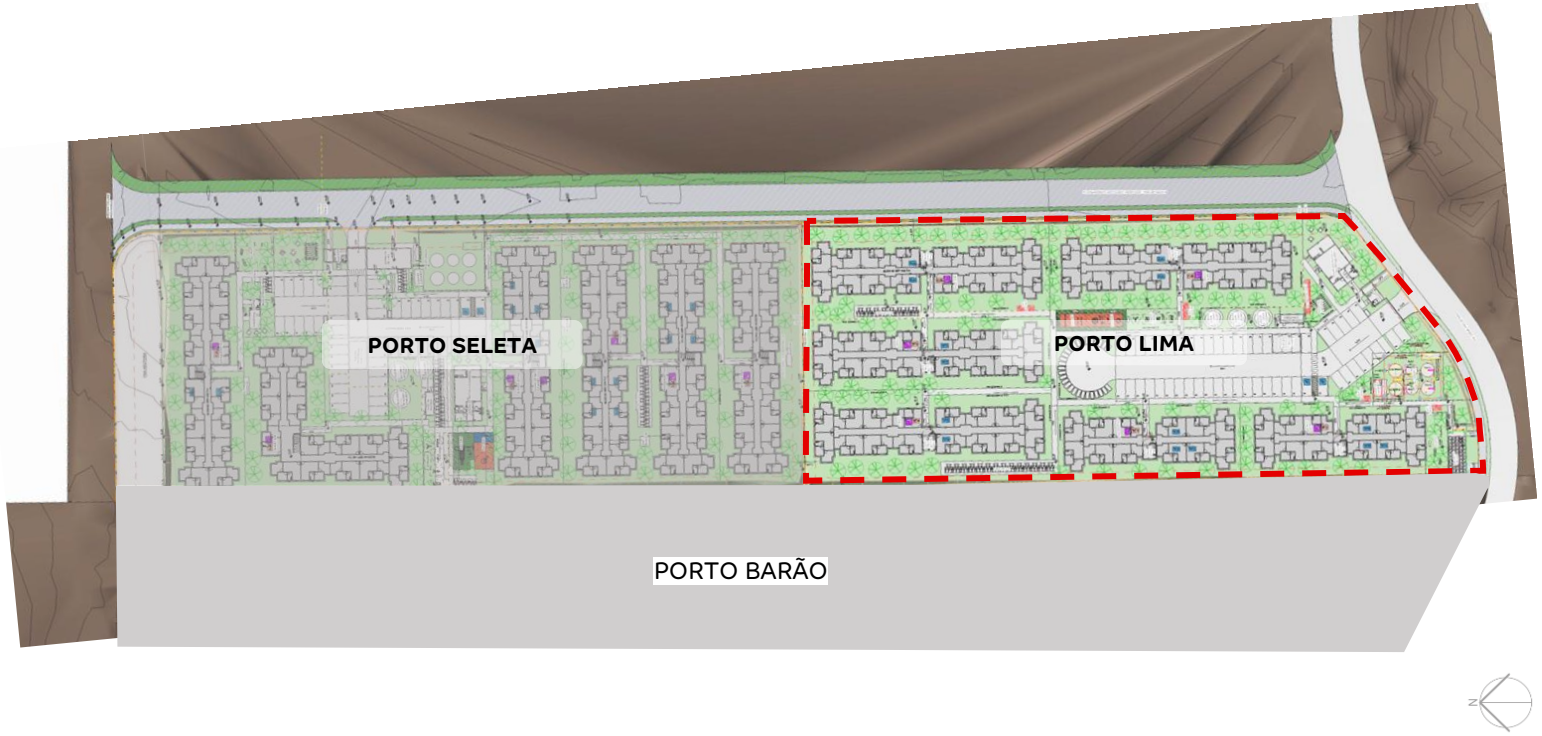

8

PRODUTO

Empreendimento Porto Lima
Lançamento

Informações Gerais – Condomínio 01		
Terreno	Área terreno	10.951,31m²
	Menor poligonal	10.876,565 m²
	App/fna	Sim - 61,139m²
	Reserva de calçada/ melhoramento viário	Sim
	Área liquida	10.815,426
Diretrizes Urbanísticas	Zoneamento	ZUPI C AP5
	Ca máximo	3,0
	Ca básico	1,0
	Ca projetado	1,60
Geral	Total uh	434
	Total de vagas exigido	-
	Total de vagas projetado	54 vagas de carro e 30 vagas de moto
Tipologia	Tipologia	Modular sem elevador
	Gabarito máximo	T+4 (LC 97)
	Gabarito projetado	T+4 (LC 97)
	Lâmina	02 - 12PP | 04 – 16PP
	Área privativa	33,98m² ~ 34,12m²
Condomínio	Unidade pcd	14 U.A
	Unidade lazer | técnica	06
	Torre	06
	Fase	Única
Lazer	Lazer Interno	01- Espaço Teen, 02- Espaço Saúde, 03-Espaço Fitness, 04- Espaço Office, 05- Brinquedoteca, 06- Sport Bar
	Lazer Externo	07- Play Kids, 08- Mini Quadra Descoberta, 09- Play Pet, 10- Salão de Festas com Coworking, 11- Fitness Externo, 12 – Praça de Chagada

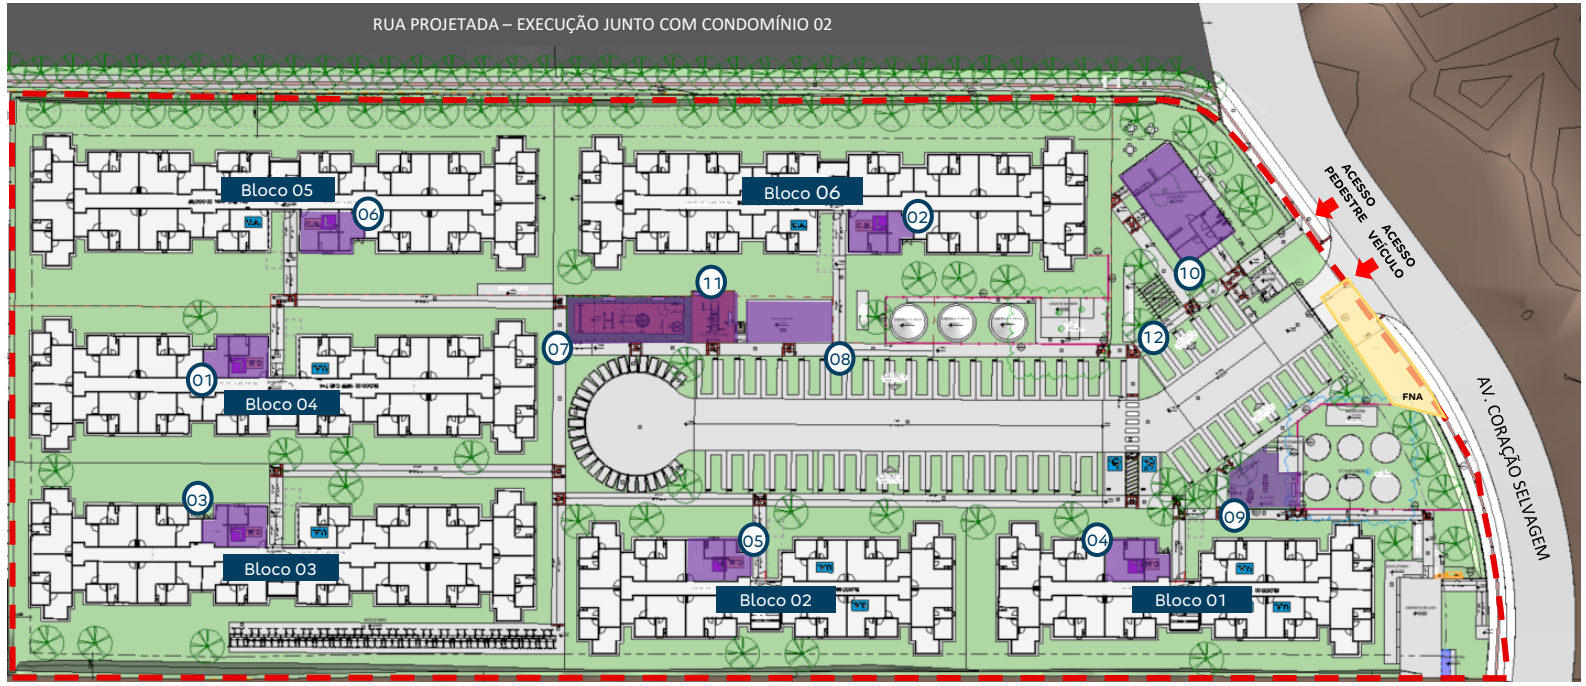

PRODUTO

Empreendimento Porto Lima
Lançamento

	Descrição	Criticidade	Observação
Usabilidade	Acesso Empreendimento		
	Percurso do pedestre até torre		
Diferencial produto	Faixa de renda	2	
	Prime	Não	
	Super condomínio	Não	
	Atributos Infra	-	
	Atributos Torre	Não	
	Edifício Garagem	Não	

PRODUTO

Empreendimento Porto Lima
Lançamento

Fase única: 434UH (Sendo 14 U.A) - 54 vagas de carro (Sendo 02 PCD) – 30 vagas de moto				
Módulo	**Blocos**	**UH**	**Vagas**	**Parecer**
Módulo 01	03 Blocos (T+4)	197 UH (Sendo 08 U.A)	54 vagas de carro (Sendo 02 PCD) e 30 vagas de moto	Dos Lazeres, estão contemplados no módulo 01 o Espaço Fitness, Brinquedoteca, Espaço Office, Play Kids, Fitness Externo, Mini Quadra Descoberta, Play Pet, Salão de Festas com Coworking e Praça de chagada. Demais lazeres que não estão contemplados neste módulo, necessário inclusão dessa informação no RI e material de vendas.
Módulo 02	03 Blocos (T+4)	237 UH (Sendo 06 U.A)	-	Dos Lazeres, estão contemplados no módulo 02 o Espaço Teen, Sport Bar e Espaço Saúde.

RUA PROJETADA

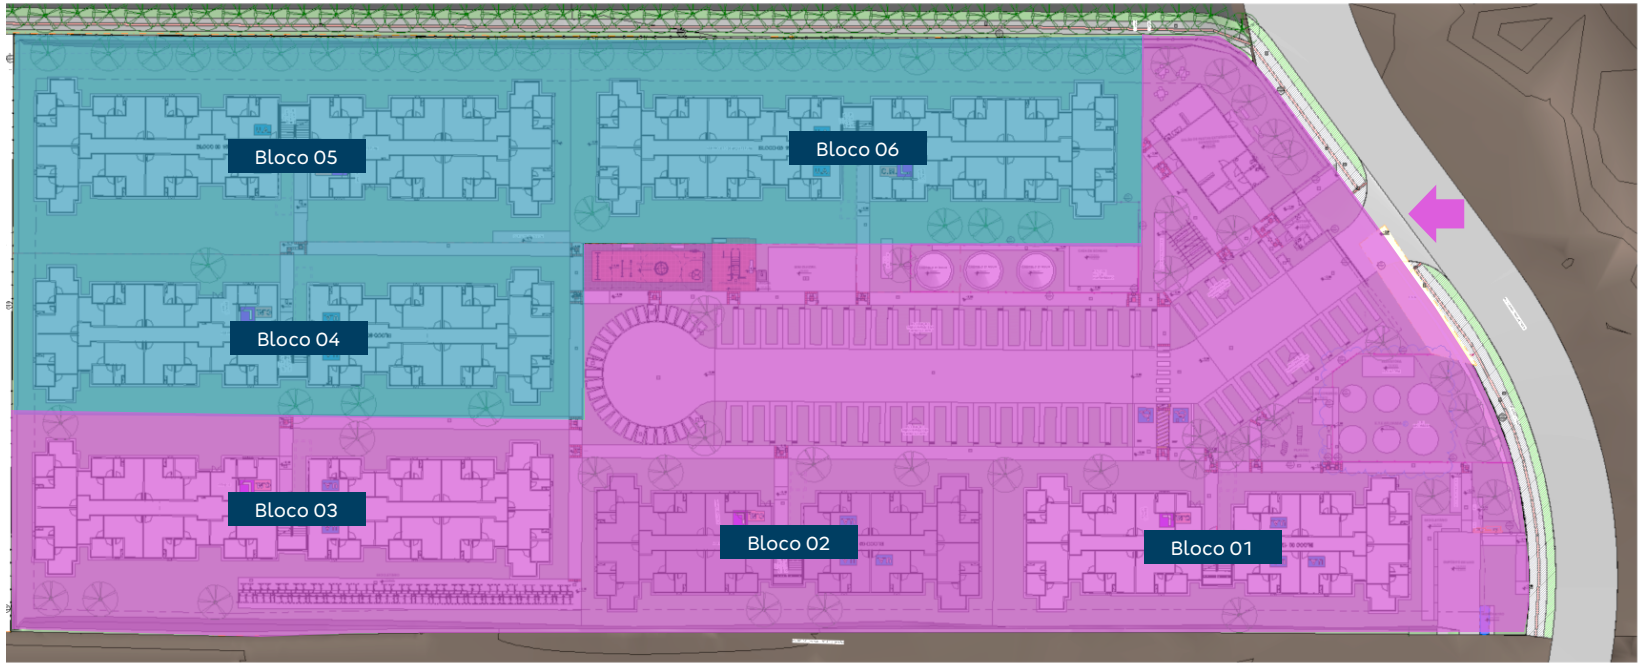

- Pareceres
- Análise da Mancha e Implantação
- Prospecção
- Operações
- Inteligência de Mercado
- Financeiro

Custo de Construção

	PORTO LIMA REV01 COND. 1 - FASE ÚNICA	PORTO LIMA REV00 COND. 1 - FASE ÚNICA	PORTO LIMA REV01 CONSOLIDADO ENTRE COND. FASE ÚNICA	PORTO LIMA REV00 CONSOLIDADO ENTRE COND. FASE ÚNICA	PORTO LIMA CEN04 | REV06.1 CONSOLIDADO	PARQUE HORTÊNSIA LVS
Torres	12	12	12	12	12	5
Unidades Construídas	440	440	440 | 480	440 | 480	280 | 160 | 320 | 160	360
Unidades Vendidas	434	434	434 | 473	434 | 473	276 | 158 | 315 | 158	355
Total Unidades Vendidas			907	907	907	
Condomínios (qta.)	1	1	2	2	2	1
Cidade	Rio de Janeiro	Rio de Janeiro	Rio de Janeiro	Rio de Janeiro	Rio de Janeiro	Rio de Janeiro
Produto / Selo	F2 MODULAR	F2 MODULAR	F2 MODULAR	F2 MODULAR	F2 MODULAR	F2 MODULAR
Tipologia	4 Torre | T+4 | 16PP	4 Torre | T+4 | 16PP	09 Torre | T+4 | 16PP	09 Torre | T+4 | 16PP	09 Torre | T+4 | 16PP	01 Torre | T+4 | 10PP
Tipologia	2 Torre | T+4 | 12PP	2 Torre | T+4 | 12PP	2 Torre | T+4 | 12PP	2 Torre | T+4 | 12PP	2 Torre | T+4 | 12PP	01 Torre | T+4 | 14PP
Tipologia			1 Torre | T+04 | 16PP (L)	1 Torre | T+04 | 16PP (L)	1 Torre | T+04 | 16PP (L)	03 Torre | T+4 | 16PP
Atributos	Quadra | Salão de festas	Quadra | Salão de festas	Quadra | Salão de festas	Quadra | Salão de festas		
Projeto Infra	AP	AP	AP	AP	AP	
Projeto Torre	AP	AP	AP	AP	AP	
Mês Base	março-26	janeiro-26	março-26	janeiro-26	abril-25	setembro-25
Incc	1.237,036	1.225,633	1.237,036	1.225,633	1.178,386	1.210,470
LVS	janeiro-25	novembro-25	janeiro-25	novembro-25	fevereiro-25	janeiro-26
Base de Preço	LPU 100	LPU 99	LPU 100	LPU 99	LPU 89	LPU 94
Takt	2+2	2+2	2+2	2+2	2+2	
Prazo (mês)	12	12	12 | 13	12 | 13	11 | 9 | 12 | 9	11
CUSTO TOTAL I	R$ / UND R$ 94.257	R$ / UND R$ 90.206	R$ / UND R$ 94.690	R$ / UND R$ 90.061	R$ / UND R$ 88.561	R$ / UND R$ 88.688
Indireto	R$ 17.998	R$ 18.882	R$ 18.299	R$ 18.505	R$ 21.077	R$ 18.088
Torre	R$ 45.017	R$ 43.674	R$ 45.352	R$ 43.749	R$ 42.190	R$ 41.270
Infra	R$ 20.345	R$ 18.615	R$ 20.011	R$ 18.327	R$ 16.524	R$ 18.388
Fundação	R$ 7.234	R$ 5.696	R$ 6.923	R$ 5.644	R$ 5.010	R$ 4.164
EEE	R$ 150	R$ 150	R$ 143	R$ 143	R$ 248	R$ 431
ETE	R$ 1.562	R$ 1.368	R$ 1.402	R$ 1.309	R$ 1.134	R$ 1.474
Contenção	R$ 85	R$ 85	R$ 41	R$ 41		R$ 8
Terraplenagem	R$ 1.865	R$ 1.736	R$ 2.519	R$ 2.343	R$ 2.378	R$ 4.866
CUSTO TOTAL II	R$ 4.033	R$ 4.033	R$ 4.033	R$ 4.033	R$ 2.365	R$ 3.104
Urbanização	R$ 1.721	R$ 1.721	R$ 1.721	R$ 1.721	R$ 1.553	R$ 1.538
Drenagem	R$ 591	R$ 591	R$ 591	R$ 591	R$ 521	
Extensão de Rede Elétrica	R$ 364	R$ 364	R$ 364	R$ 364	R$ 34	
Extensão de Rede Hidráulica	R$ 1.357	R$ 1.357	R$ 1.357	R$ 1.357	R$ 256	R$ 1.566
CUSTO TOTAL III						
Incorridos						
CUSTO TOTAL IV						
Aprendizado						
CUSTO TOTAL V		R$ 877		R$ 875	R$ 3.646	
Atualização por INCC		R$ 877		R$ 875	R$ 3.646	
CUSTO TOTAL I+II	R$ 98.290	R$ 94.239	R$ 98.723	R$ 94.094	R$ 90.925	
ATRIBUTOS	R$ 483	R$ 483	R$ 483	R$ 483		
CUSTO TOTAL I AO IV	R$ 98.290	R$ 95.116	R$ 98.723	R$ 94.970	R$ 94.571	R$ 91.793

Custo de Construção

	PORTO LIMA REV01 COND. 1 - FASE ÚNICA	PORTO LIMA REV00 COND. 1 - FASE ÚNICA	
Torres	12	12	
Unidades Construídas	440	440	
Unidades Vendidas	434	434	
Total Unidades Vendidas	0	0	
Condomínios (qta.)	1	1	
Cidade	Rio de Janeiro	Rio de Janeiro	
Produto / Selo	F2 MODULAR	F2 MODULAR	
Tipologia	4 Torre | T+4 | 16PP	4 Torre | T+4 | 16PP	
Tipologia	2 Torre | T+4 | 12PP	2 Torre | T+4 | 12PP	
Atributos	Quadra | Salão de festas	Quadra | Salão de festas	
Projeto Infra	AP	AP	
Projeto Torre	AP	AP	
Mês Base	março-26	janeiro-26	
Incc	1237,036	1225,633	
LVS	janeiro-25	novembro-25	
Indiretos	janeiro-25	novembro-25	
Base de Preço	LPU 100	LPU 99	
Takt	2+2	2+2	
Prazo (mês)	12	12	
CUSTO TOTAL I	R$ / UND R$ 94.257	R$ / UND R$ 90.206	DIF R$ 4.051
Indireto	R$ 17.998	R$ 18.882	-R$ 884
Torre	R$ 45.017	R$ 43.674	R$ 1.343
Infra	R$ 20.345	R$ 18.615	R$ 1.730
Fundação	R$ 7.234	R$ 5.696	R$ 1.538
EEE	R$ 150	R$ 150	R$ 0
ETE	R$ 1.562	R$ 1.368	R$ 195
Contenção	R$ 85	R$ 85	R$ 0
Terrapplenagem	R$ 1.865	R$ 1.736	R$ 130
CUSTO TOTAL II	R$ 4.033	R$ 4.033	R$ 0
Urbanização	R$ 1.721	R$ 1.721	R$ 0
Drenagem	R$ 591	R$ 591	R$ 0
Extensão de Rede Eletrica	R$ 364	R$ 364	R$ 0
Extensão de Rede Hidráulica	R$ 1.357	R$ 1.357	R$ 0
CUSTO TOTAL III	R$ 0	R$ 0	R$ 0
Incorridos	R$ 0	R$ 0	R$ 0
CUSTO TOTAL IV	R$ 0	R$ 0	R$ 0
Aprendizado	R$ 0	R$ 0	R$ 0
CUSTO TOTAL V	R$ 0	R$ 877	-R$ 877
Atualização por INCC	R$ 0	R$ 877	-R$ 877
CUSTO TOTAL	R$ 98.290	R$ 95.116	R$ 3.174

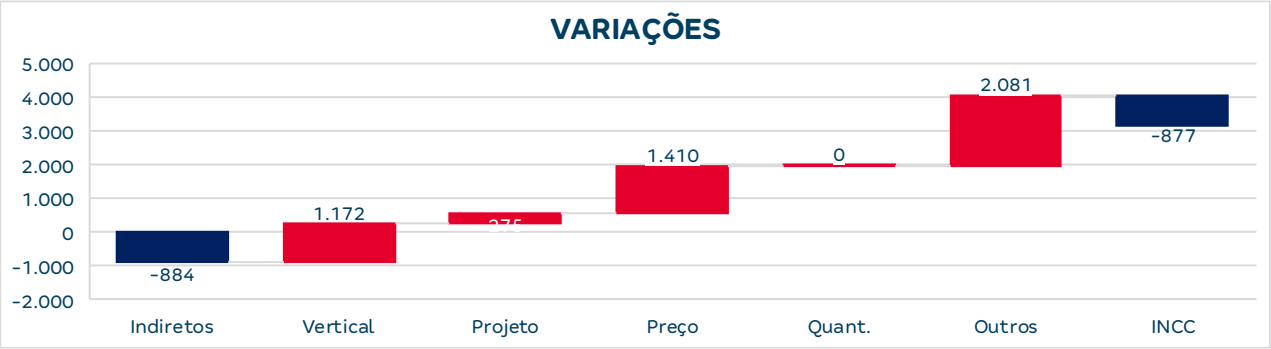

INDIRETOS
-785 | G11 Serviços técnicos
-45 | G13 Pessoal Permanente

VERTICAL
+1.172 | Vertical

PROJETO
+659 | Fundação Torre (troca de solo)
+197 | Reserv. Metalico (Fundação est. Raiz)
-354 | Concreto Torre (FCK25 x FCK20)

PREÇO
+553 | Fundação Torre (troca de solo)
+326 | Fundação Torre (Lajão)
+130 | Terraplenagem
+279 | Reserv. Metalico
+195 | E.T.E. (Cotação)

OUTROS
+723 | Inst. Torre
+1.358 | Inst. Infra

INCC
-877 | Atualização de INCC

Custo de Construção

	PORTO LIMA REV01 CONSOLIDADO ENTRE COND. FASE ÚNICA	PORTO LIMA REV00 CONSOLIDADO ENTRE COND. FASE ÚNICA	
Torres	12	12	
Unidades Construídas	280 | 160 | 320 | 160	280 | 160 | 320 | 160	
Unidades Vendidas	276 | 158 | 315 | 158	276 | 158 | 315 | 158	
Total Unidades Vendidas	907	907	
Condomínios (qta.)	2	2	
Cidade	Rio de Janeiro	Rio de Janeiro	
Produto / Selo	F2 MODULAR	F2 MODULAR	
Tipologia	09 Torre | T+4 | 16PP	09 Torre | T+4 | 16PP	
Tipologia	2 Torre | T+4 | 12PP	2 Torre | T+4 | 12PP	
Tipologia	1 Torre | T+04 | 16PP (L)	1 Torre | T+04 | 16PP (L)	
Atributos	Quadra | Salão de festas	Quadra | Salão de festas	
Projeto Infra	AP	AP	
Projeto Torre	AP	AP	
Mês Base	março-26	janeiro-26	
Incc	1237,036	1225,633	
LVS	janeiro-25	novembro-25	
Indiretos	janeiro-25	novembro-25	
Base de Preço	LPU 100	LPU 99	
Takt	2+2	2+2	
Prazo (mês)	12 | 13	12 | 13	
CUSTO TOTAL I	R$ / UND R$ 94.690	R$ / UND R$ 90.061	DIF R$ 4.629
Indireto	R$ 18.299	R$ 18.505	-R$ 206
Torre	R$ 45.352	R$ 43.749	R$ 1.603
Infra	R$ 20.011	R$ 18.327	R$ 1.684
Fundação	R$ 6.923	R$ 5.644	R$ 1.279
EEE	R$ 143	R$ 143	R$ 0
ETE	R$ 1.402	R$ 1.309	R$ 93
Contenção	R$ 41	R$ 41	R$ 0
Terrapplenagem	R$ 2.519	R$ 2.343	R$ 175
CUSTO TOTAL II	R$ 4.033	R$ 4.033	R$ 0
Urbanização	R$ 1.721	R$ 1.721	R$ 0
Drenagem	R$ 591	R$ 591	R$ 0
Extensão de Rede Eletrica	R$ 364	R$ 364	R$ 0
Extensão de Rede Hidráulica	R$ 1.357	R$ 1.357	R$ 0
CUSTO TOTAL III	R$ 0	R$ 0	R$ 0
Incorridos	R$ 0	R$ 0	R$ 0
CUSTO TOTAL IV	R$ 0	R$ 0	R$ 0
Aprendizado	R$ 0	R$ 0	R$ 0
CUSTO TOTAL V	R$ 0	R$ 875	-R$ 875
Atualização por INCC	R$ 0	R$ 875	-R$ 875
CUSTO TOTAL	R$ 98.723	R$ 94.970	R$ 3.754

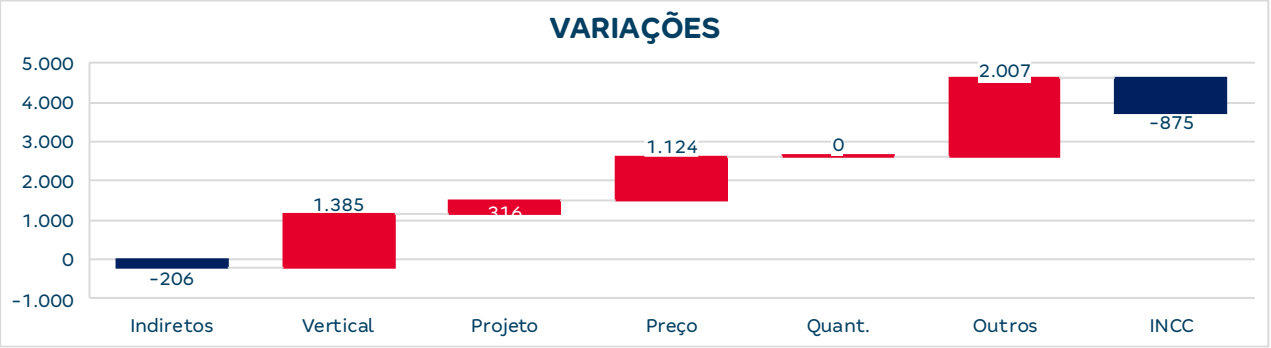

INDIRETOS
-376 | G11 Serviços técnicos
+219 | G13 Pessoal Permanente

VERTICAL
+1.338 |Vertical

PROJETO
+315 | Fundação (troca de solo)
+94 | Reserv. Metalico (Fundação est. Raiz)
-169 | Concreto Torre (FCK25 x FCK20)

PREÇO
+447 | Fundação Torre (troca de solo)
+532 | Fundação Torre (Lajão)
+175 | Terraplenagem
+267 | Reserv. Metalico
+66 | E.T.E. (Cotação)

OUTROS
+797 | Inst. Torre
+1.359 | Inst. Infra

INCC
-875 | Atualização de INCC

Operações

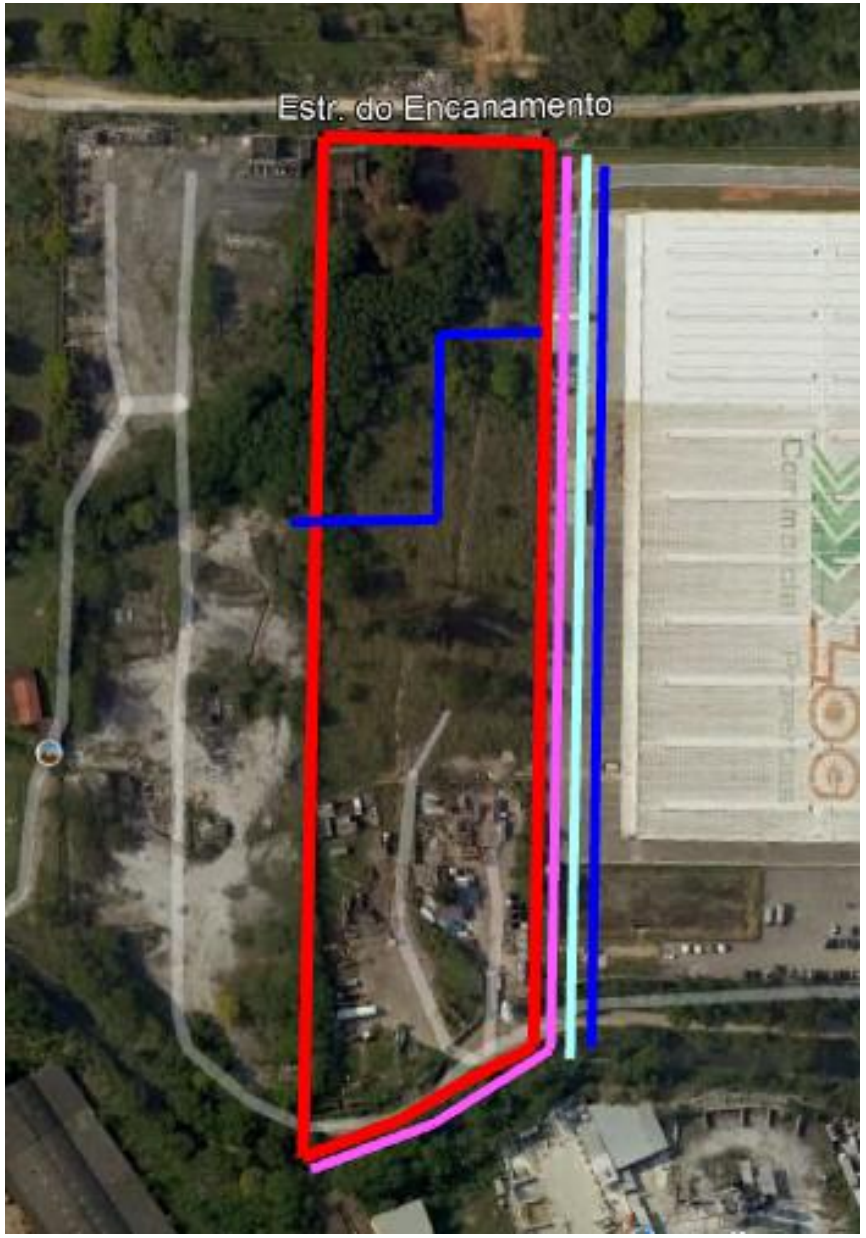

SISTEMA DE ABASTECIMENTO DE ÁGUA
Considerado extensão de 350m no cond. 02

SISTEMA DE ESGOTAMENTO SANITÁRIO
Viabilidade existente. Considerado ETE. Considerado custo de extensão de rede de esgoto no cond. 02.

SISTEMA DE DRENAGEM
Considerado extensão de 97 no cond. 02 FNA.

SISTEMA DE ABASTECIMENTO DE GÁS
Abastecimento por GLP.

SISTEMA DE ABASTECIMENTO ELÉTRICO
Existe viabilidade técnica. Considerado extensão de posteamento na rua nova a ser projetada.

TERRENO

URBANIZAÇÃO
Considerado rua de acesso ao Condomínio 2 (pavimentação, calçada e grama) e calçada na testada do Condomínio 1.

Operações

Matriz Risco Concessionária	
Água	Nível 1
Esgoto	Nível 1
Drenagem	Nível 2
Elétrica	Nível 3
Gás	NA
Urbanização	Nível 3

LEGENDA		
Nível	Tipo	Status
1	Com Diretriz	Conclusiva
2		Conclusiva com projeto aprovado
3		Conclusiva sem projeto aprovado
4		Não Conclusiva
5	Sem Diretriz	-
NA	-	Não aplicável

Água:
- Viabilidade Cond. 01 emitida em 23/09/2025, com validade de 24 meses. Viabilidade para 434u.h.
- Viabilidade Cond. 02 emitida em 23/09/2025, com validade de 24 meses. Viabilidade para 473u.h.

Esgoto:
- Viabilidade Cond. 01 emitida em 02/12/2025, com validade de 12 meses. Viabilidade para 434 u.h.
- Viabilidade Cond. 02 emitida em 02/12/2025, com validade de 12 meses. Viabilidade para 473u.h.

Drenagem:
- DPEP existente. Considerado extensão projeto aprovado.

Elétrica:
- Viabilidade Cond. 01e 2 emitida em 27/06/2025, para 442 u.h com validade de 60 dias.

Gás:
- Empreendimento com GLP.

Urbanização:
- Considerado rua de acesso ao Condomínio 2 (pavimentação, calçada e grama) e calçada na testada do Condomínio 1. Enviado a PAA existente para esse terreno.

Fundação:
- Sendo Realizada 3ª campanha de sondagem..
- Considerada Radier e Estaca Raiz, com diâmetro de 31 e profundidade de 12 m.

Logística

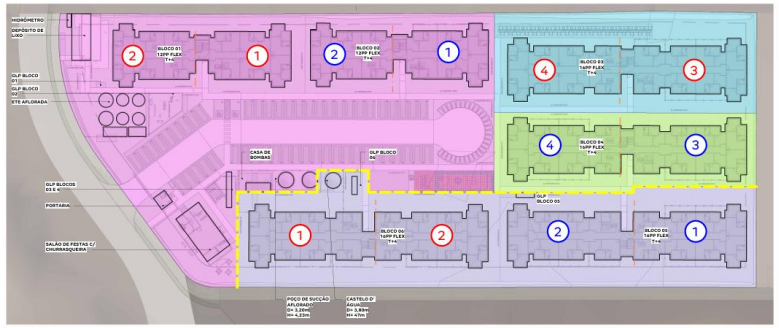

MODULAÇÃO E TOMBAMENTO
1 : 500

VIVÊNCIA - CONTAINERS								
DESCRIÇÃO	QUANTIDADE	TAMANHO MÓDULOS	MOBILIZAÇÃO	DESMOBILIZAÇÃO	PRÉ FORMA	ESTRUTURA	ACAB.	FASE
CONTAINER ALMOXARIFADO (LOG)	1 MÓDULO DE CONTAINER	2,41 X 6,10 m	1 MOBILIZAÇÃO	1 DESMOBILIZAÇÃO	-	TODO PERÍODO	TODO PERÍODO	FASE 01 E 02
CONTAINER PORTARIA (LOG)	CONSIDERAR 1 MÓDULO COM SANITÁRIO E CATRACA	2,41 X 4,90 m	1 MOBILIZAÇÃO	1 DESMOBILIZAÇÃO	TODO PERÍODO	** AJUSTAR	** AJUSTAR	FASE 01 E 02
CONTAINER PROVISÓRIO (LOG)	CONSIDERAR 8 MÓDULOS DE CONTAINER	2,41 X 6,10 m	1 MOBILIZAÇÃO	1 DESMOBILIZAÇÃO	TODO PERÍODO	-	-	FASE 01 E 02
CONTAINER VESTIÁRIO ACABAMENTO (LOG)	CONSIDERAR 2 MÓDULOS DE CONTAINER	2,41 X 6,10 m	1 MOBILIZAÇÃO	1 DESMOBILIZAÇÃO	-	-	TODO PERÍODO	FASE 01 E 02
CONTAINER VESTIÁRIO ESTRUTURA (LOG)	CONSIDERAR 2 MÓDULOS DE CONTAINER (EQUIPE VERTICAL)	2,41 X 6,10 m	1 MOBILIZAÇÃO	1 DESMOBILIZAÇÃO	-	TODO PERÍODO	-	FASE 01 E 02
CONTAINER VIVÊNCIA PADRÃO (LOG)	CONSIDERAR 14 MÓDULOS COM 2 ESCADAS (7 MÓDULOS NO PAV. T E 7 MÓDULOS NO PAV SUPERIOR)	2,41 X 6,10 m	1 MOBILIZAÇÃO	1 DESMOBILIZAÇÃO	-	TODO PERÍODO	TODO PERÍODO	FASE 01 E 02

TENDAS_PERÍODOS							
DESCRIÇÃO	QUANTIDADE	LARGURA	COMPRIMENTO	PRÉ FORMA	ESTRUTURA	ACABAMENTO	FASE
GAIOLA DE DESMOLDANTE (LOG)	1	4,00	6,00	-	TODO PERÍODO	-	FASE 01 E 02
GAIOLA DE INFLAMÁVEIS (LOG)	1	3,00	4,00	-	TODO PERÍODO	TODO PERÍODO	FASE 01 E 02
TENDA ACABAMENTO (LOG)	1	9,98	7,07	-	TODO PERÍODO	TODO PERÍODO	FASE 01 E 02
TENDA ARMADOR (LOG)	2	4,00	7,00	TODO PERÍODO	TODO PERÍODO	-	FASE 01 E 02
TENDA BANHEIRO QUÍMICO E BEBEDOURO (LOG)	1	3,00	3,00	-	TODO PERÍODO	TODO PERÍODO	FASE 01 E 02
TENDA CENTRAL DE KITS (LOG)	1	10,00	10,00	-	TODO PERÍODO	TODO PERÍODO	FASE 01 E 02
TENDA CENTRAL DE PORTAS (LOG)	1	10,00	10,00	-	TODO PERÍODO	TODO PERÍODO	FASE 01 E 02
TENDA LAZER (LOG)	1	4,26	8,37	-	TODO PERÍODO	TODO PERÍODO	FASE 01 E 02
TENDA MOLDADOR (LOG)	1	3,00	4,00	TODO PERÍODO	TODO PERÍODO	-	FASE 01 E 02

EQUIPAMENTOS E MAQUINÁRIOS							
EQUIPAMENTO	QUANTIDADE	MOBILIZAÇÃO	DESMOBILIZAÇÃO	PRÉ FORMA	ESTRUTURA	ACABAMENTO	FASE
BETONEIRA (LOG)	VARIÁVEL	-	-	TODO PERÍODO	TODO PERÍODO	-	FASE 01 E 02
BOMBA LANÇA (LOG)	VARIÁVEL	-	-	TODO PERÍODO	TODO PERÍODO	-	FASE 01 E 02
CAMINHÃO MUNCK (LOG)	1 EQUIPAMENTO PARA CADA FASE	1 MOBILIZAÇÃO	1 DESMOBILIZAÇÃO	-	CONSIDERAR MEIO PERÍODO DE ESTRUTURA	-	FASE 01 E 02
GUINDASTE (LOG)	1 EQUIPAMENTO PARA IÇAMENTO DOS CASTELOS	1 MOBILIZAÇÃO	1 DESMOBILIZAÇÃO	-	-	-	FASE 01 E 02
PERFURATRIZ (LOG)	1 EQUIPAMENTO PARA CADA FASE	1 MOBILIZAÇÃO	1 DESMOBILIZAÇÃO	CONSIDERAR PERÍODO DE ESTACA CONFORME PROJETO.	-	-	FASE 01 E 02
SKYTRAK (LOG)	1 EQUIPAMENTO PARA CADA FASE	1 MOBILIZAÇÃO	1 DESMOBILIZAÇÃO	-	TODO PERÍODO	CONSIDERAR 15 DIAS DO PERÍODO DE ACABAMENTO	FASE 01 E 02

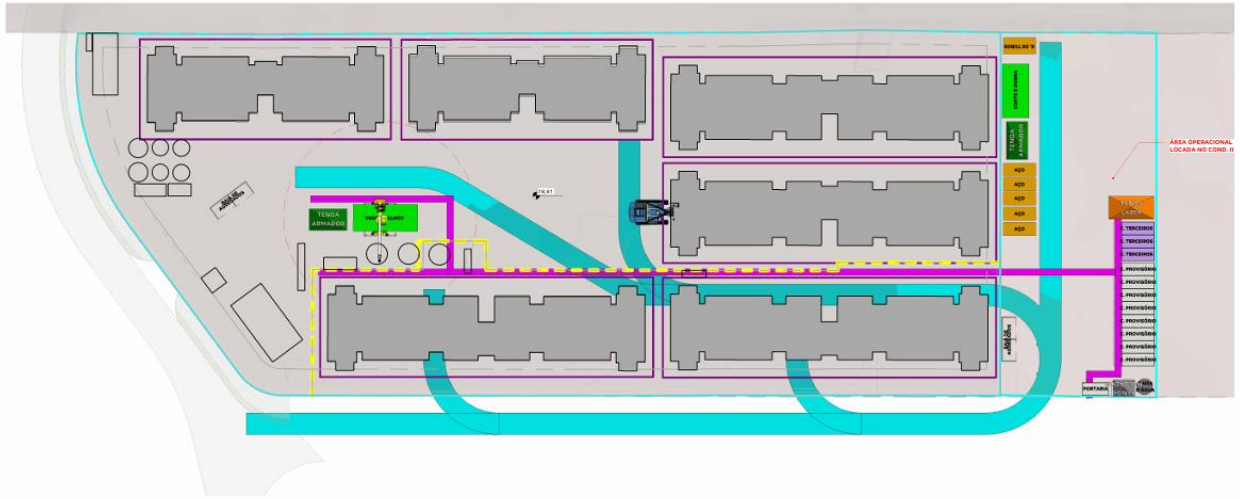

PRÉ FORMA
1 : 500

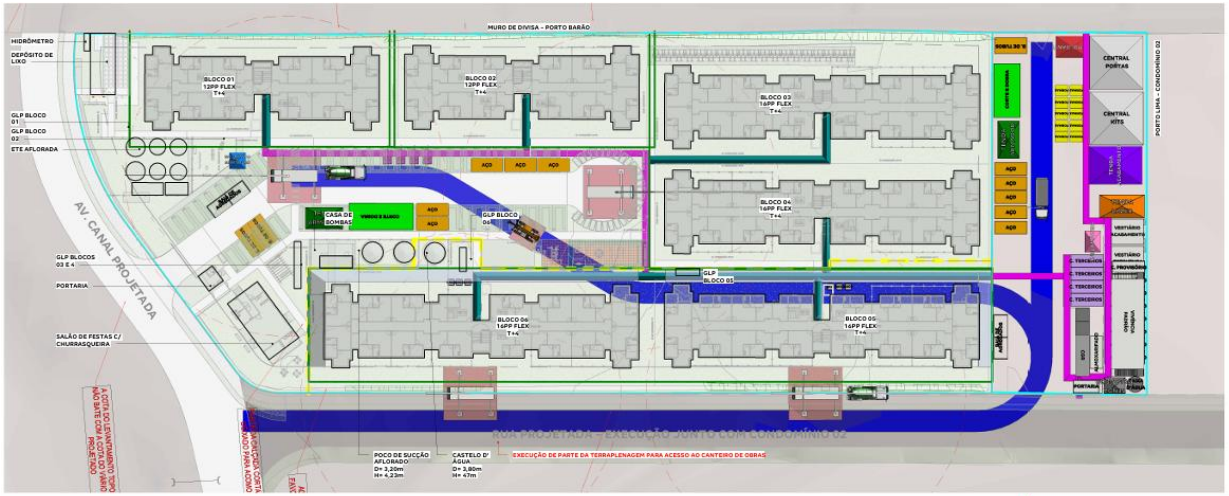

ESTRUTURA E ACABAMENTO
1 : 500

Logística

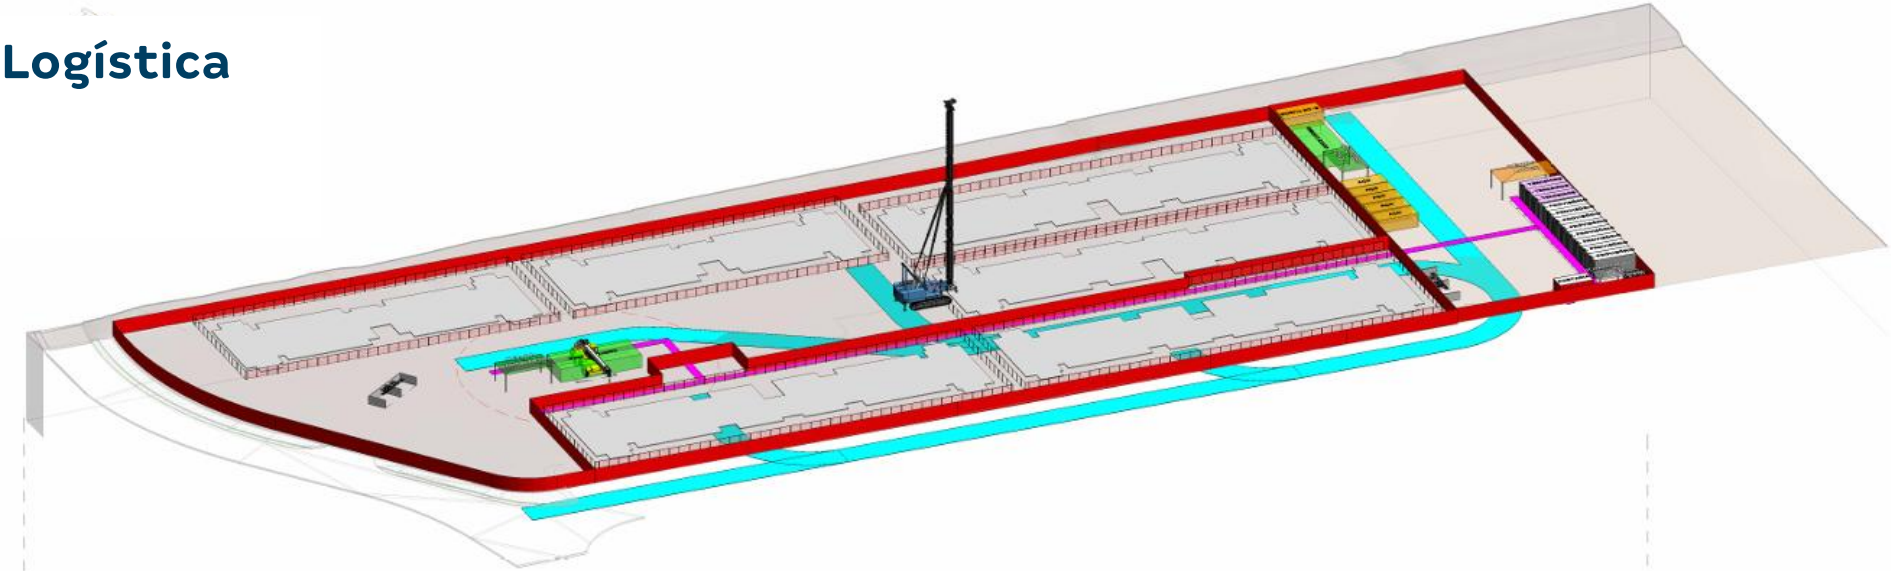

VISTA 3D - PRÉ FORMA

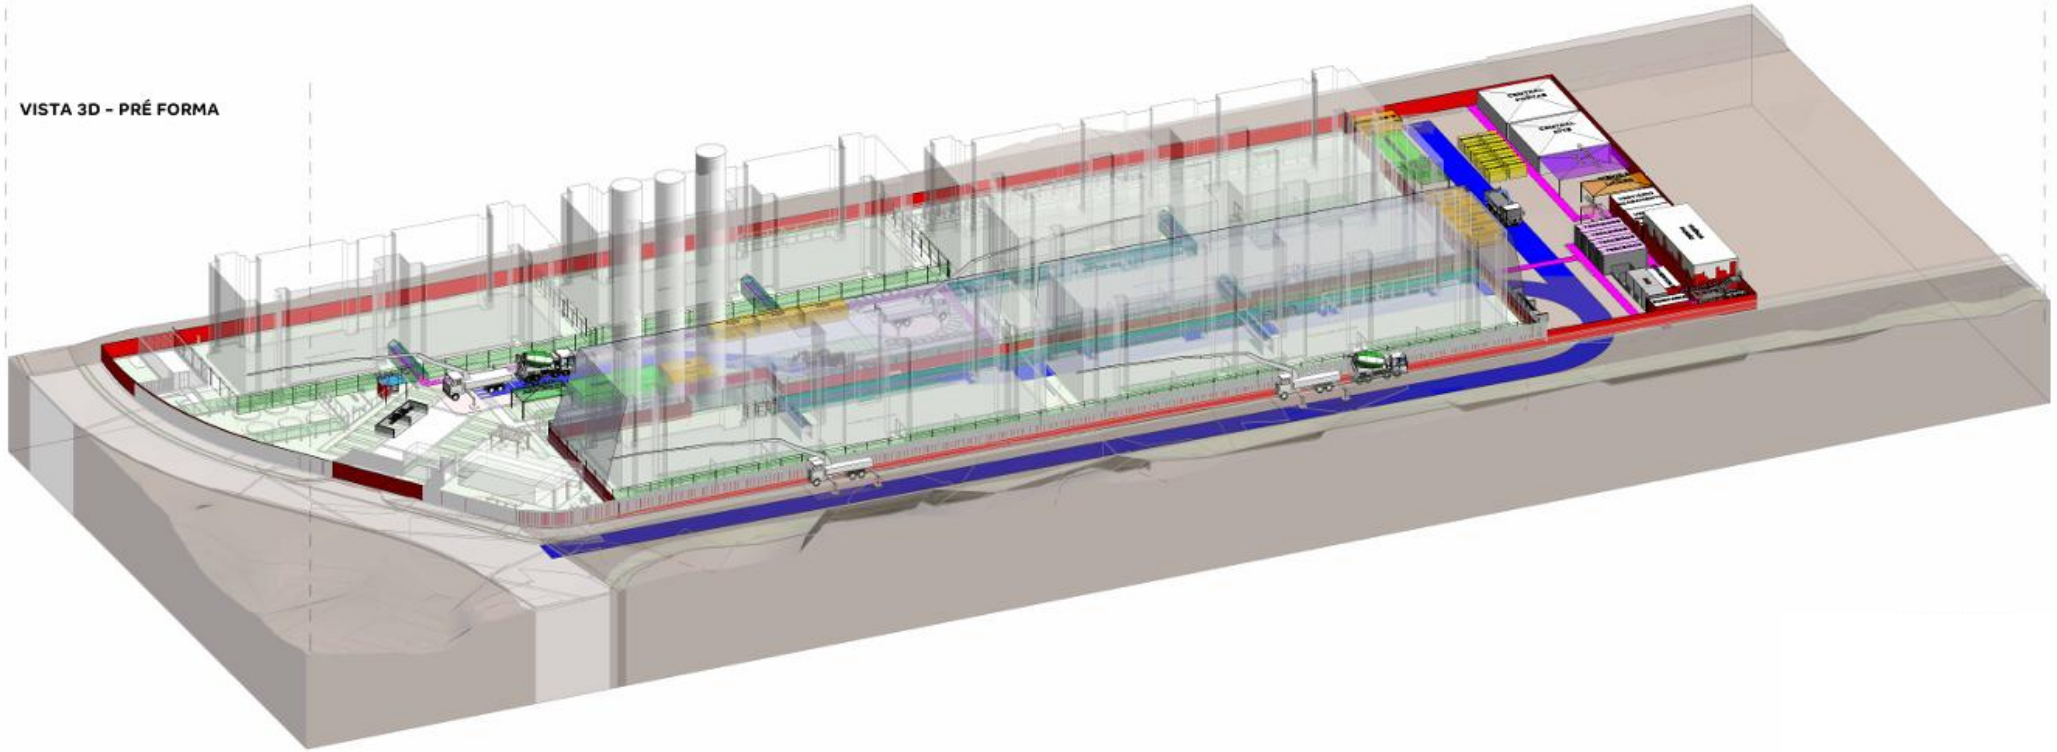

VISTA 3D - ESTRUTURA E ACABAMENTO

Logística

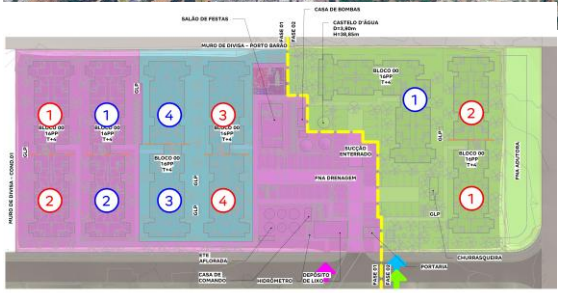

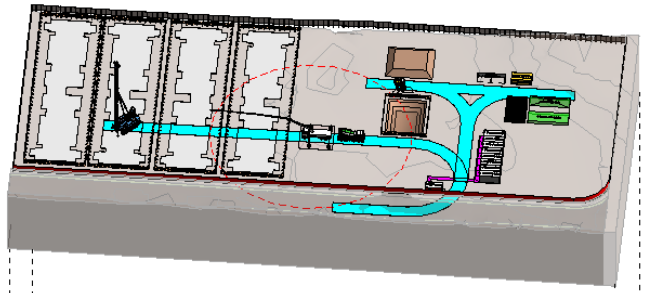

VISTA 3D - PRE FORMA-F1

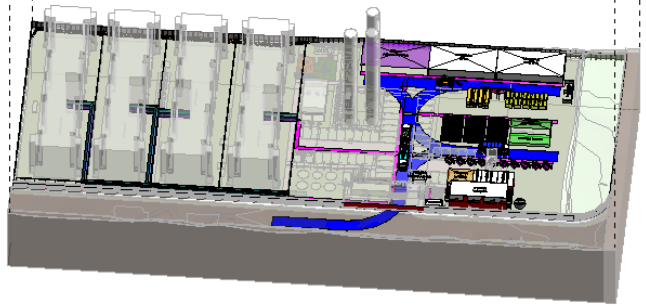

VISTA 3D - ESTRUTURA E ACABAMENTO-F1

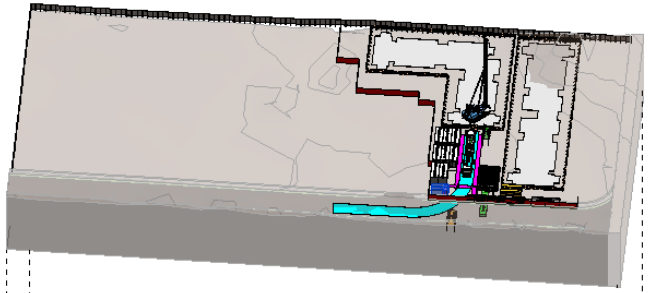

VISTA 3D - PRE FORMA-F2

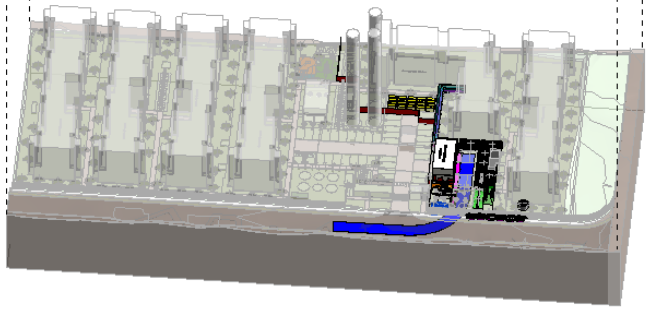

VISTA 3D - ESTRUTURA E ACABAMENTO-F2

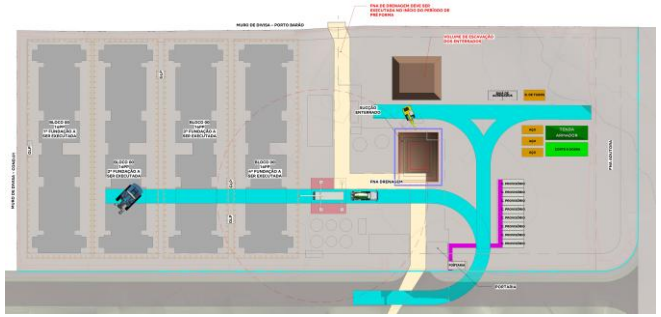

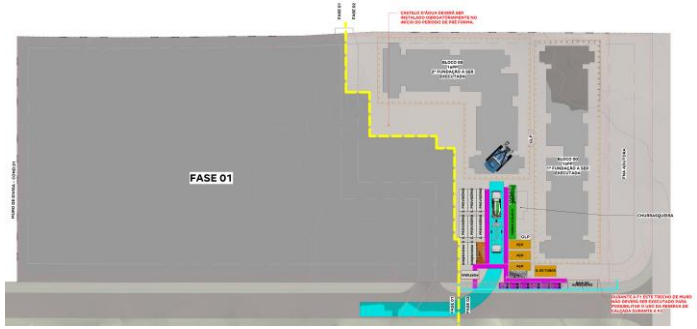

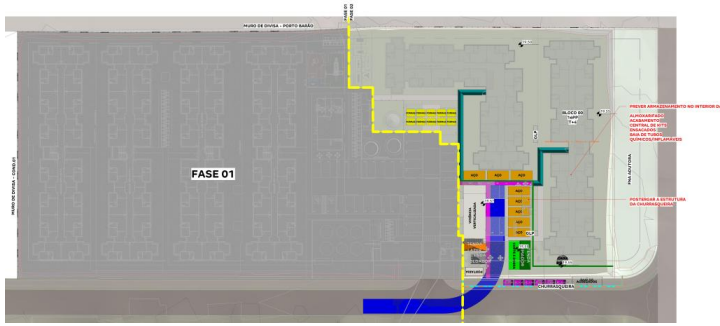

VIVENCIA - CONTAINERS									
DESCRIÇÃO	QUANTIDADE	TAMANHO MÓDULOS	MOBILIZAÇÃO	DESMOBILIZAÇÃO	PRÉ FORMA	ESTRUTURA	ACAB.	FASE	CÓDIGO ORÇAMENTO
CONTAINER ALMOXARIFADO (LOG)	1 MÓDULO DE CONTAINER	2,41 X 6,10 m	1 MOBILIZAÇÃO	1 DESMOBILIZAÇÃO	-	TODO PERÍODO	TODO PERÍODO	F1	
CONTAINER PORTARIA (LOG)	CONSIDERAR 1 MÓDULO COM SANITÁRIO E CATRACA	2,41 X 4,90 m	1 MOBILIZAÇÃO	1 DESMOBILIZAÇÃO	TODO PERÍODO	TODO PERÍODO	TODO PERÍODO	F1	
CONTAINER PORTARIA (LOG)	CONSIDERAR 1 MÓDULO COM SANITÁRIO E CATRACA	2,41 X 4,90 m	1 MOBILIZAÇÃO	1 DESMOBILIZAÇÃO	TODO PERÍODO	TODO PERÍODO	TODO PERÍODO	F2	
CONTAINER PROVISÓRIO (LOG)	CONSIDERAR 8 MÓDULOS DE CONTAINER	2,41 X 6,10 m	1 MOBILIZAÇÃO	1 DESMOBILIZAÇÃO	TODO PERÍODO	-	-	F1	
CONTAINER PROVISÓRIO (LOG)	CONSIDERAR 8 MÓDULOS DE CONTAINER	2,41 X 6,10 m	1 MOBILIZAÇÃO	1 DESMOBILIZAÇÃO	TODO PERÍODO	-	-	F2	
CONTAINER VESTIÁRIO ACABAMENTO (LOG)	CONSIDERAR 2 MÓDULOS DE CONTAINER	2,41 X 6,10 m	1 MOBILIZAÇÃO	1 DESMOBILIZAÇÃO	-	-	TODO PERÍODO	F1	
CONTAINER VESTIÁRIO ESTRUTURA (LOG)	CONSIDERAR 2 MÓDULOS DE CONTAINER (EQUIPE VERTICAL)	2,41 X 6,10 m	1 MOBILIZAÇÃO	1 DESMOBILIZAÇÃO	-	TODO PERÍODO	-	F1	
CONTAINER VIVÊNCIA PADRÃO (LOG)	CONSIDERAR 14 MÓDULOS COM 2 ESCADAS (7 MÓDULOS NO PAV. T E 7 MÓDULOS NO PAV SUPERIOR)	2,41 X 6,10 m	1 MOBILIZAÇÃO	1 DESMOBILIZAÇÃO	-	TODO PERÍODO	TODO PERÍODO	F1	
CONTAINER VIVÊNCIA VERTICALIZADA (LOG)	CONSIDERAR 17 MÓDULOS DE CONTAINERS E 1 ESCADA PARA ACESSO (SENDO 6 NO PAV.T.., 6 NO PAV 1 E 5 NO ULTIMO PAV.)	2,41 X 6,10 m	1 MOBILIZAÇÃO	1 DESMOBILIZAÇÃO	-	TODO PERÍODO	TODO PERÍODO	F2	

TENDAS_PERIODOS								
DESCRIÇÃO	QUANTIDADE	LARGURA	COMPRIMENTO	PRÉ FORMA	ESTRUTURA	ACABAMENTO	FASE	CÓDIGO ORÇAMENTO
GAIOLA DE DESMOLDANTE (LOG)	1	2,00	2,00	-	TODO PERÍODO	-	F1/F2	
GAIOLA DE INFLAMÁVEIS (LOG)	1	2,00	2,00	-	TODO PERÍODO	TODO PERÍODO	F1/F2	
TENDA ACABAMENTO (LOG)	1	10,00	20,00	-	TODO PERÍODO	TODO PERÍODO	F1	
TENDA ARMADOR (LOG)	4	<varia>	<varia>	TODO PERÍODO	TODO PERÍODO	-	F1/F2	
TENDA CENTRAL DE KITS (LOG)	1	10,00	20,00	-	TODO PERÍODO	TODO PERÍODO	F1	
TENDA CENTRAL DE PORTÃS (LOG)	1	10,00	20,00	-	TODO PERÍODO	TODO PERÍODO	F1	
TENDA LAZER (LOG)	3	<varia>	<varia>	-	TODO PERÍODO	TODO PERÍODO	F1/F2	
TENDA MOLDADOR (LOG)	3	<varia>	<varia>	TODO PERÍODO	TODO PERÍODO	-	F1/F2	

LOG_EQUIPAMENTOS E MAQUINÁRIOS								
EQUIPAMENTO	QUANTIDADE	MOBILIZAÇÃO	DESMOBILIZAÇÃO	PRÉ FORMA	ESTRUTURA	ACABAMENTO	FASE	CÓDIGO ORÇAMENTO
BETONEIRA (LOG)	VARIAVEL	-	-	TODO PERÍODO	TODO PERÍODO	-	F1/F2	
BOMBA ESTACIONÁRIA PADRÃO (LOG)_R01	1 EQUIPAMENTO	-	-	-	TODO PERÍODO	-	F1/F2	
BOMBA LANÇA (LOG)	VARIAVEL	-	-	TODO PERÍODO	TODO PERÍODO	-	F1	
ESCAVADEIRA (LOG)							F1/F2	
PERFURATRIZ (LOG)	1 EQUIPAMENTO	1 MOBILIZAÇÃO	1 DESMOBILIZAÇÃO	CONSIDERAR PERÍODO DE ESTACA CONFORME PROJETO.	-	-	F1/F2	
SKYTRAK (LOG)	1 EQUIPAMENTO	1 MOBILIZAÇÃO	1 DESMOBILIZAÇÃO	-	TODO PERÍODO	CONSIDERAR 15 DIAS DO PERÍODO DE ACABAMENTO	F1/F2	

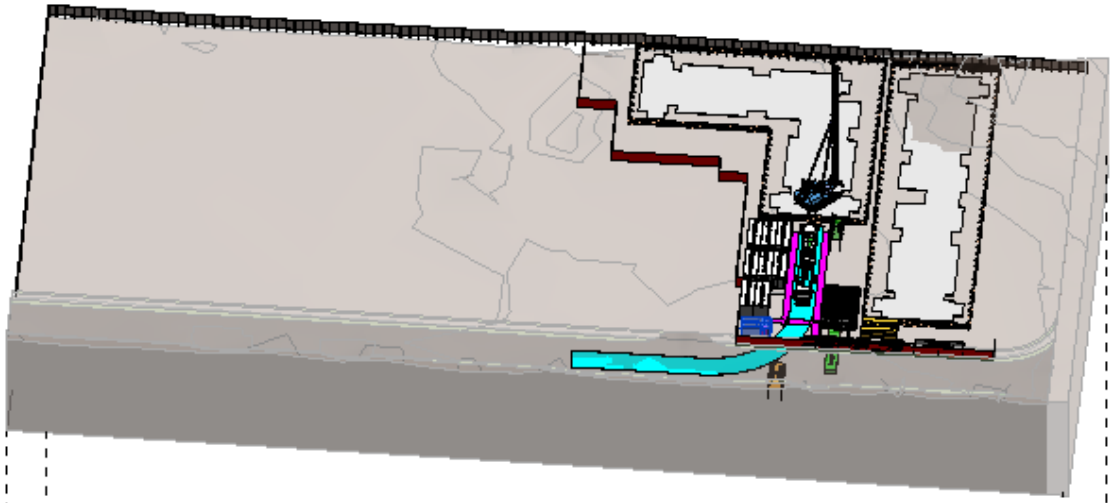

VISTA 3D - PRE FORMA-F2

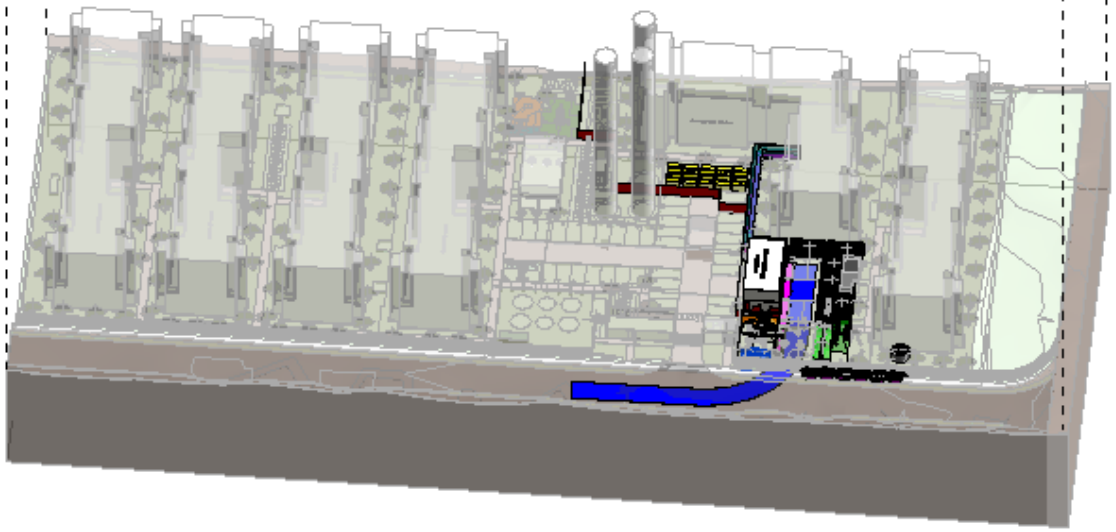

VISTA 3D - ESTRUTURA E ACABAMENTO-F2

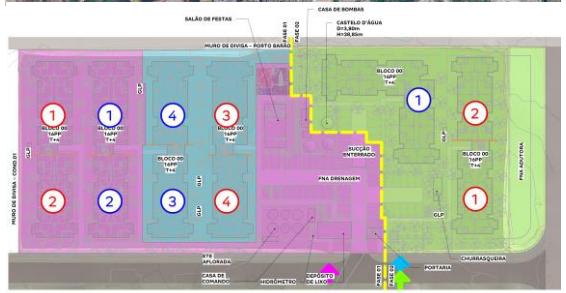

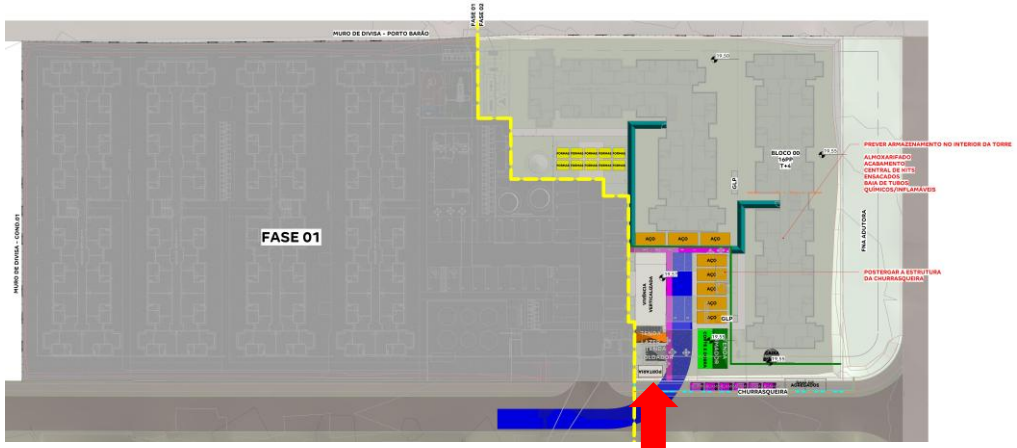

OBS.: 01

➢ OBS. 01	DEVIDO AO ESPAÇO OPERACIONAL LIMITADO, PREVER CUSTOS COM VIVÊNCIA VERTICALIZADA NA FASE 02.
➢ OBS. 02	FNA DE DRENAGEM DEVERÁ SER EXECUTADA NO INÍCIO DO PERÍODO DE PRÉ FORMA.

PCP 174

Empreendimento	Lançto.	Unidades	# jogos	Equipes de forma	Início Obra	Início Forma 1	Início Forma 2	Início Forma 3	Término Forma 1	Término Forma 2	Término Forma 3	Previsão AGI
Aurora Iguaçu	fev/26	730	2	C	16/07/26	13/12/26	14/12/26		01/08/27	02/08/27		jan/28
Porto Lima I	mar/26	434	3	A	03/11/26	27/03/27	02/04/27	17/04/27	27/06/27	03/07/27	18/07/27	dez/27
Elevato Ramos	mar/26	494	3	A	30/12/26	28/06/27	04/07/27	19/07/27	10/10/27	16/10/27	30/10/27	jun/28
Silva Vale I	jun/26	494	2	C	05/03/27	02/08/27	03/08/27		06/01/28	07/01/28		set/28
Mirante Boa Vista - F1+F2	jul/26	442	3	A	23/05/27	11/10/27	17/10/27	31/10/27	13/01/28	19/01/28	01/02/28	out/28
Luisa Vale	ago/26	414	2	C	19/08/27	07/01/28	08/01/28		17/05/28	18/05/28		jan/29
Elevato Carolina Machado	set/26	480	3	A	23/08/27	14/01/28	20/01/28	02/02/28	24/04/28	30/04/28	13/05/28	jan/29
Elevato Nova Iguaçu	out/26	606	3	A	27/11/27	25/04/28	01/05/28	14/05/28	31/08/28	06/09/28	19/09/28	mai/29

Pareceres

Análise da Mancha e Implantação

Prospecção

Operações

Inteligência de Mercado

Financeiro

Demanda e Distribuição da Mancha

Potencial de Demanda			Lançados		Lanç + Landbank	
Mancha	CÓD.	Shr.	ANO	MÊS	ANO	MÊS
Rio de Janeiro Oeste 1/6	RZO 1/6	40%	1.664	139	1.997	166

Faixas MCMV	Empreendimento	Renda	Lançamento	mar/26	abr/26	mai/26	jun/26	jul/26	ago/26	set/26	out/26	nov/26	dez/26	jan/27	fev/27	mar/27	abr/27	mai/27	jun/27	jul/27	ago/27	set/27	out/27	nov/27	dez/27
Faixa 1	**Porto Lima**	**2.375**	**mar-26**		**45**	**45**	**45**	**45**	**45**	**45**	**45**	**45**	**45**	**29**											
Faixa 1	**Porto Seleta**	**2.375**	**jan-27**												**45**	**45**	**45**	**45**	**45**	**45**	**45**	**45**	**45**	**45**	**23**
Total de Vendas Lançados				**0**	**0**	**0**	**0**	**0**	**0**	**0**	**0**	**0**	**0**	**0**	**0**	**0**	**0**	**0**	**0**	**0**	**0**	**0**	**0**	**0**	**0**
Total de Vendas Lançados + Landbank				**0**	**45**	**45**	**45**	**45**	**45**	**45**	**45**	**45**	**45**	**29**	**45**	**45**	**45**	**45**	**45**	**45**	**45**	**45**	**45**	**45**	**23**
Total Mancha | Faixa 1					*100%*	*100%*	*100%*	*100%*	*100%*	*100%*	*100%*	*100%*	*100%*	*100%*	*100%*	*100%*	*100%*	*100%*	*100%*	*100%*	*100%*	*100%*	*100%*	*100%*	*100%*
Total Mancha | Faixa 2					*0%*	*0%*	*0%*	*0%*	*0%*	*0%*	*0%*	*0%*	*0%*	*0%*	*0%*	*0%*	*0%*	*0%*	*0%*	*0%*	*0%*	*0%*	*0%*	*0%*	*0%*
Total Mancha | Faixa 3					*0%*	*0%*	*0%*	*0%*	*0%*	*0%*	*0%*	*0%*	*0%*	*0%*	*0%*	*0%*	*0%*	*0%*	*0%*	*0%*	*0%*	*0%*	*0%*	*0%*	*0%*

Parecer de I.M sobre a mancha:

O projeto analisado em comitê está em linha com o potencial teórico de demanda calculado para a mancha. (Total Lançados)

Canibalização:

Sem Risco de Canibalização

Porto Lima | Mapa Concorrência

		Porto Lima	Varandas Mendanha
		TENDA	Engefic
	Distância Tenda (km)		1,61km
Região 1 Km	População	7.329	23.945
	Dens. Demográfica	2.347	7.671
	Renda (R$)	5.265	6.834
	Classe Social	C1 (de R$ 3.1K a 5.4K)	B2 (de R$ 5.4K a 9.8K)
	PEA Dia	6.772	12.122
Quantitativo	Lançamento	mar/26	jul/25
	Unidades	434	320
	Estoque	434	106
	VSO	45	31
	Stockout	10	3
Qualitativo	Condomínios	1	1
	Torres	6	6
	Gabarito	T+4	T+4
	Plantas (m²)	34,1m²	44,6m² - 70,1m²
	Tipologia	2 Dorms	2 Dorms
	Opções	Não	Garden
	Varanda	Não	Sim
	Vagas	12%	Rotativa
	Lazer	Bicicletário, Playpet, playkids, praça de chegada, mini quadra, espaço ducha, salão de festas com churrasqueira gourmet, fitness externo, 6 unidades de lazer interno com sugestão de Mini market	Mini Market, Bicicletário, Piscina, Churrasqueira, Salão de Festas, Espaço Conveniência, Quadra, Espaço Fitness, Brinquedoteca, Playground, Pet Place

Farol Renda
Acima de 300
Entre 0 e 300
Abaixo de 0

Diagnóstico Concorrência

- A concorrência possui target de preço e renda acima ao previsto para o Porto Lima.

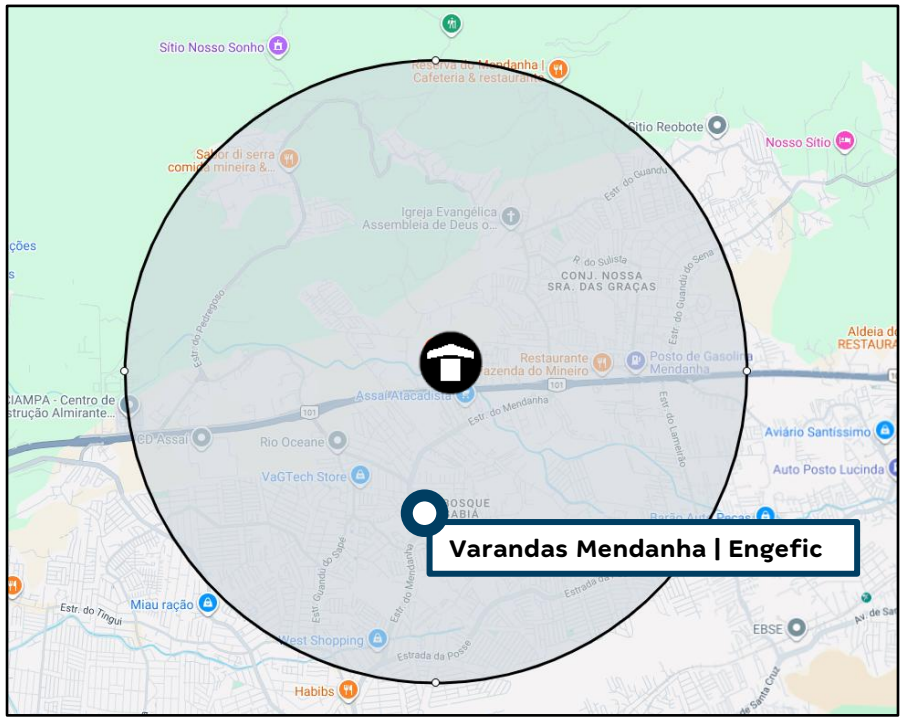

- Tipologias	Porto Lima Avaliação	Porto Lima Preço Nominal	Porto Lima CEF	Porto Lima Renda	Porto Lima % Unidades	Varandas Mendanha Avaliação	Varandas Mendanha Preço Nominal	Varandas Mendanha CEF	Varandas Mendanha Renda	Varandas Mendanha Dif	Varandas Mendanha Farol
Uh tipo	205.000	200.266	160.502	2.341	88%	264.000	244.000	211.200	5.171	2.830	●
Vg Carro	220.000	211.956	165.784	2.628	12%	-	-	-	-	-	-

Informações Viabilidade

Projeto:	Porto Lima			
Tipo:	Uh tipo		Uh tipo	
Método	**Ref - Porto Valencia**		**Vision**	
Avaliação	205.000		205.000	
Renda Inicial (VF)	2.476		2.521	
Renda Final*	2.341		0	
% RET1	75%		100%	
Tipo:	VF	R$	VF	R$
Ato	0,28	660	0,53	1.278
FGTS	0,14	338	0,57	1.370
Financiamento	93,49%	133.598	94,11%	136.768
Subsídio	129,91%	26.565	115,22%	21.960
Prazo de Pró-soluto	19	19	19	19
Pró-Soluto	90,51%	15.471	89,42%	15.562
Preço Raso (RS)	176.633	176.633	176.937	176.937
TCD	94,69%	23.633	93,16%	23.674
VSO	41	41	41	41
Preço de Venda	**210.280**	**210.280**	**210.641**	**210.641**
Elasticidade	-4,762%	-4,762%	-4,762%	-4,762%
Preço de Venda Final	**200.266**	**200.266**	**200.611**	**200.611**
Preço Raso (R$)	**176.633**		**176.937**	
% de Raso	**88,20%**		**88,20%**	
BP25 - Não Inflacionado	**-**		**-**	
BP25 - Inflacionado	**-**		**-**	

Informações Viabilidade

Projeto:	Porto Lima			
Tipo:	**Vg Carro**		**Vg Carro**	
Método	**Ref - Porto Valencia**		**Vision**	
Avaliação	220.000		220.000	
Renda Inicial (VF)	2.990		3.043	
Renda Final*	2.628		0	
% RET1	50%		100%	
Tipo:	**VF**	**R$**	**VF**	**R$**
Ato	0,59	1.671	0,72	2.088
FGTS	0,75	2.126	1,03	2.974
Financiamento	90,52%	145.201	95,14%	154.876
Subsídio	226,87%	18.457	104,67%	7.605
Prazo de Pró-soluto	19	19	19	19
Pró-Soluto	94,40%	19.489	97,08%	20.393
Preço Raso (RS)	186.943	186.943	187.937	187.937
TCD	82,98%	25.013	81,98%	25.146
VSO	4	4	4	4
Preço de Venda	**222.554**	**222.554**	**223.737**	**223.737**
Elasticidade	-4,762%	-4,762%	-4,762%	-4,762%
Preço de Venda Final	**211.956**	**211.956**	**213.082**	**213.082**
Preço Raso (R$)	**186.943**		**187.937**	
% de Raso	**88,20%**		**88,20%**	
BP25 - Não Inflacionado	**-**		**-**	
BP25 - Inflacionado	**-**		**-**	

Análise de Preço

Informações Viabilidade

Projeto:	Porto Lima
Tipo:	**Faixa 2**
Método	**Ref - Porto Valencia**
Avaliação	206.797
Renda Inicial (VF)	2.538
Renda Final*	2.375

Tipo:	VF	R$
Ato	0,32	781
FGTS	0,22	552
Financiamento	93,13%	134.989
Subsídio	141,53%	25.594
Prazo de Pró-soluto	19	19
Pró-Soluto	90,98%	15.953
Preço Raso (RS)	177.868	177.868
TCD	93,29%	23.799
VSO	45	45
Preço de Venda	**211.270**	**211.270**
Elasticidade	-4,762%	-4,762%
Preço de Venda Final	**201.667**	**201.667**

Preço Raso (R$)	**177.868**
% de Raso	**88,20%**
Raso Todas as Fases	**181.732**
Nominal Todas as Fases	**206.048**

1

Análise de Riscos	Farol IM
IM avalia o preço Referencia como **factível**.	

1) O empreendimento está inserido em uma região de renda média baixa, com oferta limitada de polos de serviços. Ainda assim, conta com um importante diferencial de mobilidade, o fácil acesso à Avenida Brasil, via que conecta o bairro aos principais pontos de interesse da cidade.

Adicionalmente, o projeto mantém um posicionamento de preço acessível, sendo o mais competitivo frente aos concorrentes diretos da região.

	Preço Real					Preço Normalizado (19m)	
	Avaliação	Preço Raso	Renda Mediana	VSO	PSOL	Δ PSOL	Preço Raso
Porto Valência F2	206.900	188.274	2.526	35	21	-2.132	186.142
Parque Hortência	196.150	183.660	2.412	25	17	2.008	185.668
Porto Lima	206.797	177.868	2.538	45	19	-	177.868

Resumo de Preços

Vision

Nome Fase	Tipologia	Renda	Ato	FGTS	Cond.	Subsídio	PSOL	TCD	VSO	Nom. Pré	Avali.	Elast.	Nom. Pós	Raso Pós	PSOL (m)	RET1
Porto Seleta	Uh tipo	2.476	0,28	0,14	93,5%	129,9%	90,5%	98,6%	41	219.004	205.000	-4,7619%	208.575	183.961	28	75%
Porto Seleta	Vg Carro	2.990	0,59	0,75	90,5%	226,9%	94,4%	87,1%	4	233.544	220.000	-4,7619%	222.423	196.175	28	50%

Análise de Preço

Informações Viabilidade

Projeto:	Porto Lima
Tipo:	**Faixa 2**
Método	**Ref - Porto Valencia**
Avaliação	206.797
Renda Inicial (VF)	2.538
Renda Final*	2.375

Tipo:	VF	R$
Ato	0,32	781
FGTS	0,22	552
Financiamento	93,13%	134.989
Subsídio	141,53%	25.594
Prazo de Pró-soluto	19	19
Pró-Soluto	90,98%	15.953
Preço Raso (RS)	177.868	177.868
TCD	93,29%	23.799
VSO	45	45
Preço de Venda	**211.270**	**211.270**
Elasticidade	-4,762%	-4,762%
Preço de Venda Final	**201.667**	**201.667**
Preço Raso (R$)	**177.868**	
% de Raso	**88,20%**	
Raso Todas as Fases	**181.732**	
Nominal Todas as Fases	**206.048**	

1

Análise de Riscos	Farol IM
Ciclo avalia o preço Referencia como **factível**.	

Tenda

sua próxima conquista

Cenário Aprovação

Informações Viabilidade

Projeto:	Porto Lima			
Tipo:	Uh tipo		Uh tipo	
Método	**Ref - Porto Valencia**		**Vision**	
Avaliação	205.000		205.000	
Renda Inicial (VF)	2.476		2.521	
Renda Final*	-		-	
% RET1	75%		75%	
Tipo:	VF	R$	VF	R$
Ato	0,28	699	0,53	1.355
FGTS	0,14	358	0,57	1.452
Financiamento	93,49%	141.614	94,11%	144.974
Subsídio	129,91%	28.159	115,22%	23.277
Prazo de Pró-soluto	17	17	17	17
Pró-Soluto	95,94%	14.673	94,78%	14.759
Preço Raso (RS)	185.504	185.504	185.816	185.816
TCD	99,45%	24.820	97,84%	24.862
VSO	29	29	29	29
Preço de Venda	**208.341**	**208.341**	**208.691**	**208.691**
Elasticidade	0,952%	0,952%	0,952%	0,952%
Preço de Venda Final	**210.325**	**210.325**	**210.679**	**210.679**
Preço Raso (R$)	**185.504**		**185.816**	
% de Raso	**88,20%**		**88,20%**	
BP25 - Não Inflacionado	**0**		**0**	
BP25 - Inflacionado	**0**		**0**	

Informações Viabilidade

Projeto:	Porto Lima			
Tipo:	**Vg Carro**		**Vg Carro**	
Método	**Ref - Porto Valencia**		**Vision**	
Avaliação	220.000		220.000	
Renda Inicial (VF)	2.990		3.043	
Renda Final*	-		-	
% RET1	50%		50%	
Tipo:	**VF**	**R$**	**VF**	**R$**
Ato	0,59	1.771	0,72	2.213
FGTS	0,75	2.253	1,03	3.153
Financiamento	90,52%	153.913	95,14%	164.169
Subsídio	226,87%	19.564	104,67%	8.061
Prazo de Pró-soluto	17	17	17	17
Pró-Soluto	100,07%	18.483	102,90%	19.341
Preço Raso (RS)	195.985	195.985	196.937	196.937
TCD	86,99%	26.223	85,91%	26.350
VSO	4	4	4	4
Preço de Venda	**220.112**	**220.112**	**221.181**	**221.181**
Elasticidade	0,952%	0,952%	0,952%	0,952%
Preço de Venda Final	**222.208**	**222.208**	**223.287**	**223.287**
Preço Raso (R$)	**195.985**		**196.937**	
% de Raso	**88,20%**		**88,20%**	
BP25 - Não Inflacionado	**0**		**0**	
BP25 - Inflacionado	**0**		**0**	

Resumo de Preços

Vision

Nome Fase	Tipologia	Renda	Ato	FGTS	Cond.	Subsídio	PSOL	TCD	VSO	Nom. Pré	Avali.	Elast.	Nom. Pós	Raso Pós	PSOL (m)	RET1
Porto Seleta	Uh tipo	2.476	0,28	0,14	93,5%	129,9%	94,6%	98,5%	32,46	209.310	205.000	-0,4762%	208.313	183.730	18	75%
Porto Seleta	Vg Carro	2.990	0,59	0,75	90,5%	226,9%	98,7%	86,2%	3,923	221.333	220.000	-0,4762%	220.279	194.284	18	50%

- Pareceres
- Análise da Mancha e Implantação
- Prospecção
- Operações
- Inteligência de Mercado
- Financeiro

Informações Gerais – Consolidado

Porto Lima | Porto Seleta – RJ – Rio de Janeiro Capital

Datas e Prazos

	Compra	Lançamento	Início Obra	Término Obra	LÇTO até IO	IO até TO	Chaves	LÇTO até Chaves
Consolidado	out-23							
Porto Lima s/ vaga		mar-26	set-26	set-27	6 meses	12 meses	mar-29	36 meses
Porto Lima c/ vaga		mar-26	set-26	set-27	6 meses	12 meses	mar-29	36 meses
Porto Seleta s/ vaga		abr-27	out-27	nov-28	6 meses	13 meses	abr-30	36 meses
Porto Seleta c/ vaga		abr-27	out-27	nov-28	6 meses	13 meses	abr-30	36 meses

Terreno e Incorridos

TOTAL (R$ + Perm.):	8,50 MM	**Incorrido Terreno:**	0,70 MM	**Área do Terreno (100%):**	23.010 m²
Cash:	8,50 MM	**Nº de Parcelas Cash :**	44	**Custo de terreno m²:**	369,4
Permuta Financeira:	0,00 MM (0,00%)			**VaR 26 (R$ mil):**	1.334
Permuta Física:	0,00 MM (0,00%)			**VaR 27 (R$ mil):**	0
Ato / %VGV:	0,35 MM / 0,2%	**usto Adc. Ambientes:**	32,31 M	**Incorrido de Construção:**	0,03 MM

Área Líquida do Terreno:	22.905 m²
Custo de terreno m² Área Líquida:	371,1
Fração Terreno/Terreno + Custo Obra (%VGV):	4,4% / 50,9%
CA Máx/Proj.	3,0 / 1,6
Incorridos de Incorporação:	0,83 MM

Vendas

Fases	Nº Pavimentos	Preço Raso Unit.	Qtde	Preço Unit.	Aval. CEF	% de Selling Adc:	% Crédito Tenda	% TCD
Porto Lima s/ vaga	T+4	185.504	381	210.325	205.000	-0,4%	80,9%	11,8%
Porto Lima c/ vaga	T+4	195.985	53	222.208	220.000	-0,3%	79,1%	11,8%
Porto Seleta s/ vaga	T+4	183.730	422	208.313	205.000	-0,4%	80,5%	11,8%
Porto Seleta c/ vaga	T+4	194.284	51	220.279	220.000	-0,3%	78,6%	11,8%

Unidades Totais:	907	**Preço Médio:**	210.643	**Renda Média:**	2.535	**ITBI+Emol. Unit. Médio:**	3.661
Unidades Tenda:	907	**Avaliação Média:**	206.720	**Ato:**	816 (0,3)	**Custo do Ciclo Unit.:**	14.651
VSO:	34,8846153846154 U	**VGV Total:**	191.053.315	**FGTS:**	571 (0,2)	**Preço Raso Médio:**	185.785
RET Médio:	1,8%	**VGV Tenda:**	191.053.315	**% em RET 1%:**	72%	**Adc. Tx. de Aceleração Médio:**	600

Construção

Custo Total Unit.:	97.804	**Eventuais:**	2,00%	**Área priv (m²):**	34,10	**Gape / Mês Unit.:**	9,42

Resultado

LI (R$):	**32.652.177**	**LI:**	**23,02%**	**Exposição de Caixa (R$):**	**19.649.101**	**Margem Bruta Econômica:**	**41,23%**
TIR:	**93,43%**	**LI Aprovação:**	**22,00%**	**Ger. Caixa 12 meses (R$):**	**(18.086.272)**	**Margem Bruta REF:**	**43,04%**
Exposição de Caixa:	**10,01%**	**Δ LI:**	**1,02%**	**Ger. Caixa 24 meses (R$):**	**2.161.532**	**Margem Rasa Econômica:**	**32,39%**
Payback Contingente (21 m):	**16 m/ (-5 m)**	**LI Marginal:**	**24,42%**	**Ger. Caixa Marginal (R$):**	**59.226.858**	**Margem Rasa REF:**	**35,43%**
Payback Consolidado:	**16 meses**					**Margem de Contribuição Econômica:**	**30,50%**

DRE – Consolidado

R$ Mil - Valores Nominais - Compra	Porto Lima | Porto Seleta		Porto Lima s/ vaga		Porto Lima c/ vaga		Porto Seleta s/ vaga		Porto Seleta c/ vaga	
	Nominal	%	Nominal	%	Nominal	%	Nominal	%	Nominal	%
Receita	196.371	100,0%	80.160	100,0%	11.724	100,0%	92.769	100,0%	11.717	100,0%
PIS/COFINS	(1.979)	1,0%	(769)	1,0%	(161)	1,4%	(889)	1,0%	(160)	1,4%
Custo Total	(114.234)	58,8%	(46.604)	58,7%	(6.465)	55,9%	(54.566)	59,4%	(6.599)	57,1%
Custo Terreno	(9.188)	4,7%	(3.860)	4,9%	(537)	4,6%	(4.275)	4,7%	(517)	4,5%
Custo Relacionados a Terreno	(988)	0,5%	(412)	0,5%	(57)	0,5%	(463)	0,5%	(56)	0,5%
Custos de Incorporação	(5.868)	3,0%	(2.397)	3,0%	(316)	2,7%	(2.810)	3,1%	(344)	3,0%
Custo de Construção	(98.190)	50,5%	(39.936)	50,3%	(5.555)	48,0%	(47.017)	51,2%	(5.682)	49,2%
Lucro Bruto Econômico	80.157	41,2%	32.788	41,3%	5.098	44,1%	37.314	40,6%	4.958	42,9%
Lucro Bruto Raso Econômico	54.726	32,4%	22.428	32,5%	3.582	35,7%	25.284	31,7%	3.432	34,2%
Custo para Rateio	-	0,0%	-	0,0%	-	0,0%	-	0,0%	-	0,0%
Lucro Bruto Contábil	80.157	41,2%	32.788	41,3%	5.098	44,1%	37.314	40,6%	4.958	42,9%
Despesas de Selling	(17.546)	9,0%	(7.153)	9,0%	(1.052)	9,1%	(8.279)	9,0%	(1.062)	9,2%
Contingência	(3.328)	1,7%	(1.358)	1,7%	(199)	1,7%	(1.572)	1,7%	(199)	1,7%
Margem de Contribuição	59.283	30,5%	24.277	30,6%	3.847	33,3%	27.463	29,9%	3.697	32,0%
Margem de Contribuição Rasa	33.852	20,0%	13.917	20,2%	2.331	23,2%	15.433	19,3%	2.171	21,6%
IR e CSLL	(1.619)	0,8%	(629)	0,8%	(131)	1,1%	(728)	0,8%	(131)	1,1%
Margem Líquida	57.664	29,7%	23.648	29,8%	3.716	32,1%	26.735	29,1%	3.566	30,9%
Lucro Bruto REF Unit.	94.524	43,0%	91.737	43,0%	103.852	46,1%	94.231	42,3%	108.078	45,7%
Lucro Raso REF Unit.	68.642	35,4%	66.609	35,4%	77.310	38,9%	67.993	34,6%	80.200	38,5%

R$ Mil - VPL - Compra	Porto Lima | Porto Seleta		Porto Lima s/ vaga		Porto Lima c/ vaga		Porto Seleta s/ vaga		Porto Seleta c/ vaga	
	VP	%	VP	%	VP	%	VP	%	VP	%
Receitas	141.859	100,0%	63.438	100,0%	9.251	100,0%	61.539	100,0%	7.631	100,0%
PIS/COFINS	(1.410)	1,0%	(600)	0,9%	(125)	1,4%	(582)	0,9%	(103)	1,4%
Custos e Despesas Totais	(107.797)	76,0%	(47.612)	75,1%	(6.696)	72,4%	(47.667)	77,5%	(5.822)	76,3%
Custo Terreno	(7.433)	5,2%	(3.122)	4,9%	(434)	4,7%	(3.458)	5,6%	(418)	5,5%
Custo Relacionados a Terreno	(1.083)	0,8%	(452)	0,7%	(63)	0,7%	(507)	0,8%	(61)	0,8%
Custos de Incorporação	(5.222)	3,7%	(2.283)	3,6%	(301)	3,3%	(2.349)	3,8%	(289)	3,8%
Custo de Construção	(76.873)	54,2%	(34.120)	53,8%	(4.746)	51,3%	(33.909)	55,1%	(4.098)	53,7%
Despesas de Selling	(14.604)	10,3%	(6.504)	10,3%	(956)	10,3%	(6.350)	10,3%	(793)	10,4%
Contingência	(1.428)	1,0%	(640)	1,0%	(94)	1,0%	(617)	1,0%	(78)	1,0%
IR e CSLL	(1.154)	0,8%	(491)	0,8%	(102)	1,1%	(476)	0,8%	(84)	1,1%
Lucro Imobiliário	32.652	23,0%	15.226	24,0%	2.429	26,3%	13.290	21,6%	1.706	22,4%

DRE – Fase

R$ Mil - Valores Nominais - Compra	Porto Lima | Porto Seleta		Primeira Fase		Demais Fases	
	Nominal	%	Nominal	%	Nominal	%
Receita	196.371	100,0%	91.884	100,0%	104.486	100,0%
PIS/COFINS	(1.979)	1,0%	(929)	1,0%	(1.050)	1,0%
Custo Total	(114.234)	58,8%	(53.069)	58,3%	(61.165)	59,1%
Custo Terreno	(9.188)	4,7%	(4.397)	4,8%	(4.792)	4,6%
Custo Relacionados a Terreno	(988)	0,5%	(469)	0,5%	(519)	0,5%
Custos de Incorporação	(5.868)	3,0%	(2.713)	3,0%	(3.155)	3,1%
Custo de Construção	(98.190)	50,5%	(45.491)	50,0%	(52.699)	50,9%
Lucro Bruto Econômico	80.157	41,2%	37.886	41,7%	42.271	40,9%
Lucro Bruto Raso Econômico	54.726	32,4%	26.010	32,9%	28.716	31,9%
Custo para Rateio	-	0,0%	-	0,0%	-	0,0%
Lucro Bruto Contábil	80.157	41,2%	37.886	41,7%	42.271	40,9%
Despesas de Selling	(17.546)	9,0%	(8.205)	9,0%	(9.341)	9,0%
Contingência	(3.328)	1,7%	(1.557)	1,7%	(1.771)	1,7%
Margem de Contribuição	59.283	30,5%	28.124	30,9%	31.160	30,1%
Margem de Contribuição Rasa	33.852	20,0%	16.248	20,5%	17.604	19,6%
IR e CSLL	(1.619)	0,8%	(760)	0,8%	(859)	0,8%
Margem Líquida	57.664	29,7%	27.363	30,1%	30.301	29,3%
Lucro Bruto REF Unit.	94.524	43,0%	93.216	43,4%		
Lucro Raso REF Unit.	68.642	35,4%	67.916	35,9%		

R$ Mil - VPL - Compra	Porto Lima | Porto Seleta		Primeira Fase		Demais Fases	
	VP	%	VP	%	VP	%
Receitas	141.859	100,0%	72.689	100,0%	69.170	100,0%
PIS/COFINS	(1.410)	1,0%	(725)	1,0%	(685)	1,0%
Custos e Despesas Totais	(107.797)	76,0%	(54.308)	74,7%	(53.488)	77,3%
Custo Terreno	(7.433)	5,2%	(3.557)	4,9%	(3.876)	5,6%
Custo Relacionados a Terreno	(1.083)	0,8%	(515)	0,7%	(569)	0,8%
Custos de Incorporação	(5.222)	3,7%	(2.584)	3,6%	(2.638)	3,8%
Custo de Construção	(76.873)	54,2%	(38.866)	53,5%	(38.007)	54,9%
Despesas de Selling	(14.604)	10,3%	(7.460)	10,3%	(7.144)	10,3%
Contingência	(1.428)	1,0%	(733)	1,0%	(694)	1,0%
IR e CSLL	(1.154)	0,8%	(593)	0,8%	(561)	0,8%
Lucro Imobiliário	32.652	23,0%	17.656	24,3%	14.997	21,7%

Comparativo EE

Comparativo dos Estudos - Consolidado	Escritura	Atual	Atual vs Escritura	Δ%
Data Estudo:	fevereiro-26	março-26	1 Meses	N/A
Lançamento:	março-26	março-26	0 Meses	N/A
Uhs:	907	907	-	0,0%
Preço Nominal:	212.375	210.643	(1.731)	-0,8%
Preço Raso:	187.804	185.785	(2.019)	-1,1%
Preço Nominal Inflacionado:	222.303	219.597	(2.705)	-1,2%
Preço Raso Inflacionado:	196.618	193.715	(2.903)	-1,5%
Renda Média:	2.581	2.535	(46)	-1,8%
RET Médio:	1,84%	1,84%	0,0 p.p.	0,0%
% em RET 1%:	72,13%	72,13%	0,0 p.p.	0,0%
VSO:	35	35	-	0,0%
ITBI/Emol. Inf (Unit)[2]:	4.399	4.381	(18)	-0,4%
Avaliação:	202.491	206.720	4.229	2,1%
Prazo construção F1:	12	12	-	0,0%
Prazo de Pró-Soluto F1:	17	17	-	0,0%
Custo Total Inf (Unit):	122.875	125.947	3.072	2,5%
Custo Construção (Unit):	94.126	97.804	3.678	3,9%
Fração de construção:	44,3%	46,4%	2,1 p.p.	4,8%
INCC Folha Rosto:	1.228,16	1.237,04	9	0,7%
Custo Terreno Inf:	9.188.291	9.188.291	-	0,0%
Custo Relacionados a Terreno (Unit):	1.138	1.089	(49)	-4,3%
Fração do Terreno[1]:	4,4% / 48,7%	4,4% / 50,9%	0,0 p.p.	0,0%
Custo de Incorp. por uh:	6.996	6.469	(527)	-7,5%
ITBI/Emol. Inf (Total)[2]:	3.990.031	3.973.841	(16.190)	-0,4%
Custo do Ciclo (Unit):	14.772	14.651	(121)	-0,8%
Lucro Imobiliário:	25,3%	23,0%	-2,3 p.p.	-9,0%
LI Marginal:	26,6%	24,4%	-2,2 p.p.	-8,2%
Exposição de caixa:	9,6%	10,0%	0,4 p.p.	3,7%
TIR:	101,9%	93,4%	-8,5 p.p.	-8,3%
Margem Bruta REF:	45,2%	43,0%	-2,2 p.p.	-4,8%
Margem Bruta Econômica:	43,3%	41,2%	-2,1 p.p.	-4,9%
Margem Rasa REF:	38,1%	35,4%	-2,6 p.p.	-6,9%
Margem Rasa Econômica:	35,0%	32,4%	-2,6 p.p.	-7,5%
Margem Contribuição Econômica:	32,6%	30,5%	-2,1 p.p.	-6,5%
Payback Contingente (Régua 21 m):	16 m/ (-5 m)	16 m/ (-5 m)	0	
Payback Consolidado:	16 Meses	16 Meses	0 Meses	0,0%

[1] Valor do terreno contratual

[2] ITBI com taxa de Aceleração

Informações Gerais – Consolidado

Porto Lima | Porto Seleta – RJ – Rio de Janeiro Capital

Datas e Prazos

	Compra	Lançamento	Início Obra	Término Obra	LÇTO até IO	IO até TO	Chaves	LÇTO até Chaves
Consolidado	out-23							
Porto Lima s/ vaga		mar-26	nov-26	nov-27	8 meses	12 meses	mar-29	36 meses
Porto Lima c/ vaga		mar-26	nov-26	nov-27	8 meses	12 meses	mar-29	36 meses
Porto Seleta s/ vaga		jan-27	mai-28	jun-29	16 meses	13 meses	jan-30	36 meses
Porto Seleta c/ vaga		jan-27	mai-28	jun-29	16 meses	13 meses	jan-30	36 meses

Terreno e Incorridos

TOTAL (R$ + Perm.):	8,50 MM	**Incorrido Terreno:**	0,70 MM	**Área do Terreno (100%):**	23.010 m²	**Área Líquida do Terreno:**	22.905 m²
Cash:	8,50 MM	**Nº de Parcelas Cash :**	44	**Custo de terreno m²:**	369,4	**Custo de terreno m² Área Líquida:**	371,1
Permuta Financeira:	0,00 MM (0,00%)			**VaR 26 (R$ mil):**	1.334	**Fração Terreno/Terreno + Custo Obra (%VGV):**	4,5% / 52,1%
Permuta Física:	0,00 MM (0,00%)			**VaR 27 (R$ mil):**	0	**CA Máx/Proj.**	3,0 / 1,6
Ato / %VGV:	0,35 MM / 0,2%	**Custo Adc. Ambientes:**	32,31 M	**Incorrido de Construção:**	0,03 MM	**Incorridos de Incorporação:**	0,83 MM

Vendas

Fases	Nº Pavimentos	Preço Raso Unit.	Qtde	Preço Unit.	Aval. CEF	% de Selling Adc:	% Crédito Tenda	% TCD
Porto Lima s/ vaga	T+4	176.632	381	200.265	205.000	-0,4%	80,1%	11,8%
Porto Lima c/ vaga	T+4	186.944	53	211.957	220.000	-0,3%	78,2%	11,8%
Porto Seleta s/ vaga	T+4	183.961	422	208.575	205.000	-0,4%	77,0%	11,8%
Porto Seleta c/ vaga	T+4	196.175	51	222.423	220.000	-0,3%	74,5%	11,8%

Unidades Totais:	907	**Preço Médio:**	206.061	**Renda Média:**	2.535	**ITBI+Emol. Unit. Médio:**	3.661
Unidades Tenda:	907	**Avaliação Média:**	206.720	**Ato:**	776 (0,3)	**Custo do Ciclo Unit.:**	14.333
VSO:	45 Unidades	**VGV Total:**	186.896.909	**FGTS:**	543 (0,2)	**Preço Raso Médio:**	181.743
RET Médio:	1,8%	**VGV Tenda:**	186.896.909	**% em RET 1%:**	72%	**Adc. Tx. de Aceleração Médio:**	600

Construção

Custo Total Unit.:	97.989	**Eventuais:**	2,00%	**Área priv (m²):**	34,10	**Gape / Mês Unit.:**	9,42

Resultado

LI (R$):	**27.362.876**	**LI:**	**20,47%**	**Exposição de Caixa (R$):**	**16.216.507**	**Margem Bruta Econômica:**	**39,01%**
TIR:	**82,16%**	**LI Aprovação:**	**22,00%**	**Ger. Caixa 12 meses (R$):**	**(13.258.231)**	**Margem Bruta REF:**	**40,15%**
Exposição de Caixa:	**8,42%**	**Δ LI:**	**-1,53%**	**Ger. Caixa 24 meses (R$):**	**8.190.372**	**Margem Rasa Econômica:**	**29,62%**
Payback Contingente (21 m):	**16 m/ (-5 m)**	**LI Marginal:**	**21,96%**	**Ger. Caixa Marginal (R$):**	**54.005.899**	**Margem Rasa REF:**	**32,16%**
Payback Consolidado:	**18 meses**					**Margem de Contribuição Econômica:**	**28,33%**

DRE – Consolidado

R$ Mil - Valores Nominais - Compra	Porto Lima | Porto Seleta		Porto Lima s/ vaga		Porto Lima c/ vaga		Porto Seleta s/ vaga		Porto Seleta c/ vaga	
	Nominal	%	Nominal	%	Nominal	%	Nominal	%	Nominal	%
Receita	192.679	100,0%	76.811	100,0%	11.199	100,0%	92.793	100,0%	11.876	100,0%
PIS/COFINS	(1.942)	1,0%	(737)	1,0%	(153)	1,4%	(890)	1,0%	(163)	1,4%
Custo Total	(116.332)	61,0%	(46.965)	61,7%	(6.516)	59,0%	(56.071)	61,0%	(6.781)	57,9%
Custo Terreno	(9.188)	4,8%	(3.860)	5,1%	(537)	4,9%	(4.275)	4,7%	(517)	4,4%
Custo Relacionados a Terreno	(1.072)	0,6%	(447)	0,6%	(62)	0,6%	(502)	0,5%	(61)	0,5%
Custos de Incorporação	(5.846)	3,1%	(2.399)	3,2%	(316)	2,9%	(2.789)	3,0%	(342)	2,9%
Custo de Construção	(100.227)	52,5%	(40.260)	52,9%	(5.600)	50,7%	(48.505)	52,8%	(5.862)	50,0%
Lucro Bruto Econômico	74.405	39,0%	29.109	38,3%	4.530	41,0%	35.833	39,0%	4.932	42,1%
Lucro Bruto Raso Econômico	48.953	29,6%	19.131	28,9%	3.073	32,0%	23.408	29,5%	3.341	33,0%
Custo para Rateio	-	0,0%	-	0,0%	-	0,0%	-	0,0%	-	0,0%
Lucro Bruto Contábil	74.405	39,0%	29.109	38,3%	4.530	41,0%	35.833	39,0%	4.932	42,1%
Despesas de Selling	(17.107)	9,0%	(6.868)	9,0%	(1.014)	9,2%	(8.171)	8,9%	(1.054)	9,0%
Contingência	(3.265)	1,7%	(1.302)	1,7%	(190)	1,7%	(1.573)	1,7%	(201)	1,7%
Margem de Contribuição	54.032	28,3%	20.939	27,5%	3.326	30,1%	26.089	28,4%	3.677	31,4%
Margem de Contribuição Rasa	28.581	17,3%	10.961	16,6%	1.869	19,5%	13.664	17,2%	2.086	20,6%
IR e CSLL	(1.589)	0,8%	(603)	0,8%	(126)	1,1%	(728)	0,8%	(133)	1,1%
Margem Líquida	52.443	27,5%	20.337	26,7%	3.201	29,0%	25.361	27,6%	3.544	30,3%
Lucro Bruto REF Unit.	85.453	40,1%	79.783	39,5%	92.512	43,1%	87.589	39,9%	102.803	43,8%
Lucro Raso REF Unit.	60.377	32,2%	55.965	31,4%	67.194	35,4%	61.720	31,9%	75.147	36,3%

R$ Mil - VPL - Compra	Porto Lima | Porto Seleta		Porto Lima s/ vaga		Porto Lima c/ vaga		Porto Seleta s/ vaga		Porto Seleta c/ vaga	
	VP	%	VP	%	VP	%	VP	%	VP	%
Receitas	133.651	100,0%	60.104	100,0%	8.686	100,0%	57.504	100,0%	7.357	100,0%
PIS/COFINS	(1.329)	1,0%	(568)	0,9%	(117)	1,4%	(544)	0,9%	(99)	1,4%
Custos e Despesas Totais	(104.959)	78,5%	(46.829)	77,9%	(6.565)	75,6%	(45.936)	79,9%	(5.629)	76,5%
Custo Terreno	(7.433)	5,6%	(3.122)	5,2%	(434)	5,0%	(3.458)	6,0%	(418)	5,7%
Custo Relacionados a Terreno	(1.159)	0,9%	(484)	0,8%	(67)	0,8%	(543)	0,9%	(66)	0,9%
Custos de Incorporação	(5.126)	3,8%	(2.259)	3,8%	(298)	3,4%	(2.287)	4,0%	(282)	3,8%
Custo de Construção	(74.054)	55,4%	(33.509)	55,8%	(4.661)	53,7%	(32.015)	55,7%	(3.869)	52,6%
Despesas de Selling	(14.781)	11,1%	(6.392)	10,6%	(921)	10,6%	(6.626)	11,5%	(841)	11,4%
Contingência	(1.319)	1,0%	(597)	1,0%	(87)	1,0%	(563)	1,0%	(72)	1,0%
IR e CSLL	(1.087)	0,8%	(465)	0,8%	(96)	1,1%	(445)	0,8%	(81)	1,1%
Lucro Imobiliário	27.363	20,5%	12.706	21,1%	2.004	23,1%	11.024	19,2%	1.628	22,1%

DRE – Fase

R$ Mil - Valores Nominais - Compra	Porto Lima | Porto Seleta		Primeira Fase		Demais Fases	
	Nominal	%	Nominal	%	Nominal	%
Receita	192.679	100,0%	88.010	100,0%	104.670	100,0%
PIS/COFINS	(1.942)	1,0%	(890)	1,0%	(1.052)	1,0%
Custo Total	(116.332)	61,0%	(53.481)	61,4%	(62.852)	60,7%
Custo Terreno	(9.188)	4,8%	(4.397)	5,0%	(4.792)	4,6%
Custo Relacionados a Terreno	(1.072)	0,6%	(509)	0,6%	(563)	0,5%
Custos de Incorporação	(5.846)	3,1%	(2.715)	3,1%	(3.131)	3,0%
Custo de Construção	(100.227)	52,5%	(45.860)	52,6%	(54.366)	52,5%
Lucro Bruto Econômico	74.405	39,0%	33.639	38,6%	40.765	39,3%
Lucro Bruto Raso Econômico	48.953	29,6%	22.204	29,3%	26.749	29,9%
Custo para Rateio	-	0,0%	-	0,0%	-	0,0%
Lucro Bruto Contábil	74.405	39,0%	33.639	38,6%	40.765	39,3%
Despesas de Selling	(17.107)	9,0%	(7.882)	9,0%	(9.225)	8,9%
Contingência	(3.265)	1,7%	(1.492)	1,7%	(1.774)	1,7%
Margem de Contribuição	54.032	28,3%	24.266	27,9%	29.767	28,7%
Margem de Contribuição Rasa	28.581	17,3%	12.830	17,0%	15.750	17,6%
IR e CSLL	(1.589)	0,8%	(728)	0,8%	(861)	0,8%
Margem Líquida	52.443	27,5%	23.537	27,0%	28.906	27,9%
Lucro Bruto REF Unit.	85.453	40,1%	81.337	39,9%		
Lucro Raso REF Unit.	60.377	32,2%	57.336	31,9%		

R$ Mil - VPL - Compra	Porto Lima | Porto Seleta		Primeira Fase		Demais Fases	
	VP	%	VP	%	VP	%
Receitas	133.651	100,0%	68.790	100,0%	64.860	100,0%
PIS/COFINS	(1.329)	1,0%	(686)	1,0%	(643)	1,0%
Custos e Despesas Totais	(104.959)	78,5%	(53.394)	77,6%	(51.565)	79,5%
Custo Terreno	(7.433)	5,6%	(3.557)	5,2%	(3.876)	6,0%
Custo Relacionados a Terreno	(1.159)	0,9%	(551)	0,8%	(608)	0,9%
Custos de Incorporação	(5.126)	3,8%	(2.557)	3,7%	(2.569)	4,0%
Custo de Construção	(74.054)	55,4%	(38.171)	55,5%	(35.884)	55,3%
Despesas de Selling	(14.781)	11,1%	(7.313)	10,6%	(7.467)	11,5%
Contingência	(1.319)	1,0%	(684)	1,0%	(635)	1,0%
IR e CSLL	(1.087)	0,8%	(561)	0,8%	(526)	0,8%
Lucro Imobiliário	27.363	20,5%	14.711	21,4%	12.652	19,5%

Pareceres

Análise da Mancha e Implantação

Prospecção

Operações

Inteligência de Mercado

Financeiro

Anexo

Equipado e ambientado

#	Equipados e Ambientados	32.314
	Brinquedoteca	14.124
	Espaço Teen	22.303
	Fitness	44.541
	Espaço Oficina	8.295
	Sport Bar	27.543
	Salão de Festas Gourmet	32.907
	Espaço Saúde	19.820
	Espaço Office	13.013
	Delivery (+Mini Market)	6.190
	Hall	5.214
1	Churrasqueira Gourmet	5.652
1	Salão de Festas Anexo	18.226
1	Churrasqueira anexa ao Festas	8.436

Obrigado