Tenda

sua próxima conquista

Book de Escritura

Regional: RS

Projeto: Solar do Bosque

Data Comitê: 28/04/2025

One Page – Solar do Bosque

[1]

Cidade	Porto Alegre	**Mancha de demanda**	- PZN - Porto Alegre Zona No
Regional	RS	**Cluster MPR**	1 - Vermelho
Cenário de Aprovação	Aprovação	**Tipo de Aprovação**	Consolidado
Fase Anterior	N/A		
Tipo de Comitê	Escritura	**Versão da VF**	Versão 1.0: Abr

Unidades (% Vagas)	690 (33%)	**CA Máx | Proj**	1,3 | 1,3
Tipologia	F2 - Concreto	**Escritura**	mai-25
Fases	2 fases	**Lçto | Duração (m)**	jun/25 | 30

[2]

Valor Líquido do Terreno (% VGV)	11.079 (8,0%)	**Un. Perm. Fís (% Ter)**	0 (0,0%)
Cash (Correção)	0 (IPCA)	**%VGV Perm Fin Líquida (% Ter)**	8,0% (100,0%)
Valor R$/m²	581	**VAR (%VGV)**	000 (0,0%)

[3]

Custo Construção (%VGV)	65.010 (46,9%)	**Indireto Unit.**	17.283
Prazo da Obra (meses)	15	**Torre Unit.**	45.737
Custo Total Unit. | Corrigido (LPU):	94.218 | 93.849 (89)	**Infra Unit.**	20.937
Início de Obra	dez-25	**Fundação Unit.**	9.309

[4]

Preço Nominal Unit.	200.701	**VSO**	27
Preço Raso Unit.	179.501	**Referência**	Vision
Avaliação Unit.	218.942	**Renda (% em RET 1%)**	2.494 (68,7%)

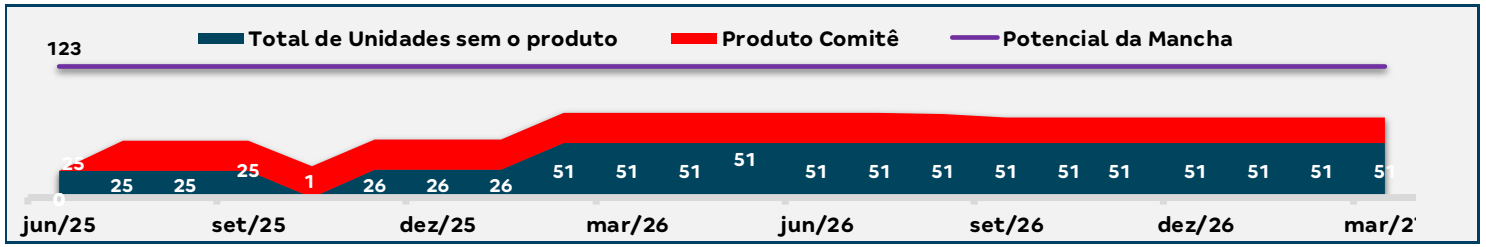

[5]

LI (Régua):	**22,4% (20,0%)**	**Margem Bruta Econômica:**	38,9%
LI Marginal:	22,9%	**Margem Rasa Econômica:**	31,1%
Margem Bruta REF:	41,0%	**Margem Contribuição Econômica:**	28,7%
Margem Rasa REF:	**34,1%**	**Exposição (% VGV):**	9.468 (6,6%)
TIR:	151,7%	**VGV Total:**	138.483
Payback Contingente (21 m) :	**17 m/ (-4 m)**	**Ger. Caixa 12 meses (R$):**	(6.747)
Payback Consolidado:	17	**Ger. Caixa 24 meses (R$):**	6.040

***Valores em R$ 1000**

Destaques

[1] Terreno localizado no município de **Porto Alegre**, em Santa Rosa de Lima, sequencia do empreendimento Parque Paris (mesmo bairro), em stockout desde dezembro/24.
O projeto passou por processo de reversão de tipologia (T+4 Hzinho -> T+4 modular), gerando um acréscimo de 190 unidades vs Projeto na tipologia anterior, totalizando **1 condomínio de 690 unidades.**

Projeto em processo de unificação de fases para o lançamento em junho.

O empreendimento possui 25% das unidades com vaga de estacionamento, totalizando 174 vagas, todas vinculadas.

[2] Negócio **100% em permuta financeira (8,0% do VGV)**, com valor estimado de R$ 11.000.000,00.
- Não há VGV mínimo estabelecido para este negócio;
- Quitação do saldo de permuta financeira em 48 meses após escritura, com desconto de 25%, a critério do permutante;

CVC assinado em novembro/2023.
- Cláusulas resolutivas de contrato com prazo de 18 meses após a baixa das suspensivas, superadas em nov/2023 (contrato vence em maio/25);

Garantia: Seguro Garantia de Pagamento em favor dos Vendedores, cotado em 400k (1% do valor do negócio).

Escritura aguarda emissão do projeto aprovado, previsto p/ 15/05.

Corretagem: R$ 296.000 (2,7% do Preço Terreno) pagos em 5 parcelas.

[3] Custo de obra consolidado de 94.218/uh

[4] Preço de venda desconsidera o subsídio estadual (20k/uh)

[5] Entrega acima dos Financials mínimos exigidos.

Pareceres

Análise da Mancha e Implantação

Prospecção

Operações

Inteligência de Mercado

Financeiro

Anexos

Pareceres

Área	Riscos Associados	Parecer	Criticidade
Jurídico	Due Diligence em renovação, com previsão para 30/04. Parecer anterior e visão preliminar da renovação não apontam óbices.	Ok com ressalvas	
Legalização	PL em revisão por legalização, será protocolado até 24/04.	Ok	
Produto	Sem riscos associados	Ok	
GETEC	Quantitativos concreto/aço Torre e Lajão conforme Engenharia de Produto	Ok com ressalvas	
Logística	Sem riscos associados	Ok	
Inteligência de mercado	IM avalia o Preço Referência como factível.	Ok	
Comercial/Ciclo	Parecer: Acreditamos que o preço é POSSÍVEL com o VSO proposto. Entendemos que esse empreendimento atenderá a demanda orgânica da sua microrregião, suprindo o stockout que seria gerado pelo Quinta do Lago Bolsena.	Ok	
Estudos Econômicos	Sem riscos associados	ok	

Pareceres

Análise da Mancha e Implantação

Prospecção

Operações

Inteligência de Mercado

Financeiro

Anexos

Mancha de Demanda

MANCHAS DE DEMANDA

- PZN – Porto Alegre Norte + Alvorada

Lançamento

1. Parque Paris
2. Quinta do Lago

LandBank

3. Quintana Parque
4. Estância do Sol
5. Solar do Bosque
6. Alto da Colina -Dallaesquina
7. Gran Boulevard
8. Alto da Encosta
9. Alvorecer Village
10. Sonata
11. Monte Verde

Cluster MPR – (Comitê)

Cluster 1 - Vermelho

Região

Borda

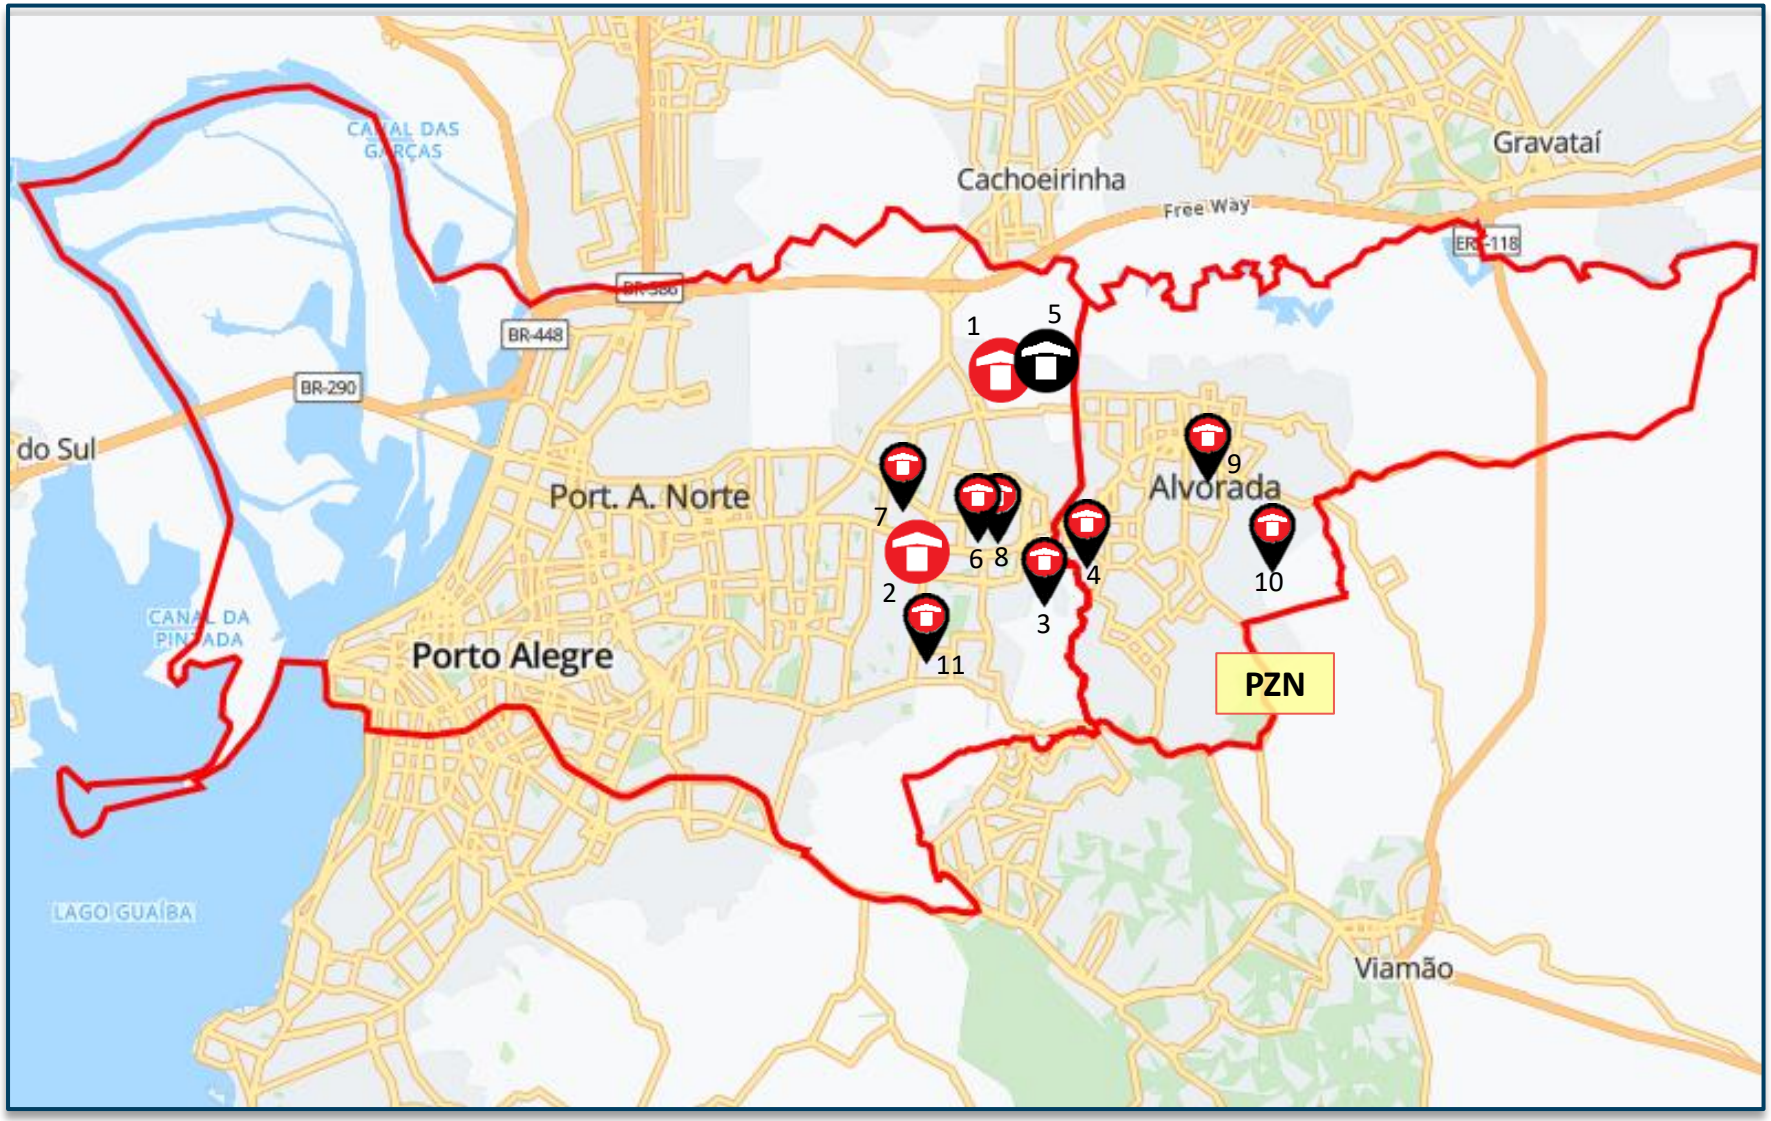

Lançados *LandBank* *Comitê*

Microlocalização – Bairro Santa Rosa de Lima

PRODUTO

Empreendimento Solar do Bosque
Descritivo - Escritura | Lançamento

Informações Gerais		
Terreno	Área terreno	19.074,66 m²
	Menor poligonal	19.074,66 m²
	App/fna	Não | Não
	Reserva de calçada/ melhoramento víario	Não | Não
	Área liquida	19.074,66 m²
	Zoneamento	MZ 03 UEU 10 QTR 001 - Zona de ocupação intensiva
	Ca máximo	1,30
	Ca projetado	1,30
	Gabarito máximo	18 m (T+05)
Geral	Total uh	690
	Total de vagas	225 (32,60%)
Tipologia	Tipologia	F002-IS2 FLEX
	Gabarito	T+04
	Lâmina	14pp | 16pp
	Área privativa	35,44m² | 35,64m² | 35,90m² | 35,72m²
	Varanda	N/A
Condomínio	Unidade pcd	21
	Unidade lazer | técnica	00 | 00
	Torre	09
	Fase	Fase 01 : 380uh | Fase 02 : 310uh
Lazer	Lazer externo	02 Salões de Festas, 01 Play Baby, 01 Churrasqueira Gourmet, 01 Chimarródromo, 01 Espaço Relax, 01 Play Kids, 01 Fitness Externo, 01 Quadra Gramada, 01 Espaço cultivo, 01 Play Pet.
	Lazer interno	N/A

Lazeres Externos :

1. Salão de Festas
2. Play Baby
3. Churrasqueira Gourmet
4. Chimarródromo
5. Espaço Relax
6. Play Kids
7. Fitness Externo
8. Quadra Gramada
9. Espaço Cultivo

PRODUTO

Empreendimento Solar do Bosque
Atributos de produto - Escritura | Lançamento

	Descrição	Criticidade	Parecer
Usabilidade	**Acesso Empreendimento**		
	Percurso do pedestre até torre		
Diferencial produto	**Prime**	Não	
	Supercondomínio	Não	
	Atributos Infra	Sim	02 Salões de Festas, 01 Play Baby, 01 Churrasqueira Gourmet, 01 Chimarródromo, 01 Espaço Relax, 01 Play Kids, 01 Fitness Externo, 01 Quadra Gramada, 01 Espaço cultivo, 01 Play Pet.
	Atributos Torre	Sim	Nova fachada
	Edifício Garagem	Não	

	Riscos associados	Parecer	Criticidade
Produto	Não há riscos associados	ok	

Play Kids

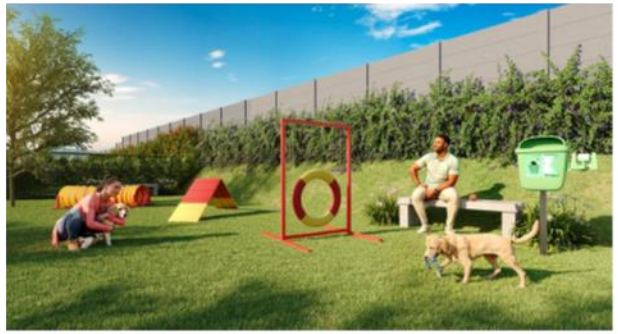
Play Pet

Quadra Gramada

Espaço Relax

Empreendimento Solar do Bosque
Modulação - Escritura | Lançamento

Fase 01 : 380uh (sendo 13 U.R.) – 130 vagas (sendo 04 PCD e 12 de moto) | Fase 02 : 310uh (sendo 08 U.R.) -

Módulo	Blocos	UH	Vagas	Parecer
Módulo 01	02 Blocos (16PP T+04)	160 UH (sendo 6 PCD)	89 vagas (sendo 2 PCD, 1 carga e descarga e 9 de moto)	O fitness externo, quadra gramada e o play kids foram alocados nos módulos 02 e 03 respectivamente devendo ser indicados na incorporação imobiliária neste formato.
Módulo 02	01 Bloco (16PP T+04)	80 UH (sendo 3 PCD)	41 vagas (sendo 2 PCD e 3 de moto)	
Módulo 03	02 Blocos (14PP T+04)	140 UH (sendo 4 PCD)	00 vagas	
Módulo 04	02 Blocos (16PP T+04)	160 UH (sendo 4 PCD)	20 vagas de moto	
Módulo 05	01 Bloco (16PP T+04) e 01 Bloco (14PP T+04)	150 UH (sendo 4 PCD)	75 vagas (sendo 11 de moto)	

Pareceres

Análise da Mancha e Implantação

Prospecção

Operações

Inteligência de Mercado

Financeiro

Anexos

Condições do Negócio

- **VALOR DO NEGÓCIO**
- **R$ 10.999.738 (8,00% do VGV)**

- **CONDIÇÃO**
  - **a) <u>100% Permuta Financeira</u>**
    - i. 8,0% do VGV a serem pagos em permuta financeira correspondente ao valor estimado de R$10.999.738;

- **PRAZOS CONTRATUAIS – CVC assinado em NOV/2023**
- Cláusulas Suspensivas com prazo de vencimento de 150 dias (05/2024) – **superado**;
- Cláusulas Resolutivas: 18 meses a partir da baixa das cláusulas suspensivas do contrato – **em andamento (aguarda aprovação do Projeto – previsto p/ 15/05)**;
- Quitação integral dos recebíveis em até 48 meses da escritura do imóvel. Caso haja valores pendentes de permuta financeira, será aplicado um desconto de 25% no montante a ser quitado.

- **CORREÇÃO MONETÁRIA**
- Não incide correção monetária sobre os valores de permuta financeira;

- **INTERMEDIAÇÃO IMOBILIÁRIA**
- R$296,0k (2,7% sobre o valor do terreno) a ser pago em 5 parcelas de R$59,2k cada, a primeira a ser paga 30 dias após a ECV;

- **GARANTIAS**
- **Em favor da Tenda:** N.A.
- **Em favor do Vendedor:** Seguro permuta no percentual de 1%.

➢ CONDIÇÕES RESOLUTIVAS PARA ECV

i. Obtenção da anuência dos confrontantes no eventual processo de retificação de área – **OK, superado;**
ii. Due Dilligence favorável – **em andamento, previsão de finalizar até 30/04 (sem riscos mapeados)**;
iii. Aprovação e Licenciamento do Projeto de Construção com no mínimo 500 unidades - **em andamento (prev. 30/04), aprovação de 690 unidades;**
iv. A existência de passivo ambiental, constatado após elaboração de laudos de cobertura vegetal, levantamento topográfico e planialtimétrico, e de contaminação no solo e/ou no lençol freático - **OK superado;**
v. A existência de qualquer medida, óbice e/ou empecilho, de natureza administrativa e/ou judicial de forma a impedir a remoção ou manipulação de eventual vegetação local, a qual deverá ser implementada anteriormente a outorga das escrituras públicas definitivas, ou ainda, a exigência de contrapartida financeira para se obter as devidas autorizações de manejo de vegetação – **OK, superado;**
vi. Inviabilidade técnica e financeira pela necessidade de execução de rede de água e esgoto que atenda ao empreendimento – **OK, superado;**
vii. Análise positiva da viabilidade técnica , financeira e comercial do Empreendimento – **em andamento (aprovação do comitê)**;
viii. A não viabilidade das redes de água e esgoto existentes no local, que sejam tidas como insuficientes a garantir a vazão necessária às unidades autônomas que comporão o Empreendimento pretendido – **OK, superado;**
ix. a inviabilidade de contratação de financiamento pela instituição financeira para construção do empreendimento antes mencionado, consoante os termos e condições do Programa do Governo Federal Casa Verde Amarela ou qualquer outro programa que venha a substituí-lo - **em andamento, sem riscos mapeados;**

Pareceres

Análise da Mancha e Implantação

Prospecção

Operações

Inteligência de Mercado

Financeiro

Anexos

Implantação

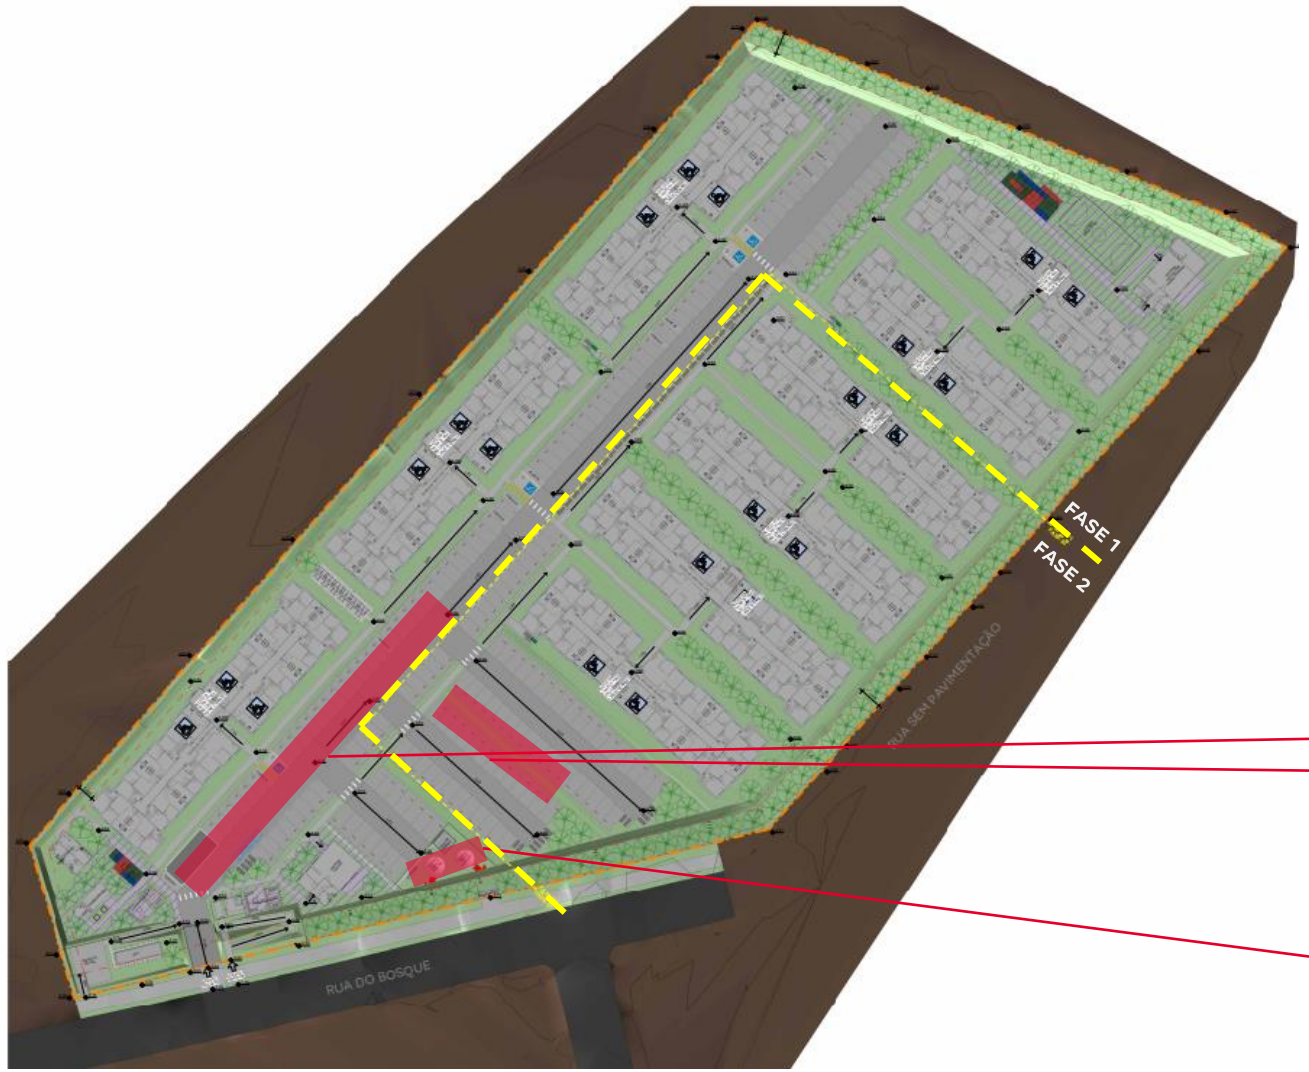

FASE 1

2 Torres 14PP | T+4
3 Torres 16PP | T+4
380 Unid. A Construir
380 Unid. A Vender

FASE 2

1 Torre 14PP | T+4
3 Torres 16PP | T+4
310 Unid. A Construir
310 Unid. A Vender

Enterrados
Bacia de amortecimento
Volume = 498 m³

2 Reservatórios
Ø 3,18m – 30,28 m

Custo de Construção

	SOLAR DO BOSQUE - F1 R01	SOLAR DO BOSQUE - F2 R01	SOLAR DO BOSQUE - CONSOLIDADO R01	SOLAR DO BOSQUE - UNIFICADO R01	SOLAR DO BOSQUE - F1 BP25	SOLAR DO BOSQUE - F2 BP25	SOLAR DO BOSQUE - CONSOLIDADO BP25
Torres	5	4	9	9	5	4	9
Unidades Construídas	380	310	690	690	380	310	690
Unidades Vendidas	380	310	690	690	380	310	690
Condomínios (qta.)	1	1	1	1	1	1	1
Cidade	Porto Alegre - RS	Porto Alegre - RS	Porto Alegre - RS	Porto Alegre - RS	Porto Alegre - RS	Porto Alegre - RS	Porto Alegre - RS
Produto / Selo	F2 MODULAR	F2 MODULAR	F2 MODULAR	F2 MODULAR	F2 MODULAR	F2 MODULAR	F2 MODULAR
Tipologia	2 Torres | T+4 | 14PP | C1A	1 Torre | T+4 | 14PP | C1A	3 Torres | T+4 | 14PP | C1A	3 Torres | T+4 | 14PP | C1A	2 Torres | T+4 | 14PP | C1A	1 Torre | T+4 | 14PP | C1A	3 Torres | T+4 | 14PP | C1A
Tipologia	3 Torres | T+4 | 16PP | C1A	3 Torres | T+4 | 16PP | C1A	6 Torres | T+4 | 16PP | C1A	6 Torres | T+4 | 16PP | C1A	3 Torres | T+4 | 16PP | C1A	3 Torres | T+4 | 16PP | C1A	6 Torres | T+4 | 16PP | C1A
Projeto Infra	EP	EP	EP	EP			
Projeto Torre	EP	EP	EP	EP			
Mês Base	abril-24	abril-24	abril-24	abril-24	outubro-24	outubro-24	outubro-24
Incc	1.178,386	1.178,386	1.178,386	1.178,386	1.134,775	1.134,775	1.134,775
LVS	fevereiro-25	fevereiro-25	fevereiro-25	fevereiro-25			
Indiretos	fevereiro-25	fevereiro-25	fevereiro-25	fevereiro-25			
Base de Preço	LPU 89	LPU 89	LPU 89	LPU 89			
Takt	2x2	2x2	2x2	2x2			
Prazo (mês)	15	11	15 | 11	18	13	12	13 | 12
CUSTO TOTAL I	R$ / UND R$ 101.615	R$ / UND R$ 82.733	R$ / UND R$ 93.132	R$ / UND R$ 90.045	R$ / UND R$ 91.087	R$ / UND R$ 76.459	R$ / UND R$ 84.515
Indireto	R$ 16.583	R$ 16.125	R$ 16.377	R$ 13.785	R$ 13.776	R$ 13.897	R$ 13.830
Torre	R$ 42.009	R$ 42.940	R$ 42.428	R$ 42.237	R$ 42.915	R$ 43.424	R$ 43.144
Infra	R$ 25.237	R$ 14.088	R$ 20.228	R$ 19.924	R$ 19.866	R$ 12.726	R$ 16.658
Fundação	R$ 9.094	R$ 9.573	R$ 9.309	R$ 9.309	R$ 7.421	R$ 6.406	R$ 6.965
EEE							
ETE							
Contenção	R$ 32		R$ 18	R$ 18			
Terraplenagem	R$ 8.658	R$ 7	R$ 4.771	R$ 4.771	R$ 7.109	R$ 7	R$ 3.918
CUSTO TOTAL II	R$ 1.086	R$ 1.086	R$ 1.086	R$ 1.086	R$ 1.438	R$ 1.438	R$ 1.438
Urbanização	R$ 278	R$ 278	R$ 278	R$ 278	R$ 267	R$ 267	R$ 267
Drenagem							
Extensão de Rede Elétrica	R$ 217	R$ 217	R$ 217	R$ 217	R$ 141	R$ 141	R$ 141
Extensão de Rede Hidráulica	R$ 591	R$ 591	R$ 591	R$ 591	R$ 1.029	R$ 1.029	R$ 1.029
CUSTO TOTAL III							
Incorridos							
CUSTO TOTAL IV							
Aprendizado							
CUSTO TOTAL V					R$ 3.556	R$ 2.994	R$ 3.303
Atualização por INCC					R$ 3.556	R$ 2.994	R$ 3.303
CUSTO TOTAL I+II	R$ 102.701	R$ 83.819	R$ 94.218	R$ 91.131	R$ 92.525	R$ 77.897	R$ 85.953
CUSTO TOTAL I AO IV	R$ 102.701	R$ 83.819	R$ 94.218	R$ 91.131	R$ 96.081	R$ 80.891	R$ 89.256

Custo de Construção

	SOLAR DO BOSQUE - CONSOLIDADO R01	SOLAR DO BOSQUE - CONSOLIDADO BP25
Torres	9	9
Unidades Construídas	690	690
Unidades Vendidas	690	690
Condomínios (qta.)	1	1
Cidade	Porto Alegre - RS	Porto Alegre - RS
Produto / Selo	F2 MODULAR	F2 MODULAR
Tipologia	3 Torres | T+4 | 14PP | C1A	3 Torres | T+4 | 14PP | C1A
Tipologia	6 Torres | T+4 | 16PP | C1A	6 Torres | T+4 | 16PP | C1A
Projeto Infra	EP	
Projeto Torre	EP	
Mês Base	abril-24	outubro-24
Incc	1.178,386	fevereiro-03
LVS	fevereiro-25	
Indiretos	fevereiro-25	
Base de Preço	LPU 89	
Takt	2x2	
Prazo (mês)	15 | 11	13 | 12

CUSTO TOTAL I	R$ / UND R$ 93.132	R$ / UND R$ 84.515	DIF R$ 8.616
INDIRETO	R$ 16.377	R$ 13.830	R$ 2.547
TORRE	R$ 42.428	R$ 43.144	-R$ 716
INFRA	R$ 20.228	R$ 16.658	R$ 3.570
FUNDAÇÃO	R$ 9.309	R$ 6.965	R$ 2.345
EEE	R$ 0	R$ 0	R$ 0
ETE	R$ 0	R$ 0	R$ 0
CONTENÇÃO	R$ 18	R$ 0	R$ 18
TERRAPLENAGEM	R$ 4.771	R$ 3.918	R$ 853
CUSTO TOTAL II	R$ 1.086	R$ 1.438	-R$ 352
VIÁRIO	R$ 278	R$ 267	R$ 10
DRENAGEM	R$ 0	R$ 0	R$ 0
EXTENSÃO DE REDE ELÉTRICA	R$ 217	R$ 141	R$ 76
EXTENSÃO DE REDE HIDRÁULICA	R$ 591	R$ 1.029	-R$ 438
CUSTO TOTAL III	R$ 0	R$ 0	R$ 0
INCORRIDOS	R$ 0	R$ 0	R$ 0
CUSTO TOTAL IV	R$ 0	R$ 0	R$ 0
APRENDIZADO	R$ 0	R$ 0	R$ 0
CUSTO TOTAL V	R$ 0	R$ 3.303	-R$ 3.303
ATUALIZAÇÃO POR INCC	R$ 0	R$ 3.303	-R$ 3.303
CUSTO TOTAL	R$ 94.218	R$ 89.256	R$ 4.961

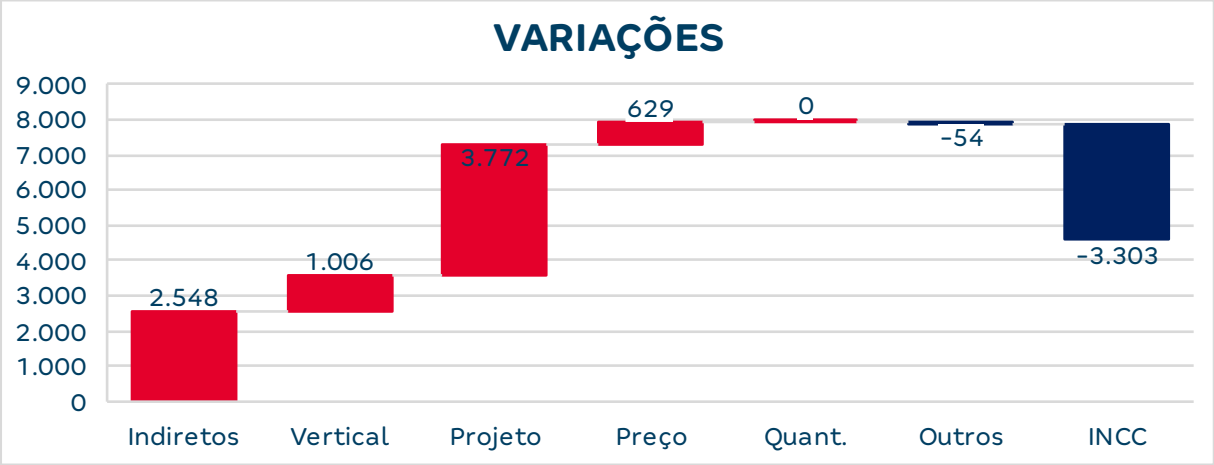

INDIRETOS
+ 60 | G17

VERTICAL
+ 1.006 | Retroalimentação

PROJETO
+ 290 | Estrutura (Concreto e Aço
+ 2.345 | Fundação
+ 853 | Terraplenagem
+ 267 | Vagas em U
+686 | Reservatório Metálico

PREÇO
+ 422 | Estrutura (Concreto e Aço)
+ 500 | Alvenaria de vedação
+ 200 | Esquadrias de Alumínio
- 438 | Cotação Extensão de rede hidráulica

OUTROS
- 54 | Inst. Infra e Torre

INCC
- 3.303 | Atualização INCC

Operações

SISTEMA DE ABASTECIMENTO DE ÁGUA
Execução de 61 m de extensão de rede em tubulação ø150 PVC Ocre para abastecimento de água.

SISTEMA DE ESGOTAMENTO SANITÁRIO
Execução de 125m de extensão de esgoto em tubulação ø160 PEAD

SISTEMA DE DRENAGEM
Descarte na rede pública em frente ao terreno.

SISTEMA DE ABASTECIMENTO DE GÁS
Abastecimento por GLP.

SISTEMA DE ABASTECIMENTO ELÉTRICO
Com viabilidade.

TERRENO

URBANIZAÇÃO
Considerado calçada na testada do empreendimento.

Operações

Matriz Risco Concessionária	
Água	Nível 3
Esgoto	Nível 3
Drenagem	Nível 3
Elétrica	Nível 3
Gás	NA
Urbanização	Nível 3

LEGENDA		
Nível	Tipo	Status
1	Com Diretriz	Conclusiva
2		Conclusiva com projeto aprovado
3		Conclusiva sem projeto aprovado
4		Não Conclusiva
5	Sem Diretriz	-
NA	-	Não aplicável

Água:
- Viabilidade emitida em 09/2024, com validade em 09/2026.

Esgoto:
- Viabilidade emitida em 08/2023, com validade em 08/2025. Viabilidade emitida para 500uh. Este estudo tem total de 690uh.

Drenagem:
- Considerado descarte por gravidade na sarjeta em rede pública na testada do terreno.

Elétrica:
- Viabilidade emitida em 10/2024.

Gás:
- Empreendimento com GLP.

Urbanização:
- Considerado calçada na testada do empreendimento.

Logística

EQUIPAMENTOS E MAQUINÁRIOS							
EQUIPAMENTO	QUANTIDADE	MOBILIZAÇÃO	DESMOBILIZAÇÃO	PRÉ FORMA	ESTRUTURA	ACABAMENTO	FASE
_TENDA_BETONEIRA (LOG)	VARIAVEL	-	-	TODO PERÍODO	TODO PERÍODO	-	FASE 01 E 02
_TENDA_BOMBA ESTACIONÁRIA PADRÃO (LOG)	VARIAVEL	-	-	-	TODO PERÍODO	-	01 E 02
_TENDA_BOMBA LANÇA (LOG)	VARIÁVEL	-	-	TODO PERÍODO	TODO PERÍODO	-	01 E 02

VIVÊNCIA - CONTAINERS							
DESCRIÇÃO	QUANTIDADE	MOBILIZAÇÃO	DESMOBILIZAÇÃO	PRÉ FORMA	ESTRUTURA	ACABAMENTO	FASE
_TENDA_CONTAINER PORTARIA (LOG)1	1 MÓDULO DE CONTAINER COM BANHEIRO	1 MOB	1 DESMOB	TODO PERÍODO	TODO PERÍODO	TODO PERÍODO	E 02
_TENDA_VIVÊNCIA MODULAR RS (LOG)							

TENDAS_PERÍODOS							
DESCRIÇÃO	QUANTIDADE	LARGURA	COMPRIMENTO	PRÉ FORMA	ESTRUTURA	ACABAMENTO	FASE
_TENDA_DESMOLDANTE (LOG)	1	2,50	4,00	-	TODO PERÍODO	-	01 E 02
_TENDA_INFLAMÁVEIS (LOG)	1	2,50	4,00	-	TODO PERÍODO	TODO PERÍODO	01 E 02
_TENDA_TENDA ACABAMENTO (LOG)	1	6,00	8,00	-	TODO PERÍODO	TODO PERÍODO	01 E 02
_TENDA_TENDA ARMADOR (LOG)	1	3,00	5,00	TODO PERÍODO	TODO PERÍODO	-	01 E 02
_TENDA_TENDA LAZER (LOG)	1	3,30	6,00	-	TODO PERÍODO	TODO PERÍODO	01 E 02
_TENDA_TENDA MOLDADOR (LOG)	1	2,50	4,00	TODO PERÍODO	TODO PERÍODO	-	01 E 02

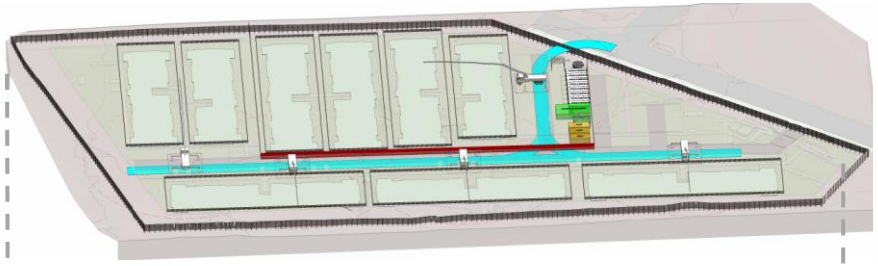

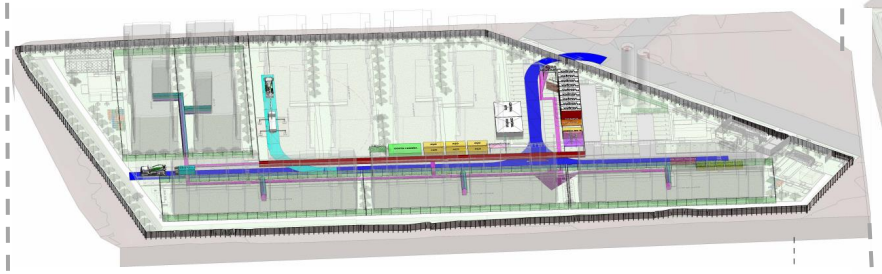

Logística

Solar do Bosque - RS

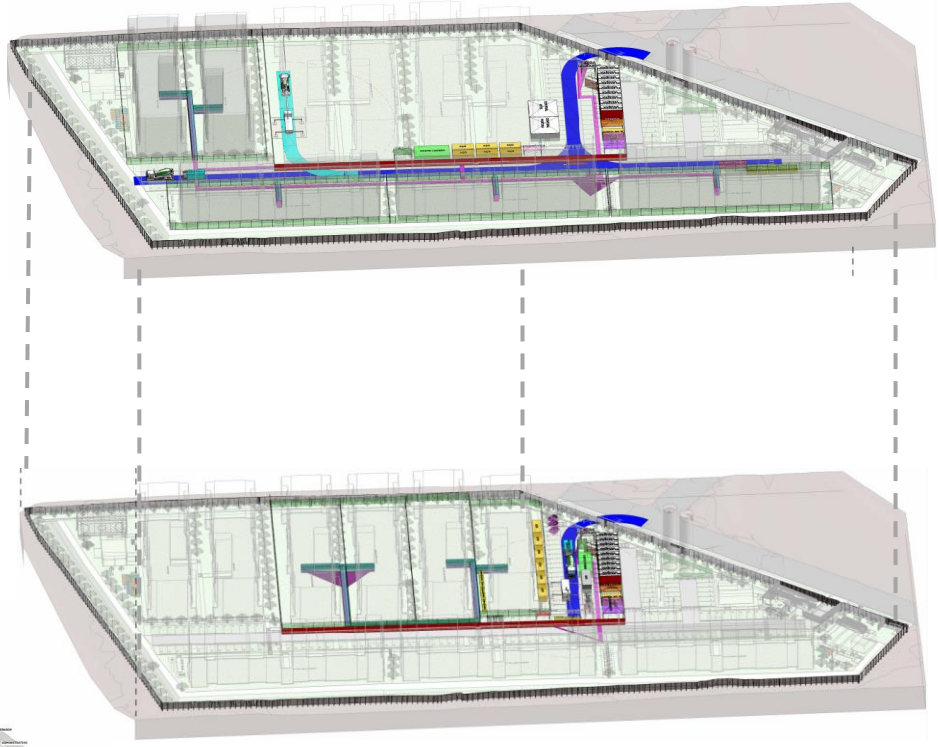

MODULAÇÃO E TOMBAMENTO
1 : 750

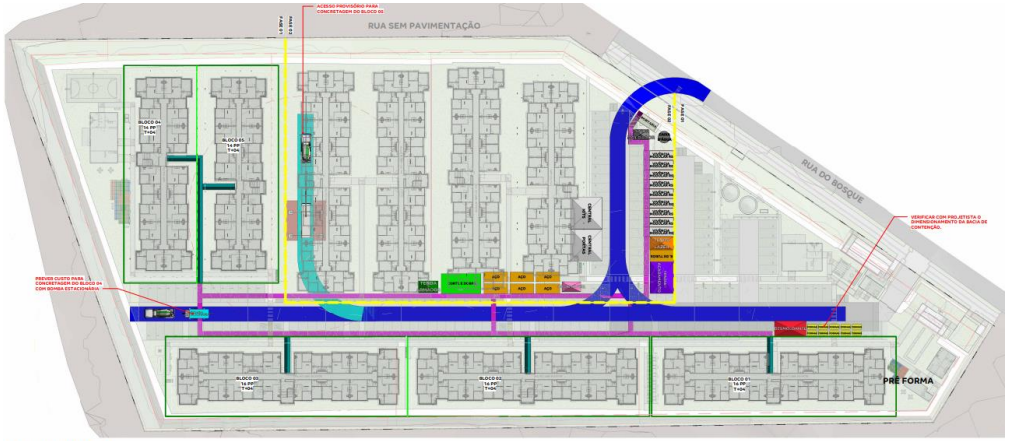

ESTRUTURA-FASE 01

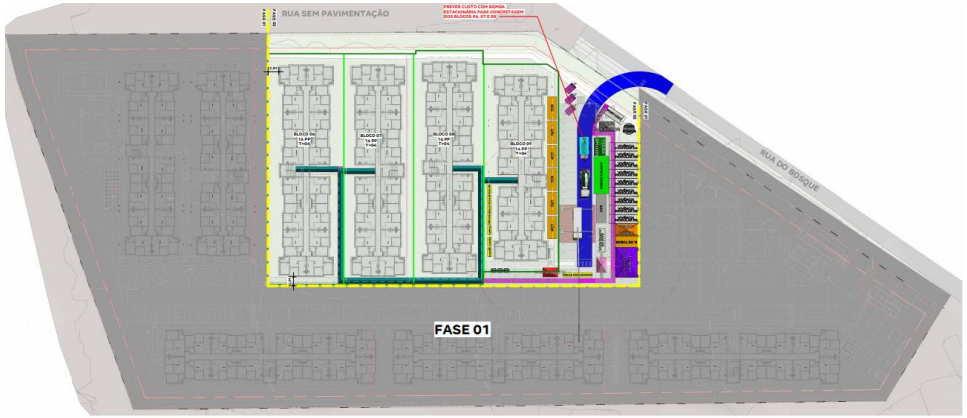

ESTRUTURA-FASE 02

Logística

ITENS A SEREM CONSIDERADOS:

- **CUSTOS** — PREVER CUSTO PARA PERDA DE CONCRETO DURANTE O PERÍODO DE FUNDAÇÃO E ESTRUTURA COM UTILIZAÇÃO DE BOMBA ESTACIONÁRIA PARA A CONCRETAGEM CONFORME INDICADO EM PROJETO, NECESSÁRIO DEVIDO À DISTÂNCIA ENTRE PONTO DE PATOLA E BLOCOS E AO GABARITO.
- **CUSTOS** — PREVER CUSTO PARA SECCIONAMENTO DOS RESERVATÓRIOS METÁLICOS (CASTELOS) EM DUAS PARTES, NÃO MAIORES QUE 20,00m CADA (GABARITO MÁXIMO DA CARRETA DE TRANSPORTE), PARA ACESSO DA CARRETA AO EMPREENDIMENTO. (VERIFICAR MEDIDAS EM NO PROJETO DE LOGISTICA)
- **NEGÓCIOS** — EXECUÇÃO DOS MÓDULOS I À IX OCORRERÁ DE FORMA CONCOMITANTE, SENDO QUE O MÓDULO I SERÁ EXECUTADO PELA PRIMEIRA EQUIPE E MÓDULO II PELA SEGUNDA EQUIPE.

C000 - TENDAS_PERÍODOS

DESCRIÇÃO	QUANTIDADE	PRÉ FORMA	ESTRUTURA	ACABAMENTO	FASE
_TENDA_DESMOLDANTE (LOG)	1	-	TODO PERÍODO	-	01 E 02
_TENDA_INFLAMÁVEIS (LOG)	1	-	TODO PERÍODO	TODO PERÍODO	01 E 02
_TENDA_TENDA ACABAMENTO (LOG)	1	-	TODO PERÍODO	TODO PERÍODO	01 E 02
_TENDA_TENDA ARMADOR (LOG)	1	TODO PERÍODO	TODO PERÍODO	-	01 E 02
_TENDA_TENDA CENTRAL DE KITS (LOG)	1	-	TODO PERÍODO	TODO PERÍODO	01 E 02
_TENDA_TENDA CENTRAL DE PORTAS (LOG)	1	-	TODO PERÍODO	TODO PERÍODO	01 E 02
_TENDA_TENDA LAZER (LOG)	1	-	TODO PERÍODO	TODO PERÍODO	01 E 02
_TENDA_TENDA MOLDADOR (LOG)	1	TODO PERÍODO	TODO PERÍODO	-	01 E 02

C000 - EQUIPAMENTOS E MAQUINÁRIOS

EQUIPAMENTO	QUANTITATIVO	PRÉ FORMA	ESTRUTURA	ACABAMENTO	FASE
_TENDA_BETONEIRA (LOG)	VARIÁVEL	TODO PERÍODO	TODO PERÍODO	-	01 E 02
_TENDA_BOMBA ESTACIONÁRIA PADRÃO (LOG)	1	-	TODO PERÍODO	-	01 E 02
_TENDA_BOMBA LANÇA (LOG)	VARIÁVEL	TODO PERÍODO	TODO PERÍODO	-	01 E 02

C000 - VIVÊNCIA - CONTAINERS

DESCRIÇÃO	QUANTIDADE DE CONTAINERS	MOBILIZAÇÃO	DESMOBILIZAÇÃO	PRÉ FORMA	ESTRUTURA	ACABAMENTO	FASE
_TENDA_CONTAINER ALMOXARIFADO (LOG)	1 MÓDULO	1 MOB	1 DESMOB	-	TODO PERÍODO	TODO PERÍODO	01 E 02
_TENDA_CONTAINER PORTARIA (LOG)	1 MÓDULO	1 MOB	1 DESMOB	TODO PERÍODO	TODO PERÍODO	TODO PERÍODO	01 E 02
_TENDA_CONTAINER PROVISÓRIO (LOG)	8 MÓDULOS (PERÍODO DE PRÉ FORMA)	1 MOB	1 DESMOB	TODO PERÍODO	-	-	FASE 01
_TENDA_CONTAINER VESTIÁRIO ACABAMENTO (LOG)	2 MÓDULOS	1 MOB	1 DESMOB	-	-	TODO PERÍODO	01 E 02
_TENDA_CONTAINER VESTIÁRIO ESTRUTURA (LOG)	2 MÓDULOS	1 MOB	1 DESMOB	-	TODO PERÍODO	-	01 E 02
_TENDA_CONTAINER VIVÊNCIA PADRÃO (LOG)	7 MÓDULOS PAV. TÉRREO, 7 MÓDULOS PAV. SUPERIOR (T+1)	1 MOB	1 DESMOB	-	TODO PERÍODO	TODO PERÍODO	01 E 02

Pareceres

Análise da Mancha e Implantação

Prospecção

Operações

Inteligência de Mercado

Financeiro

Anexos

Demanda e Distribuição da Mancha

Potencial de Demanda			Lançados		Lançados + Landbank	
Mancha	CÓD.	Shr.	ANO	MÊS	ANO	MÊS
Porto Alegre Norte + Alvorada	PZN	52%	1.481	123	1.778	148

Empreendimento	Renda	Lançamento	jun/25	jul/25	ago/25	set/25	out/25	nov/25	dez/25	jan/26	fev/26	mar/26	abr/26	mai/26	jun/26	jul/26	ago/26	set/26	out/26	nov/26	dez/26	jan/27	fev/27	mar/27
Quinta Do Lago - Bolsena	2.949	dez-24	25	25	25	25	1																	
Solar do Bosque F1	**2.468**	**jun-25**		**29**	**29**	**29**	**29**	**29**	**29**	**29**	**29**	**29**	**29**	**29**	**29**	**29**	**3**							
Solar do Bosque F2	**2.468**	**jul-26**															**24**	**24**	**24**	**24**	**24**	**24**	**24**	**24**
Monte Verde	2.859	out-25						26	26	26	26	26	26	26	26	26	26	26	26	26	26	26	26	26
Alto Da Colina F1	2.171	jan-26									25	25	25	25	25	25	25	25	25	25	25	25	25	23
Alto Da Colina F2	2.171	fev-27																						2
Total de Vendas Lançados			**25**	**25**	**25**	**25**	**1**	**0**	**0**	**0**	**0**	**0**	**0**	**0**	**0**	**0**	**0**	**0**	**0**	**0**	**0**	**0**	**0**	**0**
Total de Vendas Lançados + Landbank			**25**	**54**	**54**	**54**	**30**	**55**	**55**	**55**	**80**	**80**	**80**	**80**	**80**	**80**	**78**	**75**	**75**	**75**	**75**	**75**	**75**	**75**

Parecer de I.M sobre a mancha:

O projeto analisado em comitê está em linha com o potencial teórico de demanda calculado para a mancha. (Total Lançados)

Canibalização:

Sem Risco de Canibalização

Solar do Bosque F1 | Mapa Concorrência

		Solar do Bosque F1	Porto Versalhes
		TENDA	MRV - Com Emcash
	Distância Tenda (km)		2,39Km
Região 1 Km	População	12.655	16.238
	Dens. Demográfica	4.054	5.202
	Renda (R$)	4.078	4.729
	Classe Social	C1 (R$ 2.7k a 4.6k)	C2 (de R$ 1.5K a R$ 2.7K)
	PEA Dia	7.437	16.932
Quantitativo	Lançamento	jun/25	nov/24
	Unidades	380	220
	Estoque	380	86
	VSO	29	27
	Stockout	13	3
	Preço Nominal (R$)	198.966	218.400
	Preço CEF (R$)	163.543	171.060
	Renda Comprador (R$)	2.468	2.898
	Dif Tenda (R$)		-430
	Factibilidade		●
Qualitativo	Condomínios	1	1
	Torres	-	4
	Gabarito	T+4	T+4
	Plantas (m²)	36m²	38,4m² | 42,15m²
	Tipologia	2 Dorms	2 Dorms
	Opções	Não	Não
	Varanda	Não	Sim
	Suite	Não	Não
	Dif. Entrega	Não	Não
	Vagas	24% de Vagas	Com vaga
	Lazer	Chimarródromo, churrasqueira gourmet, playkids, playbaby, salão de festas com churrasqueira, administrativo, quadra gramada, fitness externo, bicicletários.	Churrasqueira, Espaço Piquenique, Playground.

Farol Renda
● Acima de 300
● Entre 0 e 300
● Abaixo de 0

Diagnóstico Concorrência

- O Porto Versalhes – MRV apresenta um preço acima do estimado para o Solar do Bosque. Mas, o projeto conta com a opção do Emcash.
- Embora o empreendimento da MRV ofereça a opção de Emcash e contenha o beneficio do cheque, o mesmo não incomodaria, porque já temos uma performance consolidada na região, como o projeto Parque Paris(Tenda). Além disso, o Solar do Bosque, em seu lançamento também contará com beneficio do cheque moradia que não está sendo contemplado nesse parecer, o que traz um conforto em relação a renda estimada pelo Vision.

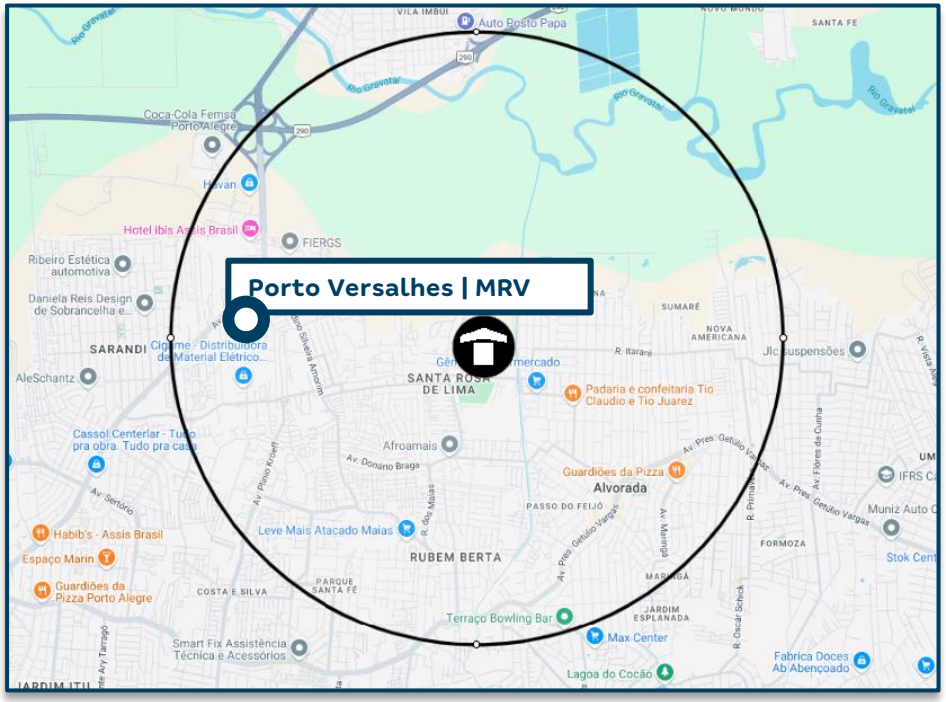

Simulação de Preço

Informações Viabilidade

Projeto:	Solar do Bosque F1			
Tipo:	**Sem vaga**		**Sem vaga**	
Método	**Ref - Parque Paris**		**Vision**	
Avaliação	215.000		215.000	
Renda Inicial (VF)	2.256		2.328	
Renda Final*	-		-	
% RET1	75%		75%	
Tipo:	**VF**	**R$**	**VF**	**R$**
Ato	0,41	923	0,44	1.033
FGTS	0,10	231	0,34	801
Financiamento	95,05%	130.235	95,80%	135.558
Subsídio	107,57%	31.765	93,53%	24.974
Prazo de Pró-soluto	20	20	20	20
Pró-Soluto	73,48%	12.047	76,80%	12.992
Preço Raso (RS)	175.200	175.200	175.358	175.358
TCD	91,43%	20.792	89,11%	20.911
VSO	22	22	22	22
Preço de Venda	**194.909**	**194.909**	**195.185**	**195.185**
Elasticidade	0,556%	0,556%	0,556%	0,556%
Preço de Venda Final	**195.991**	**195.991**	**196.269**	**196.269**
Preço Raso (R$)	**175.200**		**175.358**	
% de Raso	**89,39%**		**89,35%**	
BP25 - Não Inflacionado	**-**		**181.327**	
BP25 - Inflacionado	**-**		**184.388**	

Simulação de Preço

Informações Viabilidade

Projeto:	Solar do Bosque F1

Tipo:	Vaga Moto
Método	Vision
Avaliação	220.000
Renda Inicial (VF)	2.546
Renda Final*	-
% RET1	75%

Tipo:	VF	R$
Ato	0,44	1.116
FGTS	0,35	902
Financiamento	97,69%	145.578
Subsídio	96,45%	18.573
Prazo de Pró-soluto	20	20
Pró-Soluto	78,03%	14.440
Preço Raso (RS)	180.609	180.609
TCD	81,86%	21.011
VSO	1	1
Preço de Venda	**200.506**	**200.506**
Elasticidade	0,556%	0,556%
Preço de Venda Final	**201.620**	**201.620**
Preço Raso (R$)	**180.609**	
% de Raso	**89,58%**	
BP25 - Não Inflacionado	**A tipologia não foi aberta em BP**	
BP25 - Inflacionado		

O projeto **Parque Paris** não teve vendas de unidades com vaga moto.

Simulação de Preço

Informações Viabilidade

Projeto:	Solar do Bosque F1			
Tipo:	**Vaga Carro**		**Vaga Carro**	
Método	**Ref - Parque Paris**		**Vision**	
Avaliação	230.000		230.000	
Renda Inicial (VF)	2.998		2.958	
Renda Final*	-		-	
% RET1	50%		50%	
Tipo:	**VF**	**R$**	**VF**	**R$**
Ato	0,47	1.417	0,45	1.335
FGTS	0,33	1.002	0,31	913
Financiamento	97,94%	159.964	97,46%	157.720
Subsídio	112,68%	9.471	138,20%	12.637
Prazo de Pró-soluto	20	20	20	20
Pró-Soluto	71,91%	15.667	68,21%	14.661
Preço Raso (RS)	187.521	187.521	187.266	187.266
TCD	69,53%	21.011	70,47%	21.011
VSO	6	6	6	6
Preço de Venda	**207.380**	**207.380**	**207.127**	**207.127**
Elasticidade	0,556%	0,556%	0,556%	0,556%
Preço de Venda Final	**208.532**	**208.532**	**208.277**	**208.277**
Preço Raso (R$)	**187.521**		**187.266**	
% de Raso	**89,92%**		**89,91%**	
BP25 - Não Inflacionado	**-**		**186.322**	
BP25 - Inflacionado	**-**		**189.462**	

Análise de Preço

Informações Viabilidade

Projeto:	Solar do Bosque F1	
Tipo:	**Faixa 2**	
Método	**Vision**	
Avaliação	218.316	
Renda Inicial (VF)	2.468	
Renda Final*	-	
Tipo:	**VF**	**R$**
Ato	0,44	1.100
FGTS	0,34	828
Financiamento	96,21%	140.540
Subsídio	103,03%	22.175
Prazo de Pró-soluto	20	20
Pró-Soluto	75,03%	13.389
Preço Raso (RS)	178.031	178.031
TCD	84,96%	20.935
VSO	29	29
Preço de Venda	**197.861**	**197.861**
Elasticidade	0,556%	0,556%
Preço de Venda Final	**198.966**	**198.966**
Preço Raso (R$)	**178.031**	
% de Raso	**89,48%**	
Raso Todas as Fases	**179.501**	
Nominal Todas as Fases	**200.701**	

1

Análise de Riscos	Farol IM
IM avalia o Preço Vision como **factível**.	

1) I.M está de acordo com o preço Vision, visto que, os projetos da regional já capturaram a faixa de renda estimada no parecer.

Conforme apresentado no slide "Panorama de Concorrência", embora o empreendimento da MRV ofereça a opção de Emcash e contenha o beneficio do cheque, o mesmo não incomodaria, porque já temos uma performance consolidada na região, como o projeto Parque Paris (Tenda). Além disso, o Solar do Bosque, em seu lançamento também contará com beneficio do cheque moradia que não está sendo contemplado nesse parecer, o que traz um conforto em relação a renda estimada pelo Vision.

Dessa forma, entendemos que o preço proposto é adequado, considerando a performance dos projetos da regional.

	Preço Real					Preço Normalizado (20m)	
	Avaliação	Preço Raso	Renda Média	VSO	PSOL	Δ PSOL	Preço Raso
Quinta do Lago - Bolsena	**219.964**	**189.394**	**3.186**	**36**	**22**	**-1.716**	**187.678**
Solar do Bosque	**218.316**	**178.031**	**2.468**	**29**	**20**	**-**	**178.031**

Simulação de Preço – Fases Futuras

Vision

Nome Fase	Tipologia	Renda	Ato	FGTS	Cond.	Subsídio	PSOL	TCD	VSO	Nom. Pré	Avali.	Elast.	Nom. Pós	Raso Pós	PSOL (m)	RET1
Solar do Bosque F2	Vaga Carro	2.958	0,45	0,31	98,1%	138,2%	70,1%	72,4%	7	204.211	230.000	3,3333%	211.018	189.426	16	50%
Solar do Bosque F2	Vaga Moto	2.546	0,44	0,35	97,7%	96,5%	80,2%	84,1%	1	197.634	220.000	3,3333%	204.222	182.630	16	50%
Solar do Bosque F2	Sem vaga	2.328	0,44	0,34	95,8%	93,5%	78,9%	91,6%	16	192.601	215.000	3,3333%	199.021	177.533	16	75%

Entorno

Distâncias - Mobilidade

- Av. Assis Brasil - 3,4 km
- Av. Baltazar de O. Garcia – 3,1 km
- Av. Bernardino Silveira Pastoriza – 600 m
- Av. Francisco Silveira Bittencourt – 1,8 km

Raio 2,5 Km

- Centro de Alvorada
- Fiergs

Concorrência

Porto Versalhes (MRV) – 3,4 km

- Preço Cheio (UH mais barata): R$ 216.900
- Avaliação: R$ 208.000
- Renda: R$ 2.320
- Estoque: 168
- 40% Vaga de Estacionamento
- Diferenciais: chuveiro a gás, circuito fechado de TV para segurança.

Parecer: Acreditamos que o preço é POSSÍVEL com o VSO proposto. Entendemos que esse empreendimento atenderá a demanda orgânica da sua microrregião, suprindo o stockout que seria gerado pelo Quinta do Lago Bolsena.

Pareceres

Análise da Mancha e Implantação

Prospecção

Operações

Inteligência de Mercado

Financeiro

Anexos

Informações Gerais – Consolidado – APROVAÇÃO

Solar do Bosque - RS - Porto Alegre Capital

Datas e Prazos

	Compra	Lançamento	Início Obra	Término Obra	LÇTO até IO	IO até TO	Chaves	LÇTO até Chaves
Consolidado	nov-23							
Solar do Bosque F1 vaga carro		jun-25	dez-25	mar-27	6 meses	15 meses	jun-28	36 meses
Solar do Bosque F1 vaga moto		jun-25	dez-25	mar-27	6 meses	15 meses	jun-28	36 meses
Solar do Bosque F1 sem vaga		jun-25	dez-25	mar-27	6 meses	15 meses	jun-28	36 meses
Solar do Bosque F2 vaga carro		jul-26	jan-27	dez-27	6 meses	11 meses	jul-29	36 meses
Solar do Bosque F2 vaga moto		jul-26	jan-27	dez-27	6 meses	11 meses	jul-29	36 meses
Solar do Bosque F2 sem vaga		jul-26	jan-27	dez-27	6 meses	11 meses	jul-29	36 meses

Terreno e Incorridos

TOTAL (R$ + Perm.):	11,08 MM	**Incorrido Terreno:** 0,00 MM	**Área do Terreno (100%):**	19.075 m²	**Área Líquida do Terreno:** 19.075 m²
Cash:	0,00 MM		**Custo de terreno m²:**	580,8	**Custo de terreno m² Área Líquida:** 580,8
Permuta Financeira:	11,08 MM (8,00%)		**VaR 25 (R$ mil):**	0	**Fração Terreno/Terreno + Custo Obra (%VGV):** 8,0% / 54,9%
Permuta Física:	0,00 MM (0,00%)		**VaR 26 (R$ mil):**	0	**CA Máx/Proj.** 1,3 / 1,3
Ato / %VGV:	0,00 MM / 0,0%		**Incorrido de Construção:**	0,09 MM	**Incorridos de Incorporação:** 0,33 MM

Vendas

Fases	Nº Pavimentos	Preço Raso Unit.	Qtde	Preço Unit.	Aval. CEF	Cond. Parcela	% Pró-soluto	% TCD
Solar do Bosque F1 vaga carro	T+4	187.266	80	208.277	230.000	97,5%	68,2%	70,5%
Solar do Bosque F1 vaga moto	T+4	180.609	12	201.620	220.000	97,7%	78,0%	81,9%
Solar do Bosque F1 sem vaga	T+4	175.358	288	196.269	215.000	95,8%	76,8%	89,1%
Solar do Bosque F2 vaga carro	T+4	189.426	94	211.018	230.000	98,1%	70,1%	72,4%
Solar do Bosque F2 vaga moto	T+4	182.630	10	204.222	220.000	97,7%	80,2%	84,1%
Solar do Bosque F2 sem vaga	T+4	177.533	206	199.021	215.000	95,8%	78,9%	91,6%

Unidades Totais:	690	**Preço Médio:**	200.701	**Renda Média:**	2.494	**ITBI+Emol. Unit. Médio:**	1.110
Unidades Tenda:	690	**Avaliação Média:**	218.942	**Ato:**	1.105 (0,44 Salários)	**Custo do Ciclo Unit.:**	13.146
VSO:	27 Unidades	**VGV Total:**	138.483.418	**FGTS:**	832 (0,33 Salários)	**Preço Raso Médio:**	179.501
RET Médio:	1,9%	**VGV Tenda:**	138.483.418	**% em RET 1%:**	69%	**Adc. Tx. de Aceleração Médio:**	800

Construção

Custo Total Unit. | Corrigido:	94.218 | 93.849	**Eventuais:**	2,00%	**Área priv (m²):**	36,00	**Gape / Mês Unit.:**	11,08

Resultado

LI (R$):	**22.228.178**	**LI:**	**22,40%**	**Exposição de Caixa (R$):**	**9.468.229**	**Margem Bruta Econômica:**	**38,94%**
TIR:	**151,72%**	**LI Aprovação:**	**20,00%**	**Ger. Caixa 12 meses (R$):**	**(6.747.455)**	**Margem Bruta REF:**	**41,02%**
Exposição de Caixa:	**6,56%**	**Δ LI:**	**2,40%**	**Ger. Caixa 24 meses (R$):**	**6.039.531**	**Margem Rasa Econômica:**	**31,12%**
Payback Contingente (21 m):	**17 m/ (-4 m)**	**LI Marginal:**	**22,88%**	**Ger. Caixa Marginal (R$):**	**40.204.514**	**Margem Rasa REF:**	**34,06%**
Payback Consolidado:	**17 meses**					**Margem de Contribuição Econômica:**	**28,75%**

DRE – APROVAÇÃO

Solar do Bosque		Primeira Fase		Demais Fases	
Nominal	%	Nominal	%	Nominal	%
144.334	100,0%	76.770	100,0%	67.565	100,0%
(1.541)	1,1%	(806)	1,0%	(735)	1,1%
(87.184)	61,1%	(50.691)	66,7%	(36.493)	54,6%
(11.279)	7,9%	(6.008)	7,9%	(5.271)	7,9%
(1.186)	0,8%	(648)	0,9%	(537)	0,8%
(1.665)	1,2%	(887)	1,2%	(779)	1,2%
(73.054)	51,2%	(43.148)	56,8%	(29.907)	44,8%
55.609	38,9%	25.274	33,3%	30.336	45,4%
-	0,0%	-	0,0%	-	0,0%
55.609	38,9%	25.274	33,3%	30.336	45,4%
(11.239)	7,9%	(5.977)	7,9%	(5.262)	7,9%
(3.320)	2,3%	(1.766)	2,3%	(1.554)	2,3%
41.050	28,7%	17.530	23,1%	23.520	35,2%
(1.261)	0,9%	(659)	0,9%	(602)	0,9%
39.789	27,9%	16.871	22,2%	22.918	34,3%

Solar do Bosque		Primeira Fase		Demais Fases	
VP	%	VP	%	VP	%
99.234	100,0%	56.609	100,0%	42.625	100,0%
(1.042)	1,1%	(585)	1,0%	(457)	1,1%
(75.964)	76,6%	(46.264)	81,7%	(29.700)	69,7%
(7.625)	7,7%	(4.342)	7,7%	(3.283)	7,7%
(1.195)	1,2%	(654)	1,2%	(541)	1,3%
(1.449)	1,5%	(810)	1,4%	(639)	1,5%
(54.492)	54,9%	(34.012)	60,1%	(20.480)	48,0%
(9.089)	9,2%	(5.255)	9,3%	(3.834)	9,0%
(1.263)	1,3%	(713)	1,3%	(550)	1,3%
(853)	0,9%	(479)	0,8%	(374)	0,9%
22.228	22,4%	9.760	17,2%	12.468	29,3%
-		-		-	

Comparativo

Comparativo dos Estudos - Consolidado	BP - 2025	Atual	Atual vs BP - 2025	Δ%
Data Estudo:	setembro-24	abril-25	7 Meses	N/A
Lançamento:	julho-25	junho-25	-1 Meses	N/A
Uhs:	690	690	-	0,0%
Preço Nominal:	201.648	200.701	(948)	-0,5%
Preço Raso:	182.544	179.501	(3.043)	-1,7%
Preço Nominal Inflacionado:	221.651	212.093	(9.558)	-4,3%
Preço Raso Inflacionado:	200.677	189.709	(10.967)	-5,5%
Renda Média:	2.942	2.494	(448)	-15,2%
RET Médio:	1,3%	1,9%	0,6 p.p.	
% em RET 1%:	88,8%	68,7%	-20,1 p.p.	
VSO:	27	27	-	0,0%
ITBI/Emol. Inf (Unit)[2]:	1.681	1.987	306	18,2%
Avaliação:	196.698	218.942	22.244	11,3%
Prazo construção F1:	13	15	2	15,4%
Prazo de Pró-Soluto F1:	18	20	2	11,1%
Custo Total Inf (Unit):	127.386	126.354	(1.032)	-0,8%
Custo Construção (Unit):	85.953	94.218	8.265	9,6%
Custo Construção Corrigido:	85.953	93.849	7.896	9,2%
Fração de construção:	43%	46,8%	4,1 p.p.	9,7%
INCC Folha Rosto:	1.126,92	1.178,39	51	4,6%
Custo Terreno Inf:	12.073.856	11.278.836	(795.019)	-6,6%
Custo Relacionados a Terreno (Unit):	6.579	1.718	(4.861)	-73,9%
Fração do Terreno[1]:	8,0% / 50,6%	8,0% / 54,9%	0,0 p.p.	0,0%
Custo de Incorp. por uh:	1.010	2.413	1.403	138,9%
ITBI/Emol. Inf (Total)[2]:	1.160.224	1.371.244	211.020	18,2%
Custo do Ciclo (Unit):	13.207	13.146	(61)	-0,5%
Lucro Imobiliário:	25,4%	22,4%	-3,0 p.p.	-11,9%
LI Marginal:	25,7%	22,9%	-2,8 p.p.	-10,8%
Exposição de caixa:	8,7%	6,6%	-2,1 p.p.	-24,2%
TIR:	139,8%	151,7%	11,9 p.p.	8,5%
Margem Bruta REF:	43,1%	41,0%	-2,1 p.p.	
Margem Bruta Econômica:	41,3%	38,9%	-2,4 p.p.	-5,8%
Margem Rasa REF:	37,2%	34,1%	-3,1 p.p.	
Margem Rasa Econômica:	34,7%	31,1%	-3,6 p.p.	-10,3%
Margem Contribuição Econômica:	31,3%	28,7%	-2,5 p.p.	-8,1%
Payback Contingente (Régua 21 m):	15 m/ (-6 m)	17 m/ (-4 m)	2	13,3%
Payback Consolidado:	15 Meses	17 Meses	2 Meses	13,3%

[1] Valor do terreno contratual

[2] ITBI com taxa de Aceleração

Obrigado