Tenda

sua próxima conquista

Book de Lançamento

Regional: RS

Projeto: Solar do Bosque

Data Comitê: 30/06/2025

Comitê Presencial – 30.06.2025

Nome	Solar do Bosque - Lançamento	Observação - Solar do Bosque
Alexandre Regis de Oliveira	Aprovado	n/a
Renan Barbosa Sanches	Aprovado	ok
Alejandro Octavio Abiusi	Aprovado	ok
Amanda da Silva Bezerra	Aprovado	ok
Fabricio Quesiti Arrivabene	Aprovado	Ok
Rodrigo Osmo	Discutir em Comitê	(1) Gostaria de entender melhor a preocupaçao do ciclo com relação a VSO no voice over.
Andre Luis Menegazzo Padilha	Aprovado	ok
Luiz Mauricio de Garcia Paula	Discutir em Comitê	Entendi a aplicação da elasticidade, mas cabe um desafio de preço aqui?

Pergunta Rodrigo Osmo

- **Gostaria de entender melhor a preocupação do ciclo com relação a VSO no voice over.**

R: Trata-se de um produto Faixa 1, posicionado na mancha com maior potencial de vendas. O histórico de vendas na mancha, nos últimos 4 anos, é de 61 unidades/mês, e o produto em questão será o único Faixa 1, e com forte affordability em função do preço proposto e o perfil de renda disponível.

Além disso, já contabilizamos 35 propostas prévias (21 prontas para gerar), mesmo antes do lançamento oficial — o que demonstra forte aderência do mercado e reforça a viabilidade do volume proposto.

Pergunta Luiz Mauricio

➢ **Entendi a aplicação da elasticidade, mas cabe um desafio de preço aqui?**

R: Abaixo temos o comparativo dos preços praticados no Parque Paris com os preços propostos para o Solar do Bosque apresentado em comitê de lançamento.

	Parque Paris com cheque	Parque Paris sem cheque	Parque Paris sem cheque (elasticidade aplicada)	**Solar do Bosque**
Nominal (R$)	210.901	203.098	180.000	**190.646**
Raso (R$)	201.350	181.595	161.000	**171.068**
VSO	38	32	53	**53**

- Preço normalizado para pró-soluto de 23 meses;
- Período analisado de 07/24 a 09/24 para vendas sem cheques e 10/24 de vendas com cheque;

Na análise foi considerado o período de vendas do Parque Paris com e sem o subsídio e aplicação da elasticidade no cenário sem cheque para chegar ao VSO de 53 vendas. Nesse cenário, obteríamos um preço raso de R$161.000 e preço nominal de R$180.000, valores abaixo do adotado no comitê de lançamento do Solar do Bosque, com raso de R$171.069 e nominal de R$190.646.

Em caso de retorno dos cheques, há margem para desafio de preço. Porém para início de lançamento e considerando cenário sem subsídio estadual, vamos com preço que entrega os financials exigidos visando VSO de 53 vendas/mês.

Comitê Digital – 25.06.2025

	Nome	Solar do Bosque - Lançamento	Observação - Solar do Bosque
4	Alexandre Regis de Oliveira	Aprovado	n/a
5	Renan Barbosa Sanches	Aprovado	ok
6	Alejandro Octavio Abiusi	Aprovado	ok
7	Amanda da Silva Bezerra	Aprovado	ok
8	Fabricio Quesiti Arrivabene	Aprovado	Ok
9	Rodrigo Osmo	Discutir em Comitê	(1) Gostaria de entender melhor a preocupaçao do ciclo com relação a VSO no voice over.
0	Andre Luis Menegazzo Padilha	Aprovado	ok
1	Luiz Mauricio de Garcia Paula	Discutir em Comitê	Entendi a aplicação da elasticidade, mas cabe um desafio de preço aqui?

Observação Fabricio Arrivabene

- **Observação: Preocupação com VSO (proj. unificado), porém numa mancha que comporta com preço atrativo. Apenas como comparação, o Parque Paris fazia em média 35~40 vendas brutas/mês.**

R: Empreendimento com preço mais atrativo que Parque Paris e sendo o único produto da Zona Norte, dentro do trimestre, após stockout do Quinta do Lago Bolsena.

Pergunta Luiz Mauricio

- **Pergunta: Tivemos uma queda de preço (nominal e raso) relevante com relação a nossa expectativa no BP25 e na escritura (abril 25). O que justifica? (imagino que nenhuma dessas contava com o cheque)**

R: O empreendimento estava faseado tanto no BP quanto na escritura, com um VSO de 29 unidades. Com a unificação do projeto, o VSO aumentou para 53 unidades, o que, consequentemente, levou à redução do preço devido à aplicação da elasticidade negativa.
Ambos os cenários desconsideram o uso de cheque.

Abaixo temos o comparativo de preço BP x Comitê:

	BP Inflacionado	BP Partida	Comitê
Raso	186.462	180.260	171.068
Nominal	209.950	202.966	190.646
VSO	29	29	53

One Page – Solar do Bosque – Cenário Real & Aprovação

	Cidade	Porto Alegre	**Mancha de demanda**	RS - PZN - Porto Alegre Zona Norte
	Regional	RS	**Cluster MPR**	1 - Vermelho
	Cenário de Aprovação	Aprovação	**Tipo de Aprovação**	Consolidado
	Fase Anterior	N/A		
	Tipo de Comitê	Lançamento	**Versão da VF**	Versão 1.0: Jun
[1]	**Unidades (% Vagas)**	690 (32%)	**CA Máx | Proj**	1,3 | 1,3
	Tipologia	F2 - Concreto	**Escritura**	jun-25
	Fases	1 fases	**Lçto | Duração (m)**	jun/25 | 24
[2]	**Valor Líquido do Terreno (% VGV)**	10.524 (8,0%)	**Un. Perm. Fís (% Ter)**	0 (0,0%)
	Cash (Correção)	0 (N.A.)	**%VGV Perm Fin Líquida (% Ter)**	8,0% (100,0%)
	Valor R$/m²	552	**VAR (%VGV)**	000 (0,0%)
[3]	**Custo Construção (%VGV)**	65.694 (49,9%)	**Indireto Unit.**	13.666
	Prazo da Obra (meses)	18	**Torre Unit.**	43.215
	Custo Total Unit. | Corrigido (LPU):	95.208 | 94.662 (91)	**Infra Unit.**	19.579
	Início de Obra	dez-25	**Fundação Unit.**	13.491
[4]	**Preço Nominal Unit.**	190.646	**VSO**	53
	Preço Raso Unit.	171.068	**Referência**	Vision
	Avaliação Unit.	201.649	**Renda (% em RET 1%)**	2.494 (92,9%)
	Fase de Lançamento - Uso exclusivo para o Ciclo Financeiro		**Preço Raso Inf. Médio Unit.**	173.970
	Preço Inf. Médio Unit.	193.864	**Margem Bruta REF (%)**	37,2%
	Custo Inf. Médio Unit.	121.687	**Margem Rasa REF (%)**	30,1%

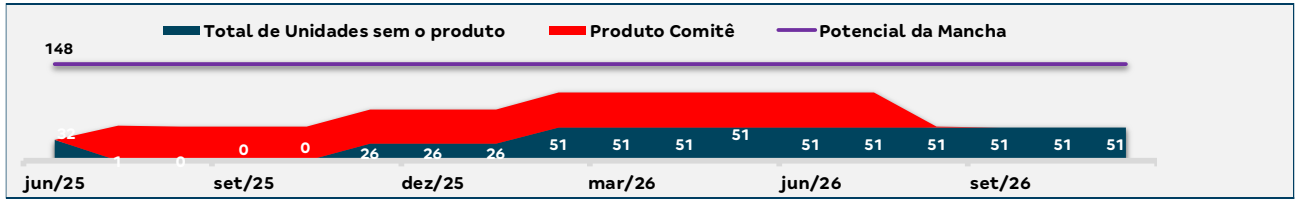

[5]	**LI (Régua):**	**20,0% (20,0%)**	**Margem Bruta Econômica:**	35,5%
	LI Marginal:	21,1%	**Margem Rasa Econômica:**	27,3%
	Margem Bruta REF:	37,2%	**Margem Contribuição Econômica:**	25,3%
	Margem Rasa REF:	**30,1%**	**Exposição (% VGV):**	10.669 (8,1%)
	TIR:	164,9%	**VGV Total:**	131.546
	Payback Contingente (21 m) :	**16 m/ (-5 m)**	**Ger. Caixa 12 meses (R$):**	(9.420)
	Payback Consolidado:	16	**Ger. Caixa 24 meses (R$):**	21.009

***Valores em R$ 1000**

Destaques

Cenário aprovação igual cenário Real – Folga de Início de 6 meses e VSO na Regra de Ouro de 13 meses.

[1] Terreno localizado no município de **Porto Alegre**, em Santa Rosa de Lima, sequencia do empreendimento Parque Paris (mesmo bairro), em stockout desde dezembro/24. Empreendimento em fase única com **690 unidades na tipologia T+4 modular.**

[2] Negócio **100% em permuta financeira (8,0% do VGV)**, com valor estimado de R$ 10,6MM

- Não há VGV mínimo estabelecido para este negócio;
- Quitação do saldo de permuta financeira em 48 meses após escritura, com desconto de 25%;

Escritura outorgada em jun/25
Corretagem: R$ 296.000 (2,8% do Preço Terreno) pagos em 5 parcelas.

[3] Custo da obra consolidada em 95.208/uh.

Presença de estruturas enterradas (atualmente em demolição) utilizou-se a solução de estaca raiz para 4 blocos projetados nas regiões afetadas (custo de fundações elevado de 13,4k/uh considerado). Ao término da demolição (previsto para 30/06) será reavaliada a solução de fundações e, sendo possível a reversão total para estaca hélice contínua, a economia potencial é de aproximadamente 2,74MM (-3,977k/uh)

[4] Preço de venda **desconsidera o subsídio estadual (20k/uh).**

Primeiro empreendimento da Regional RS com vaga de moto vinculada a unidade e torre modular T+4. Avaliação da vaga de moto pela CEF em 4.000.

VSO de 53 vendas/mês – unificação de fases (projeto originalmente faseado – 380/310) – permite ser o projeto mais barato da PZN entre toda a concorrência.

[5] Entrega acima dos Financials mínimos exigidos.

PORTO ALEGRE – ZONA NORTE

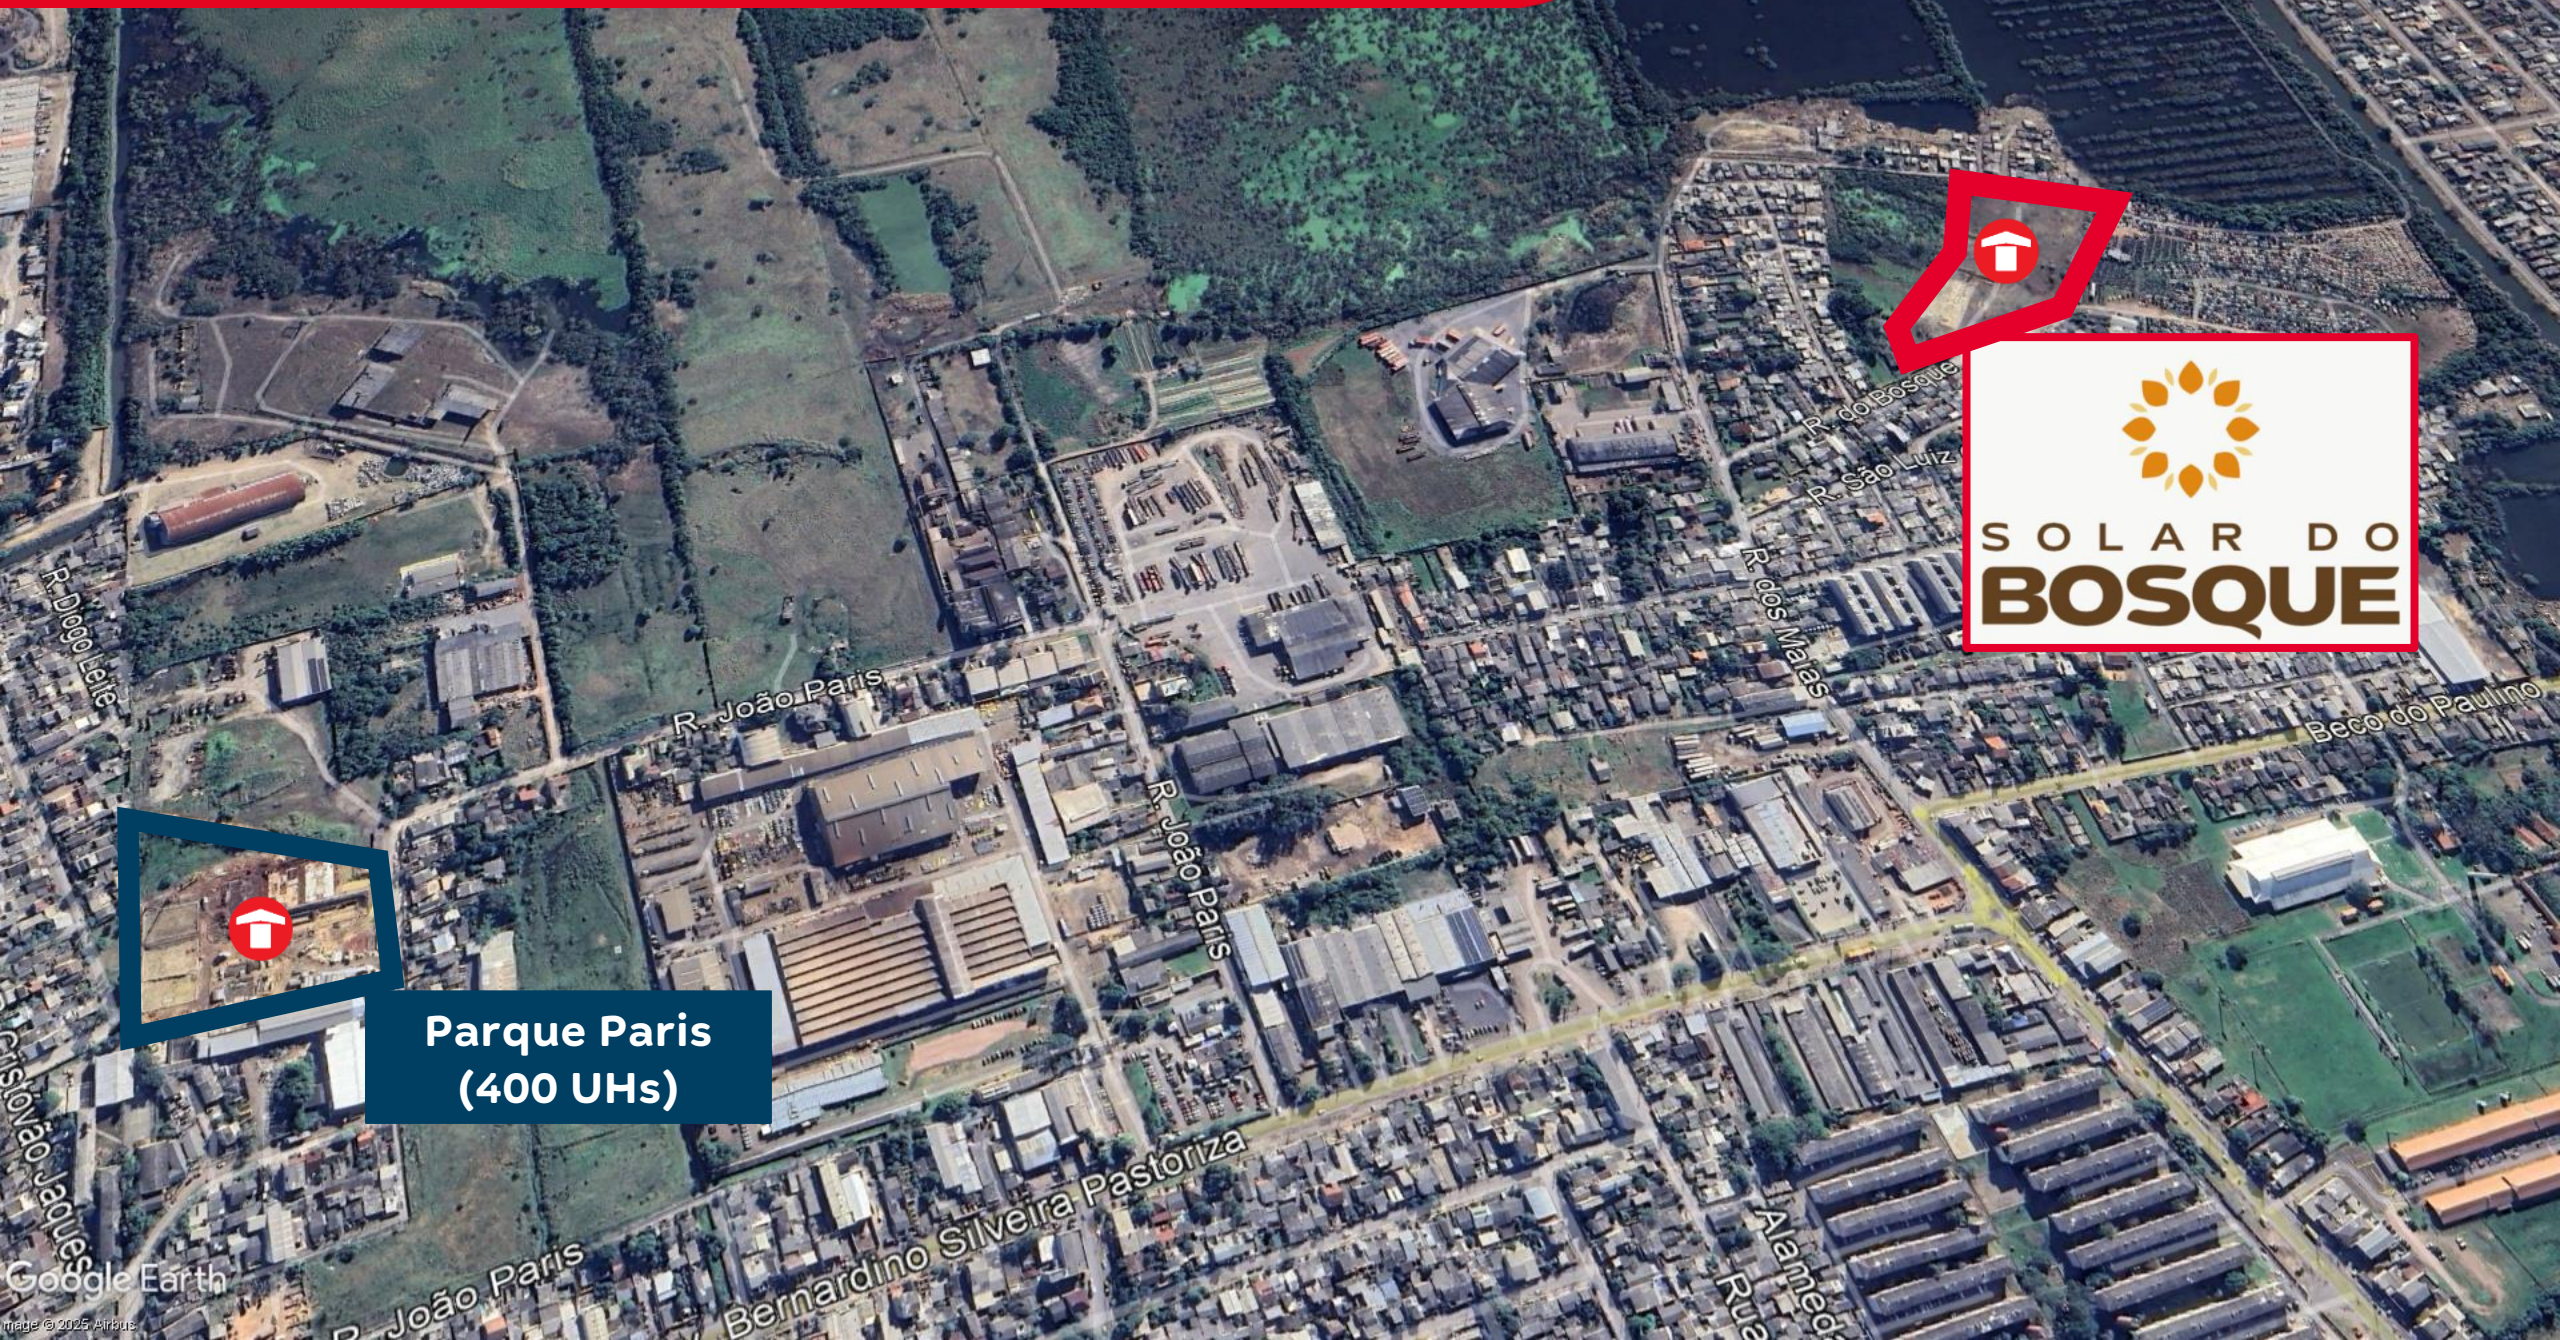

- Pareceres
- Análise da Mancha e Implantação
- Operações
- Inteligência de Mercado
- Financeiro

Pareceres

Área	Riscos Associados	Parecer	Criticidade
Jurídico	Escritura de Venda e Compra - lavratura até 16/06 e registro até 30/06. Registro da Incorporação - até 30/06. Averbação do Patrimônio de Afetação - até 30/06.	Ok com ressalvas	
Legalização	Processo de emissão do Termo de Anuência Prévia em tramitação na Metroplan.	OK	
Produto	Não há riscos associados	OK	
Custos	Considerando fundação raíz, para o Bloco 2 (integralmente), Bloco 7,8 e 9(parcial). Quantitativos concreto e aço Torre e Lajão conforme AP	Ok com ressalvas	
GETEC	Em função de estruturas enterradas no terrenos sugerido seguir com estacas raíz para Bloco 2, 7, 8 e 9.	Ok com ressalvas	
Logística	Não há riscos associados	OK	
Contratação	Laudo de Engenharia em andamento previsto para 30/06 com pendência de RI e sem pendência em 07/07, risco previsto para 07/07 e retorno da análise jurídica em 09/07 (considerando RI em 30/06)	Ok com ressalvas	
Inteligência de mercado	IM avalia o Preço Vision como factível	OK	
Comercial/Ciclo	Acreditamos que o preço é POSSÍVEL com o VSO proposto. Entendemos que esse empreendimento atenderá a demanda orgânica da sua microrregião, suprindo o stockout que seria gerado pelo Quinta do Lago Bolsena.	OK	
Estudos Econômicos	Ok, sem riscos.	Ok	

Pareceres

Análise da Mancha e Implantação

Operações

Inteligência de Mercado

Financeiro

Mancha de Demanda

MANCHAS DE DEMANDA

- PZN – Porto Alegre Norte + Alvorada

Lançamento

1. Quinta do Lago

LandBank

2. Monte Verde
3. Quintana Parque
4. Estância do Sol
5. Solar do Bosque
6. Dallaesquina
7. Gran Boulevard
8. Alto da Encosta
9. Alvorecer Village
10. Sonata

Cluster MPR – (Comitê)

- Cluster 1 - Vermelho

Região

Borda

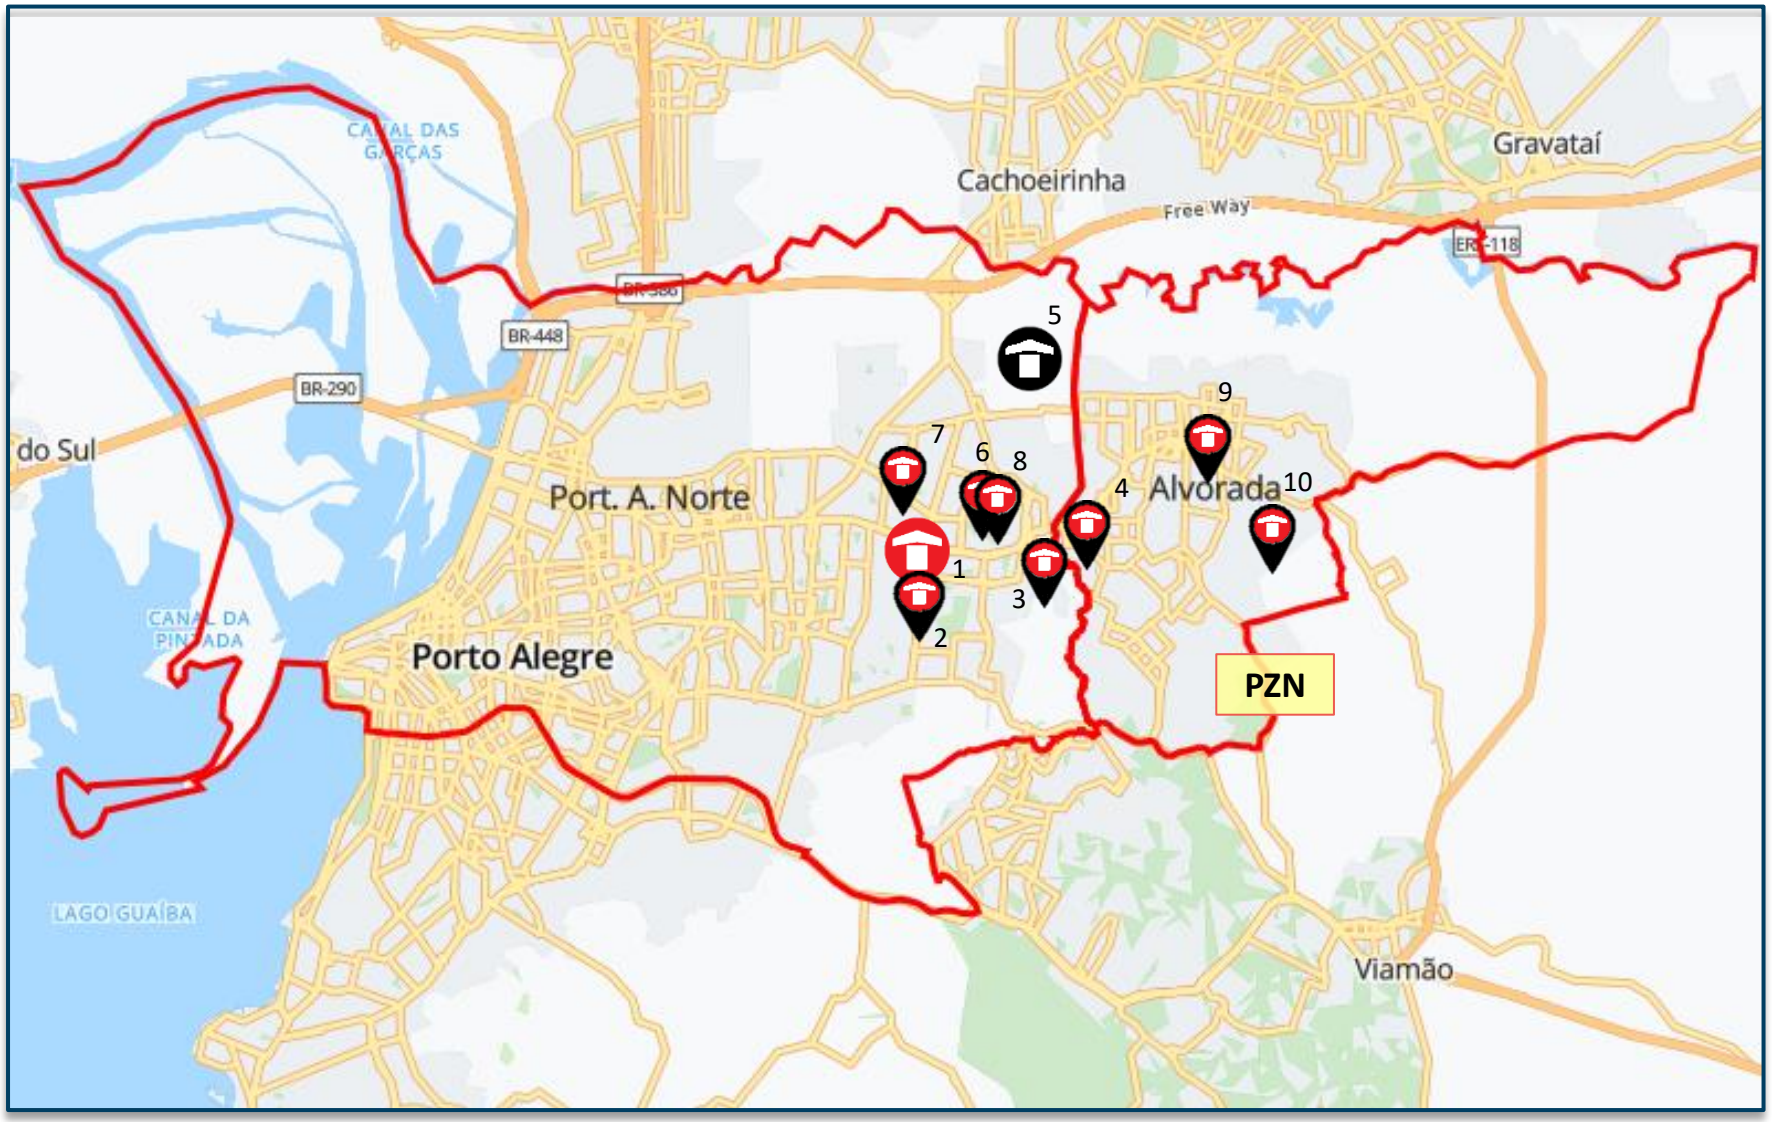

Lançados *LandBank* *Comitê*

PRODUTO

Empreendimento Solar do Bosque
Descritivo - Lançamento

Informações Gerais		
Terreno	Área terreno	19.074,66 m²
	Menor poligonal	19.074,66 m²
	App/fna	Não | Não
	Reserva de calçada/ melhoramento víario	Não | Não
	Área liquida	19.074,66 m²
	Zoneamento	MZ 03 UEU 10 QTR 001 - Zona de ocupação intensiva
	Ca máximo	1,30
	Ca projetado	1,30
	Gabarito máximo	18 m (T+05)
Geral	Total uh	690
	Total de vagas	225 (32,60%) sendo 174 comuns, 04 PCD, 03 visitantes e 43 vagas de moto
Tipologia	Tipologia	F002-IS2 FLEX
	Gabarito	T+04
	Lâmina	14pp | 16pp
	Área privativa	35,44m² | 35,64m² | 35,90m² | 35,72m²
	Varanda	N/A
Condomínio	Unidade pcd	21 – exigência de 2%
	Unidade lazer | técnica	00 | 00
	Torre	09
	Fase	Fase Única: 690 uhs
Lazer	Lazer externo	1 - Salão de Festas, 2 - Play Baby, 3 - Churrasqueira Gourmet, 4 - Chimarródromo, 5 - Espaço Relax, 6 - Play Kids, 7 - Fitness Externo, 8 - Quadra Gramada, 9 - Play Pet.
	Lazer interno	N/A

Lazeres Externos :

1. Salão de Festas
2. Play Baby
3. Churrasqueira Gourmet
4. Chimarródromo
5. Espaço Relax
6. Play Kids
7. Fitness Externo
8. Quadra Gramada
9. Play Pet

PRODUTO

Empreendimento Solar do Bosque
Atributos de produto - Lançamento

	Descrição	Criticidade	Parecer
Usabilidade	**Acesso Empreendimento**		
	Percurso do pedestre até torre		
Diferencial produto	**Prime**	Não	
	Supercondomínio	Não	
	Atributos Infra	Sim	10 lazeres externos, sendo: 02 Salões de Festas, 01 Play Baby, 01 Churrasqueira Gourmet, 01 Chimarródromo, 01 Espaço Relax, 01 Play Kids, 01 Fitness Externo, 01 Quadra Gramada, 01 Play Pet.
	Atributos Torre	Sim	Nova fachada
	Edifício Garagem	Não	

	Riscos associados	Parecer	Criticidade
Produto	Não há riscos associados	ok	

Play Kids

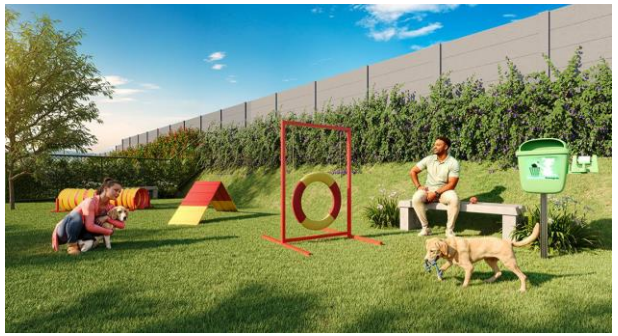
Play Pet

Quadra Gramada

Espaço Relax

Empreendimento Solar do Bosque
Modulação - Lançamento

Fase Única: 690uh (sendo 21 U.R.) – 225 vagas (sendo 04 PCD e 43 de moto)				
Módulo	**Blocos**	**UH**	**Vagas**	**Parecer**
Módulo 01	02 Blocos (16PP T+04)	160 UH (sendo 6 PCD)	89 vagas (sendo 2 PCD, 1 carga e descarga e 9 de moto)	Dos lazeres, estão contemplados no módulo 01 o chimarródromo, salão de festas, play baby e churrasqueira gourmet. Os demais lazeres não estão contemplados neste módulo e, portanto, é necessária a inclusão dessa informação no RI e material de vendas.
Módulo 02	01 Bloco (16PP T+04)	80 UH (sendo 3 PCD)	41 vagas (sendo 2 PCD e 3 de moto)	Dos lazeres, estão contemplados no módulo 02 o fitness externo.
Módulo 03	02 Blocos (14PP T+04)	140 UH (sendo 4 PCD)	00 vagas	Dos lazeres, estão contemplados no módulo 03 o play kids, play pet, salão de festas com churrasqueira e quadra descoberta.
Módulo 04	02 Blocos (16PP T+04)	160 UH (sendo 4 PCD)	20 vagas de moto	-
Módulo 05	01 Bloco (16PP T+04) e 01 Bloco (14PP T+04)	150 UH (sendo 4 PCD)	75 vagas (sendo 11 de moto)	-

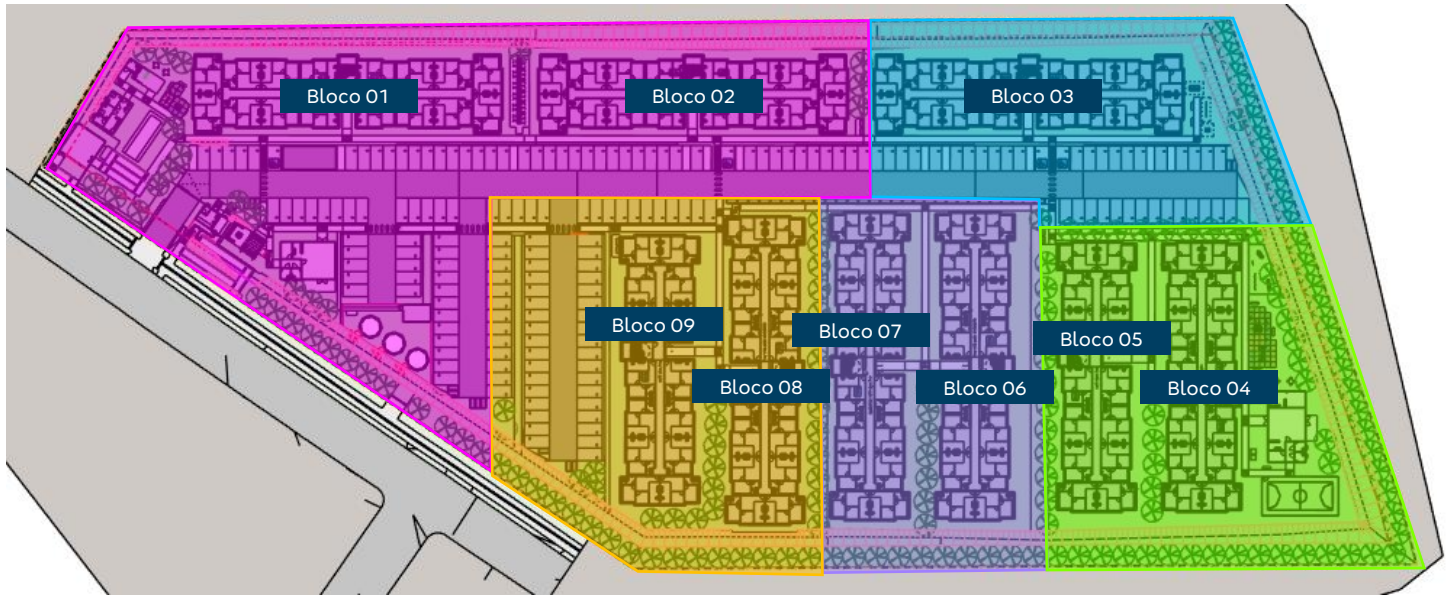

- Pareceres
- Análise da Mancha e Implantação
- Operações
- Inteligência de Mercado
- Financeiro

Custo de Construção

	SOLAR DO BOSQUE - UNIFICADO R03	SOLAR DO BOSQUE - UNIFICADO ESCRITURA	SOLAR DO BOSQUE - CONSOLIDADO BP25	MORADA DE CAMPO II LVS (ABRIL/25)
Torres	9	9	9	27
Unidades Construídas	690	690	690	540
Unidades Vendidas	690	690	690	540
Condomínios (qta.)	1	1	1	2
Cidade	Porto Alegre - RS	Porto Alegre - RS	Porto Alegre - RS	Porto Alegre - RS
Produto / Selo	F2 MODULAR	F2 MODULAR	F2 MODULAR	F2 -RS-A-5.0
Tipologia	3 Torres | T+4 | 14PP | C1A	3 Torres | T+4 | 14PP | C1A	3 Torres | T+4 | 14PP | C1A	13 Torre | T+4 | 08PP |
Tipologia	6 Torres | T+4 | 16PP | C1A	6 Torres | T+4 | 16PP | C1A	6 Torres | T+4 | 16PP | C1A	1 Torre | T+4 | 04PP |
Projeto Infra	EP	EP		PE
Projeto Torre	EP	EP		LO
Mês Base	junho-25	abril-25	outubro-24	
Incc	1191,327	1.178,386	1.134,775	
LVS	abril-25	fevereiro-25		
Indiretos	abril-25	fevereiro-25		
Base de Preço	LPU 91	LPU 89		
Takt	2x2	2x2		2x2
Prazo (mês)	18	18	17	15
CUSTO TOTAL I	R$ / UND R$ 94.660	R$ / UND R$ 90.045	R$ / UND R$ 84.515	R$ / UND R$ 84.253
Indireto	R$ 13.666	R$ 13.785	R$ 13.830	R$ 14.093
Torre	R$ 43.215	R$ 42.237	R$ 43.144	R$ 40.032
Infra	R$ 19.579	R$ 19.924	R$ 16.658	R$ 20.227
Fundação	R$ 13.491	R$ 9.309	R$ 6.965	R$ 6.114
EEE				R$ 225
ETE				
Contenção	R$ 18	R$ 18		R$ 189
Terraplenagem	R$ 4.692	R$ 4.771	R$ 3.918	R$ 3.373
CUSTO TOTAL II	R$ 548	R$ 1.086	R$ 1.438	R$ 4.721
Urbanização	R$ 95	R$ 278	R$ 267	R$ 2.204
Drenagem				
Extensão de Rede Elétrica	R$ 43	R$ 217	R$ 141	
Extensão de Rede Hidráulica	R$ 409	R$ 591	R$ 1.029	R$ 2.517
CUSTO TOTAL III				R$ 438
Incorridos				R$ 438
CUSTO TOTAL IV				
Aprendizado				
CUSTO TOTAL V		R$ 1.001	R$ 4.284	
Atualização por INCC		R$ 1.001	R$ 4.284	
CUSTO TOTAL I+II	R$ 95.208	R$ 91.131	R$ 85.953	R$ 88.974
CUSTO TOTAL I AO IV	**R$ 95.208**	**R$ 92.132**	**R$ 90.237**	**R$ 89.412**

Custo de Construção

	SOLAR DO BOSQUE - UNIFICADO R03	SOLAR DO BOSQUE - UNIFICADO ESCRITURA	
Torres	9	9	
Unidades Construídas	690	690	
Unidades Vendidas	690	690	
Condomínios (qta.)	1	1	
Cidade	Porto Alegre - RS	Porto Alegre - RS	
Produto / Selo	F2 MODULAR	F2 MODULAR	
Tipologia	3 Torres | T+4 | 14PP | C1A	3 Torres | T+4 | 14PP | C1A	
Tipologia	6 Torres | T+4 | 16PP | C1A	6 Torres | T+4 | 16PP | C1A	
Projeto Infra	EP	EP	
Projeto Torre	EP	EP	
Mês Base	junho-25	abril-25	
Incc	1191,327	1178,386	
LVS	abril-25	fevereiro-25	
Indiretos	abril-25	fevereiro-25	
Base de Preço	LPU 89	LPU 89	
Takt	2x2	2x2	
Prazo (mês)	18	18	
CUSTO TOTAL I	R$ / UND R$ 94.660	R$ / UND R$ 90.045	DIF R$ 4.615
INDIRETO	R$ 13.666	R$ 13.785	-R$ 119
TORRE	R$ 43.215	R$ 42.237	R$ 977
INFRA	R$ 19.579	R$ 19.924	-R$ 345
FUNDAÇÃO	R$ 13.491	R$ 9.309	R$ 4.181
EEE	R$ 0	R$ 0	R$ 0
ETE	R$ 0	R$ 0	R$ 0
CONTENÇÃO	R$ 18	R$ 18	R$ 0
TERRAPLENAGEM	R$ 4.692	R$ 4.771	-R$ 79
CUSTO TOTAL II	R$ 548	R$ 1.086	-R$ 538
VIÁRIO	R$ 95	R$ 278	-R$ 183
DRENAGEM	R$ 0	R$ 0	R$ 0
EXTENSÃO DE REDE ELÉTRICA	R$ 43	R$ 217	-R$ 174
EXTENSÃO DE REDE HIDRÁULICA	R$ 409	R$ 591	-R$ 182
CUSTO TOTAL III	R$ 0	R$ 0	R$ 0
INCORRIDOS	R$ 0	R$ 0	R$ 0
CUSTO TOTAL IV	R$ 0	R$ 0	R$ 0
APRENDIZADO	R$ 0	R$ 0	R$ 0
CUSTO TOTAL V	R$ 0	R$ 1.001	-R$ 1.001
ATUALIZAÇÃO POR INCC	R$ 0	R$ 1.001	-R$ 1.001
CUSTO TOTAL	R$ 95.208	R$ 92.132	R$ 3.076

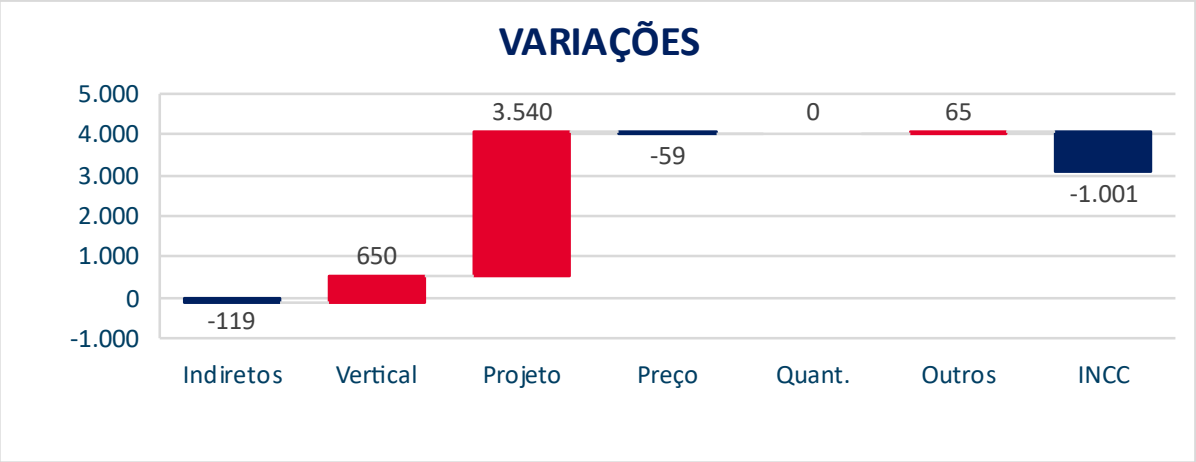

INDIRETOS
-49 |Implantação canteiro
-42 | Grupo 11
-27 | Equipamentos

VERTICAL
+650 | Retroalimentação

PROJETO
4181| Fundação (raiz)
- 562| Reservatório metálico
-79 | Terraplanagem

PREÇO
+ 124 | Enterrados

OUTROS
+ 515 | Inst. Torre
+89 | Inst. Infra
-538 | Infra Externa

INCC
- 1001 | Atualização INCC

Operações

SISTEMA DE ABASTECIMENTO DE ÁGUA
Execução de 61 m de extensão de rede em tubulação ø150 PVC Ocre para abastecimento de água.

SISTEMA DE ESGOTAMENTO SANITÁRIO
Execução de 125m de extensão de esgoto em tubulação ø160 PEAD

SISTEMA DE DRENAGEM
Descarte na rede pública em frente ao terreno.

SISTEMA DE ABASTECIMENTO DE GÁS
Abastecimento por GLP.

SISTEMA DE ABASTECIMENTO ELÉTRICO
Com viabilidade.

TERRENO

URBANIZAÇÃO
Considerado calçada na testada do empreendimento.

Operações

Matriz Risco Concessionária	
Água	Nível 3
Esgoto	Nível 3
Drenagem	Nível 3
Elétrica	Nível 3
Gás	NA
Urbanização	Nível 3

LEGENDA		
Nível	Tipo	Status
1	Com Diretriz	Conclusiva
2		Conclusiva com projeto aprovado
3		Conclusiva sem projeto aprovado
4		Não Conclusiva
5	Sem Diretriz	-
NA	-	Não aplicável

Água:
- Viabilidade emitida em 09/2024, com validade em 09/2026.

Esgoto:
- Viabilidade emitida em 08/2023, com validade em 08/2025. Viabilidade emitida para 500uh. Este estudo tem total de 690uh.

Drenagem:
- Considerado descarte por gravidade na sarjeta em rede pública na testada do terreno.

Elétrica:
- Viabilidade emitida em 10/2024.

Gás:
- Empreendimento com GLP.

Urbanização:
- Considerado calçada na testada do empreendimento.

Logística

EQUIPAMENTOS E MAQUINÁRIOS							
EQUIPAMENTO	QUANTIDADE	MOBILIZAÇÃO	DESMOBILIZAÇÃO	PRÉ FORMA	ESTRUTURA	ACABAMENTO	FASE
_TENDA_BETONEIRA (LOG)	VARIAVEL	-	-	TODO PERÍODO	TODO PERÍODO	-	FASE 01 E 02
_TENDA_BOMBA ESTACIONÁRIA PADRÃO (LOG)	VARIAVEL	-	-	-	TODO PERÍODO	-	01 E 02
_TENDA_BOMBA LANÇA (LOG)	VARIÁVEL	-	-	TODO PERÍODO	TODO PERÍODO	-	01 E 02

VIVÊNCIA - CONTAINERS							
DESCRIÇÃO	QUANTIDADE	MOBILIZAÇÃO	DESMOBILIZAÇÃO	PRÉ FORMA	ESTRUTURA	ACABAMENTO	FASE
_TENDA_CONTAINER PORTARIA (LOG)1	1 MÓDULO DE CONTAINER COM BANHEIRO	1 MOB	1 DESMOB	TODO PERÍODO	TODO PERÍODO	TODO PERÍODO	E 02
_TENDA_VIVÊNCIA MODULAR RS (LOG)							

TENDAS_PERÍODOS							
DESCRIÇÃO	QUANTIDADE	LARGURA	COMPRIMENTO	PRÉ FORMA	ESTRUTURA	ACABAMENTO	FASE
_TENDA_DESMOLDANTE (LOG)	1	2,50	4,00	-	TODO PERÍODO	-	01 E 02
_TENDA_INFLAMÁVEIS (LOG)	1	2,50	4,00	-	TODO PERÍODO	TODO PERÍODO	01 E 02
_TENDA_TENDA ACABAMENTO (LOG)	1	6,00	8,00	-	TODO PERÍODO	TODO PERÍODO	01 E 02
_TENDA_TENDA ARMADOR (LOG)	1	3,00	5,00	TODO PERÍODO	TODO PERÍODO	-	01 E 02
_TENDA_TENDA LAZER (LOG)	1	3,30	6,00	-	TODO PERÍODO	TODO PERÍODO	01 E 02
_TENDA_TENDA MOLDADOR (LOG)	1	2,50	4,00	TODO PERÍODO	TODO PERÍODO	-	01 E 02

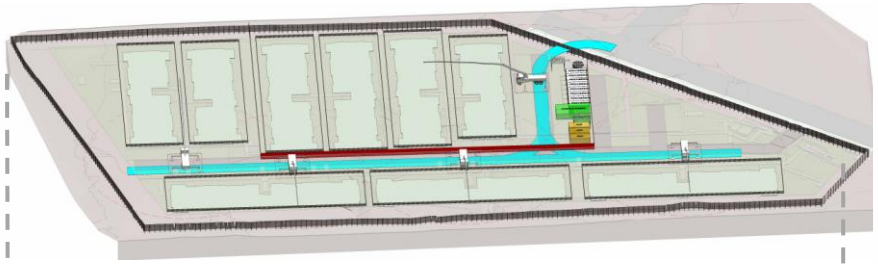

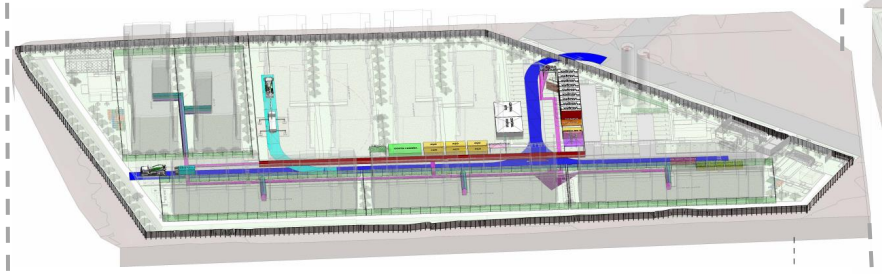

Logística

Solar do Bosque - RS

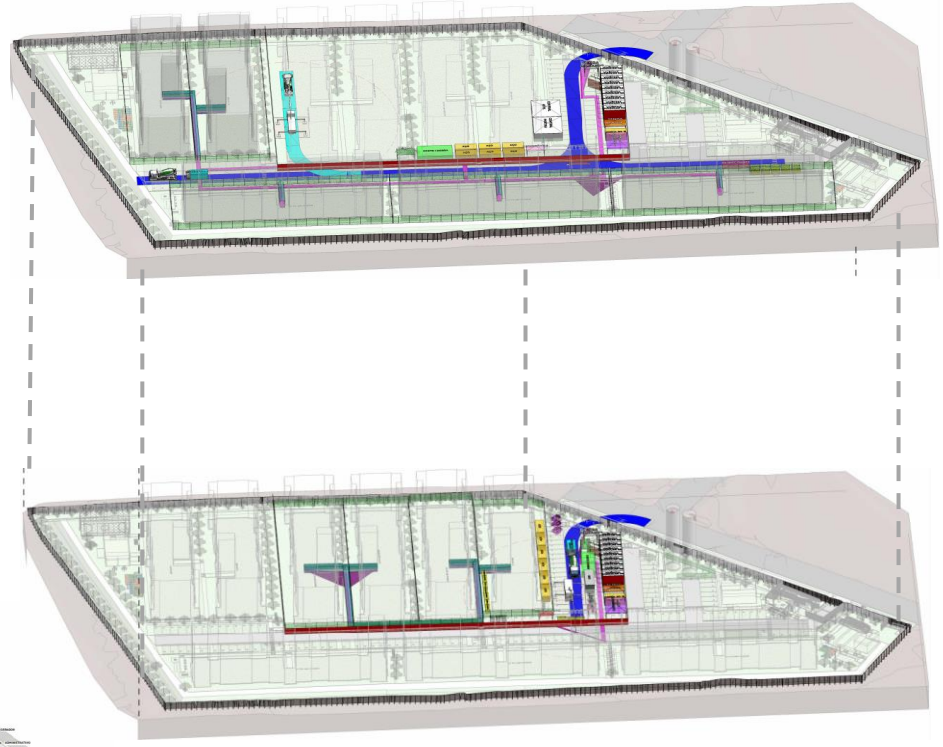

ESTRUTURA-FASE 01

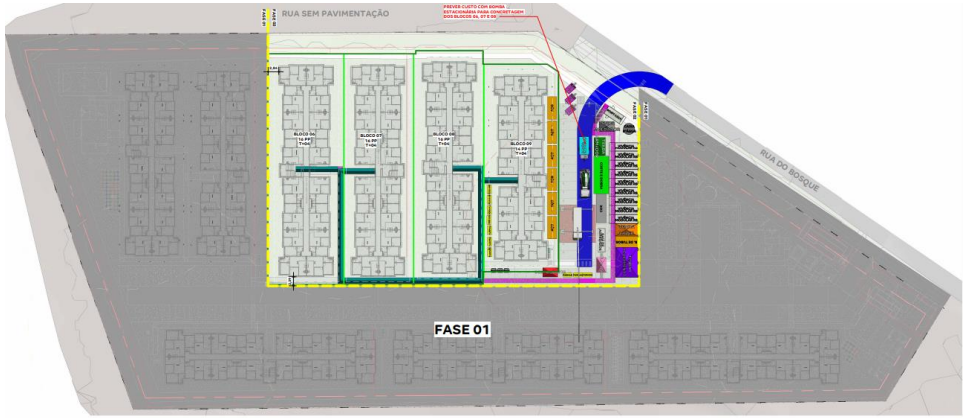

ESTRUTURA-FASE 02

MODULAÇÃO E TOMBAMENTO
1 : 750

Logística

ITENS A SEREM CONSIDERADOS:

- **CUSTOS** — PREVER CUSTO PARA PERDA DE CONCRETO DURANTE O PERÍODO DE FUNDAÇÃO E ESTRUTURA COM UTILIZAÇÃO DE BOMBA ESTACIONÁRIA PARA A CONCRETAGEM CONFORME INDICADO EM PROJETO, NECESSÁRIO DEVIDO À DISTÂNCIA ENTRE PONTO DE PATOLA E BLOCOS E AO GABARITO.
- **CUSTOS** — PREVER CUSTO PARA SECCIONAMENTO DOS RESERVATÓRIOS METÁLICOS (CASTELOS) EM DUAS PARTES, NÃO MAIORES QUE 20,00m CADA (GABARITO MÁXIMO DA CARRETA DE TRANSPORTE), PARA ACESSO DA CARRETA AO EMPREENDIMENTO. (VERIFICAR MEDIDAS EM NO PROJETO DE LOGISTICA)
- **NEGÓCIOS** — EXECUÇÃO DOS MÓDULOS I À IX OCORRERÁ DE FORMA CONCOMITANTE, SENDO QUE O MÓDULO I SERÁ EXECUTADO PELA PRIMEIRA EQUIPE E MÓDULO II PELA SEGUNDA EQUIPE.

C000 - TENDAS_PERÍODOS

DESCRIÇÃO	QUANTIDADE	PRÉ FORMA	ESTRUTURA	ACABAMENTO	FASE
_TENDA_DESMOLDANTE (LOG)	1	-	TODO PERÍODO	-	01 E 02
_TENDA_INFLAMÁVEIS (LOG)	1	-	TODO PERÍODO	TODO PERÍODO	01 E 02
_TENDA_TENDA ACABAMENTO (LOG)	1	-	TODO PERÍODO	TODO PERÍODO	01 E 02
_TENDA_TENDA ARMADOR (LOG)	1	TODO PERÍODO	TODO PERÍODO	-	01 E 02
_TENDA_TENDA CENTRAL DE KITS (LOG)	1	-	TODO PERÍODO	TODO PERÍODO	01 E 02
_TENDA_TENDA CENTRAL DE PORTAS (LOG)	1	-	TODO PERÍODO	TODO PERÍODO	01 E 02
_TENDA_TENDA LAZER (LOG)	1	-	TODO PERÍODO	TODO PERÍODO	01 E 02
_TENDA_TENDA MOLDADOR (LOG)	1	TODO PERÍODO	TODO PERÍODO	-	01 E 02

C000 - EQUIPAMENTOS E MAQUINÁRIOS

EQUIPAMENTO	QUANTITATIVO	PRÉ FORMA	ESTRUTURA	ACABAMENTO	FASE
_TENDA_BETONEIRA (LOG)	VARIÁVEL	TODO PERÍODO	TODO PERÍODO	-	01 E 02
_TENDA_BOMBA ESTACIONÁRIA PADRÃO (LOG)	1	-	TODO PERÍODO	-	01 E 02
_TENDA_BOMBA LANÇA (LOG)	VARIÁVEL	TODO PERÍODO	TODO PERÍODO	-	01 E 02

C000 - VIVÊNCIA - CONTAINERS

DESCRIÇÃO	QUANTIDADE DE CONTAINERS	MOBILIZAÇÃO	DESMOBILIZAÇÃO	PRÉ FORMA	ESTRUTURA	ACABAMENTO	FASE
_TENDA_CONTAINER ALMOXARIFADO (LOG)	1 MÓDULO	1 MOB	1 DESMOB	-	TODO PERÍODO	TODO PERÍODO	01 E 02
_TENDA_CONTAINER PORTARIA (LOG)	1 MÓDULO	1 MOB	1 DESMOB	TODO PERÍODO	TODO PERÍODO	TODO PERÍODO	01 E 02
_TENDA_CONTAINER PROVISÓRIO (LOG)	8 MÓDULOS (PERÍODO DE PRÉ FORMA)	1 MOB	1 DESMOB	TODO PERÍODO	-	-	FASE 01
_TENDA_CONTAINER VESTIÁRIO ACABAMENTO (LOG)	2 MÓDULOS	1 MOB	1 DESMOB	-	-	TODO PERÍODO	01 E 02
_TENDA_CONTAINER VESTIÁRIO ESTRUTURA (LOG)	2 MÓDULOS	1 MOB	1 DESMOB	-	TODO PERÍODO	-	01 E 02
_TENDA_CONTAINER VIVÊNCIA PADRÃO (LOG)	7 MÓDULOS PAV. TÉRREO, 7 MÓDULOS PAV. SUPERIOR (T+1)	1 MOB	1 DESMOB	-	TODO PERÍODO	TODO PERÍODO	01 E 02

PCP-165

Empreendimento	Lançto.	Unidades	# jogos	Equipes de forma	Início Obra	Início Forma 1	Início Forma 2	Início Forma 3	Término Forma 1	Término Forma 2	Término Forma 3	Previsão AGI
Parque Paris	set/23	400	2	A	29/03/24	06/08/24	19/09/24		07/01/25	14/01/25		jul/25
Morada do Campo I - F2	jan/24	180	2	B	23/09/24	09/11/24	15/11/24		13/01/25	18/01/25		jun/25
Quinta do Lago - F3 | Cond 02 Garda	fev/24	300	2	B	19/09/24	14/01/25	19/01/25		12/04/25	21/04/25		jul/25
Acqua Sena - F2	fev/24	220	2	A	09/11/24	08/01/25	15/01/25		17/03/25	21/03/25		ago/25
Ipanema Residence - F2	jun/24	240	2	A	02/01/25	18/03/25	22/03/25		29/05/25	03/06/25		out/25
Morada do Campo II	ago/24	540	2	B	28/12/24	13/04/25	22/04/25		16/09/25	04/10/25		mar/26
Morada Serena	nov/24	500	2	A	24/02/25	30/05/25	04/06/25		04/11/25	09/11/25		abr/26
Quinta do Lago - F4 | Cond 04 Bolsena	dez/24	251	2	B	30/04/25	17/09/25	05/10/25		05/12/25	23/12/25		set/26
Acqua Danúbio - F1	jan/25	388	2	A	23/06/25	05/11/25	10/11/25		08/03/26	13/03/26		dez/26
Acqua Danúbio - F2	dez/25	209	2	A	27/11/25	09/03/26	14/03/26		14/05/26	19/05/26		jan/27
Parque Ventura III F1	mai/25	440	2	B	21/07/25	06/12/25	24/12/25		25/04/26	13/05/26		fev/27
Solar do Bosque - F1+F2	jun/25	690	2	B	30/12/25	26/04/26	14/05/26		30/11/26	18/12/26		mai/27
Reserva das Figueiras F1	ago/25	260	2	A	31/12/25	15/05/26	20/05/26		06/08/26	11/08/26		jan/27

Pareceres

Análise da Mancha e Implantação

Operações

Inteligência de Mercado

Financeiro

Demanda e Distribuição da Mancha

Potencial de Demanda			Lançados		Lançados + Landbank	
Mancha	CÓD.	Shr.	ANO	MÊS	ANO	MÊS
Porto Alegre Norte + Alvorada	PZN	52%	1.481	123	1.778	148

Empreendimento	Renda	Lançamento	jun/25	jul/25	ago/25	set/25	out/25	nov/25	dez/25	jan/26	fev/26	mar/26	abr/26	mai/26	jun/26	jul/26	ago/26	set/26	out/26	nov/26	dez/26	jan/27	fev/27	mar/27
Quinta Do Lago - Bolsena	3.056	dez-24	32	1																				
Solar do Bosque	**2.123**	**jun-25**		**53**	**53**	**53**	**53**	**53**	**53**	**53**	**53**	**53**	**53**	**53**	**53**	**53**	**1**							
Monte Verde	2.859	out-25						26	26	26	26	26	26	26	26	26	26	26	26	26	26	26	26	26
Alto Da Colina F1	2.171	jan-26									25	25	25	25	25	25	25	25	25	25	25	25	25	23
Alto Da Colina F2	2.171	fev-27																						2
Total de Vendas Lançados			**32**	**54**	**53**	**53**	**53**	**53**	**53**	**53**	**53**	**53**	**53**	**53**	**53**	**53**	**1**	**0**	**0**	**0**	**0**	**0**	**0**	**0**
Total de Vendas Lançados + Landbank			**32**	**54**	**53**	**53**	**53**	**79**	**79**	**79**	**104**	**104**	**104**	**104**	**104**	**104**	**52**	**51**	**51**	**51**	**51**	**51**	**51**	**51**

Parecer de I.M sobre a mancha:

O projeto analisado em comitê está em linha com o potencial teórico de demanda calculado para a mancha. (Total Lançados)

Canibalização:

Sem Risco de Canibalização

Solar do Bosque | Mapa Concorrência

		Solar do Bosque	Porto Versalhes
		TENDA	MRV - Com Emcash
	Distância Tenda (km)		2,39Km
Região 1 Km	População	12.655	16.238
	Dens. Demográfica	4.054	5.202
	Renda (R$)	4.078	4.729
	Classe Social	C1 (R$ 2.7k a 4.6k)	C2 (de R$ 1.5K a R$ 2.7K)
	PEA Dia	7.437	16.932
Quantitativo	Lançamento	jun/25	nov/24
	Unidades	690	220
	Estoque	690	73
	VSO	53	21
	Stockout	13	3
	Preço Nominal (R$)	190.646	218.400
	Preço CEF (R$)	155.557	171.060
	Renda Comprador (R$)	2.123	2.898
	Dif Tenda (R$)		-774
	Factibilidade		●
Qualitativo	Condomínios	1	1
	Torres	-	4
	Gabarito	T+4	T+4
	Plantas (m²)	36m²	38,4m² | 42,15m²
	Tipologia	2 Dorms	2 Dorms
	Opções	Não	Não
	Varanda	Não	Sim
	Suite	Não	Não
	Dif. Entrega	Não	Não
	Vagas	28% de Vagas	Com vaga
	Lazer	Chimarródromo, churrasqueira gourmet, playkids, playbaby, salão de festas com churrasqueira, administrativo, quadra gramada, fitness externo, bicicletários.	Churrasqueira, Espaço Piquenique, Playground.

Farol Renda
● Acima de 300
● Entre 0 e 300
● Abaixo de 0

Diagnóstico Concorrência

- O Porto Versalhes – MRV apresenta um preço acima do estimado para o Solar do Bosque. Mas, o projeto conta com a opção do Emcash.
- Embora o empreendimento da MRV ofereça a opção de Emcash e contenha o beneficio do cheque, o mesmo não incomodaria, porque já temos uma performance consolidada na região, como o projeto Parque Paris(Tenda).

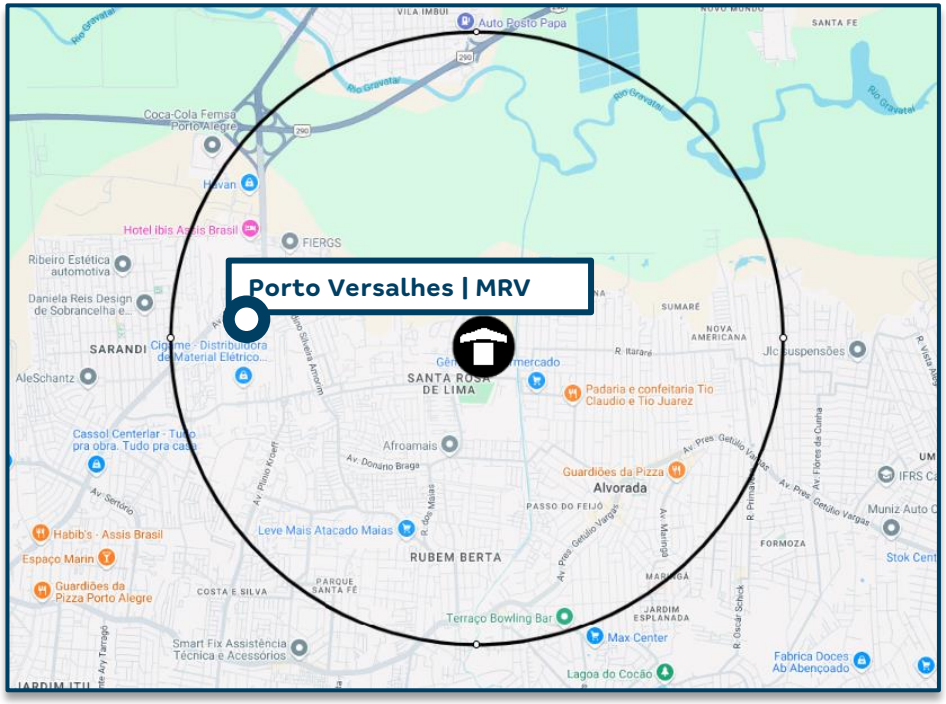

Simulação de Preço

Informações Viabilidade

Projeto:	Solar do Bosque			
Tipo:	**Sem vaga**		**Sem vaga**	
Método	**Ref - Parque París**		**Vision**	
Avaliação	199.000		199.000	
Renda Inicial (VF)	2.308		2.328	
Renda Final*	0		2.000	
% RET1	100%		100%	
Tipo:	**VF**	**R$**	**VF**	**R$**
Ato	0,39	856	0,44	966
FGTS	0,18	392	0,34	749
Financiamento	93,75%	123.914	96,75%	129.004
Subsídio	109,35%	28.167	93,22%	23.350
Prazo de Pró-soluto	23	23	23	23
Pró-Soluto	72,19%	13.926	71,80%	13.969
Preço Raso (RS)	167.256	167.256	168.038	168.038
TCD	79,84%	18.576	83,32%	19.551
VSO	38	38	38	38
Preço de Venda	**197.658**	**197.658**	**199.527**	**199.527**
Elasticidade	-5,983%	-5,983%	-5,983%	-5,983%
Preço de Venda Final	**185.832**	**185.832**	**187.589**	**187.589**
Preço Raso (R$)	**167.256**		**168.038**	
% de Raso	**90,00%**		**89,58%**	
BP25 - Não Inflacionado	**-**		**172.662**	
BP25 - Inflacionado	**-**		**178.482**	

Simulação de Preço

Informações Viabilidade

Projeto:	Solar do Bosque

Tipo:	Vaga moto
Método	Vision
Avaliação	203.000
Renda Inicial (VF)	2.546
Renda Final*	2.246
% RET1	75%

Tipo:	VF	R$
Ato	0,44	1.043
FGTS	0,35	843
Financiamento	95,84%	138.372
Subsídio	96,42%	17.365
Prazo de Pró-soluto	23	23
Pró-Soluto	72,96%	15.526
Preço Raso (RS)	173.150	173.150
TCD	76,53%	19.645
VSO	2	2
Preço de Venda	**205.064**	**205.064**
Elasticidade	-5,983%	-5,983%
Preço de Venda Final	**192.796**	**192.796**
Preço Raso (R$)	**173.150**	
% de Raso	**89,81%**	
BP25 - Não Inflacionado	-	
BP25 - Inflacionado	-	

O projeto **Parque Paris** não teve vendas de unidades com vaga moto.

Simulação de Preço

Informações Viabilidade

Projeto:	Solar do Bosque			
Tipo:	**Vaga Carro**		**Vaga Carro**	
Método	**Ref - Parque París**		**Vision**	
Avaliação	209.000		209.000	
Renda Inicial (VF)	2.998		2.958	
Renda Final*	0		2.458	
% RET1	100%		75%	
Tipo:	**VF**	**R$**	**VF**	**R$**
Ato	0,47	1.325	0,45	1.249
FGTS	0,33	937	0,31	854
Financiamento	97,48%	151.822	96,68%	149.724
Subsídio	112,54%	8.855	138,02%	11.815
Prazo de Pró-soluto	23	23	23	23
Pró-Soluto	67,24%	16.845	63,77%	15.764
Preço Raso (RS)	179.785	179.785	179.406	179.406
TCD	65,01%	19.645	65,89%	19.645
VSO	13	13	13	13
Preço de Venda	**212.121**	**212.121**	**211.718**	**211.718**
Elasticidade	-5,983%	-5,983%	-5,983%	-5,983%
Preço de Venda Final	**199.430**	**199.430**	**199.051**	**199.051**
Preço Raso (R$)	**179.785**		**179.406**	
% de Raso	**90,15%**		**90,13%**	
BP25 - Não Inflacionado	**-**		**177.727**	
BP25 - Inflacionado	**-**		**183.697**	

Análise de Preço

Informações Viabilidade

Projeto:	Solar do Bosque
Tipo:	**Faixa 2**
Método	**Vision**
Avaliação	201.649
Renda Inicial (VF)	2.494
Renda Final*	2.123

Tipo:	VF	R$
Ato	0,44	1.040
FGTS	0,33	779
Financiamento	96,70%	134.528
Subsídio	104,62%	20.250
Prazo de Pró-soluto	23	23
Pró-Soluto	69,82%	14.471
Preço Raso (RS)	171.068	171.068
TCD	78,70%	19.578
VSO	53	53
Preço de Venda	**202.052**	**202.052**
Elasticidade	-5,983%	-5,983%
Preço de Venda Final	**190.646**	**190.646**
Preço Raso (R$)	**171.068**	
% de Raso	**89,73%**	
Raso Todas as Fases	**171.068**	
Nominal Todas as Fases	**190.646**	

1

Análise de Riscos	Farol IM
IM avalia o Preço Vision como **factível**.	

1) I.M está de acordo com o preço Vision, visto que, os projetos da regional já capturaram a faixa de renda estimada no parecer.

Conforme apresentado no slide "Panorama de Concorrência", embora o empreendimento da MRV ofereça a opção de Emcash e contenha o beneficio do cheque, o mesmo não incomodaria, porque já temos uma performance consolidada na região, como o projeto Parque Paris (Tenda).

Abaixo segue o escalonamento da Regional:

	Preço Real					Preço Normalizado(23m)	
	Avaliação	Preço Raso	Renda Média	VSO	PSOL	Δ PSOL	Preço Raso
Quinta do Lago - Bolsena	**229.979**	**192.943**	**3.451**	**32**	**19**	**3.608**	**196.551**
Solar do Bosque	**201.649**	**171.068**	**2.123**	**53**	**23**	**-**	**171.068**

Entorno

Distâncias - Mobilidade

- Av. Assis Brasil - 3,4 km
- Av. Baltazar de O. Garcia – 3,1 km
- Av. Bernardino Silveira Pastoriza – 600 m
- Av. Francisco Silveira Bittencourt – 1,8 km

Raio 2,5 Km

- Centro de Alvorada
- Fiergs

Concorrência

Porto Versalhes (MRV) – 3,4 km

- Preço Cheio (UH mais barata): R$ 216.900
- Avaliação: R$ 208.000
- Renda: R$ 2.320
- Estoque: 168
- 40% Vaga de Estacionamento
- Diferenciais: chuveiro a gás, circuito fechado de TV para segurança.

Parecer: Acreditamos que o preço é POSSÍVEL com o VSO proposto. Entendemos que esse empreendimento atenderá a demanda orgânica da sua microrregião, suprindo o stockout que seria gerado pelo Quinta do Lago Bolsena.

Pareceres

Análise da Mancha e Implantação

Operações

Inteligência de Mercado

Financeiro

Informações Gerais

Solar do Bosque - RS - Porto Alegre Capital

Datas e Prazos

	Compra	Lançamento	Início Obra	Término Obra	LÇTO até IO	IO até TO	Chaves	LÇTO até Chaves
Consolidado	nov-23							
c/ vaga carro		jun-25	dez-25	jun-27	6 meses	18 meses	jun-28	36 meses
c/ vaga moto		jun-25	dez-25	jun-27	6 meses	18 meses	jun-28	36 meses
s/ vaga		jun-25	dez-25	jun-27	6 meses	18 meses	jun-28	36 meses

Terreno e Incorridos

TOTAL (R$ + Perm.):	10,52 MM	**Incorrido Terreno:** 0,00 MM	**Área do Terreno (100%):**	19.075 m²	**Área Líquida do Terreno:** 19.075 m²
Cash:	0,00 MM		**Custo de terreno m²:**	551,7	**Custo de terreno m² Área Líquida:** 551,7
Permuta Financeira:	10,52 MM (8,00%)		**VaR 25 (R$ mil):**	0	**Fração Terreno/Terreno + Custo Obra (%VGV):** 8,0% / 57,9%
Permuta Física:	0,00 MM (0,00%)		**VaR 26 (R$ mil):**	0	**CA Máx/Proj.** 1,3 / 1,3
Ato / %VGV:	0,00 MM / 0,0%		**Incorrido de Construção:**	0,35 MM	**Incorridos de Incorporação:** 0,61 MM

Vendas

Fases	Nº Pavimentos	Preço Raso Unit.	Qtde	Preço Unit.	Aval. CEF	Cond. Parcela	% Pró-soluto	% TCD
c/ vaga carro	T+4	179.406	174	199.051	209.000	96,7%	63,8%	65,9%
c/ vaga moto	T+4	173.150	22	192.796	203.000	95,8%	73,0%	76,5%
s/ vaga	T+4	168.038	494	187.589	199.000	96,8%	71,8%	83,3%

Unidades Totais:	690	**Preço Médio:**	190.646	**Renda Média:**	2.494	**ITBI+Emol. Unit. Médio:**	1.086
Unidades Tenda:	690	**Avaliação Média:**	201.649	**Ato:**	1.105 (0,44 Salários)	**Custo do Ciclo Unit.:**	12.487
VSO:	53 Unidades	**VGV Total:**	131.545.540	**FGTS:**	832 (0,33 Salários)	**Preço Raso Médio:**	171.068
RET Médio:	1,2%	**VGV Tenda:**	131.545.540	**% em RET 1%:**	93%	**Adc. Tx. de Aceleração Médio:**	800

Construção

Custo Total Unit. | Corrigido:	95.208 | 94.662	**Eventuais:**	2,00%	**Área priv (m²):**	36,00	**Gape / Mês Unit.:**	11,08

Resultado

LI (R$):	**19.733.753**	**LI:**	**20,04%**	**Exposição de Caixa (R$):**	**10.668.701**	**Margem Bruta Econômica:**	**35,48%**
TIR:	**164,91%**	**LI Aprovação:**	**20,00%**	**Ger. Caixa 12 meses (R$):**	**(9.420.376)**	**Margem Bruta REF:**	**37,23%**
Exposição de Caixa:	**8,06%**	**Δ LI:**	**0,04%**	**Ger. Caixa 24 meses (R$):**	**21.009.022**	**Margem Rasa Econômica:**	**27,31%**
Payback Contingente (21 m):	**16 m/ (-5 m)**	**LI Marginal:**	**21,10%**	**Ger. Caixa Marginal (R$):**	**33.476.672**	**Margem Rasa REF:**	**30,05%**
Payback Consolidado:	**16 meses**					**Margem de Contribuição Econômica:**	**25,29%**

DRE

R$ Mil - Valores Nominais - Compra	Solar do Bosque		c/ vaga carro		c/ vaga moto		s/ vaga	
	Nominal	%	Nominal	%	Nominal	%	Nominal	%
Receita	132.291	100,0%	34.777	100,0%	4.268	100,0%	93.245	100,0%
PIS/COFINS	(885)	0,7%	(334)	1,0%	(41)	1,0%	(511)	0,5%
Custo Total	(84.782)	64,5%	(21.492)	62,4%	(2.695)	63,7%	(60.595)	65,3%
Custo Terreno	(10.348)	7,9%	(2.723)	7,9%	(334)	7,9%	(7.292)	7,9%
Custo Relacionados a Terreno	(1.296)	1,0%	(331)	1,0%	(41)	1,0%	(924)	1,0%
Custos de Incorporação	(957)	0,7%	(236)	0,7%	(18)	0,4%	(703)	0,8%
Custo de Construção	(72.181)	54,9%	(18.202)	52,8%	(2.301)	54,4%	(51.677)	55,7%
Lucro Bruto Econômico	46.624	35,5%	12.952	37,6%	1.533	36,3%	32.139	34,7%
Custo para Rateio	-	0,0%	-	0,0%	-	0,0%	-	0,0%
Lucro Bruto Contábil	46.624	35,5%	12.952	37,6%	1.533	36,3%	32.139	34,7%
Despesas de Selling	(10.343)	7,9%	(2.710)	7,9%	(332)	7,9%	(7.301)	7,9%
Contingência	(3.043)	2,3%	(800)	2,3%	(98)	2,3%	(2.145)	2,3%
Margem de Contribuição	33.238	25,3%	9.443	27,4%	1.102	26,1%	22.694	24,5%
IR e CSLL	(724)	0,5%	(273)	0,8%	(33)	0,8%	(418)	0,4%
Margem Líquida	32.514	24,7%	9.170	26,6%	1.069	25,3%	22.276	24,0%
Lucro Bruto REF Unit.	71.680	37,2%	80.081	39,5%	73.790	37,7%	69.322	36,3%
Lucro Raso REF Unit.	51.786	30,1%	60.109	32,9%	53.881	30,7%	49.456	28,9%

R$ Mil - VPL - Compra	Solar do Bosque		c/ vaga carro		c/ vaga moto		s/ vaga	
	VP	%	VP	%	VP	%	VP	%
Receitas	98.463	100,0%	25.910	100,0%	3.166	100,0%	69.388	100,0%
PIS/COFINS	(649)	0,7%	(245)	0,9%	(30)	0,9%	(374)	0,5%
Custos e Despesas Totais	(78.080)	79,3%	(19.940)	77,0%	(2.494)	78,8%	(55.646)	80,2%
Custo Terreno	(7.558)	7,7%	(1.989)	7,7%	(243)	7,7%	(5.326)	7,7%
Custo Relacionados a Terreno	(1.342)	1,4%	(343)	1,3%	(43)	1,4%	(956)	1,4%
Custos de Incorporação	(814)	0,8%	(204)	0,8%	(14)	0,5%	(596)	0,9%
Custo de Construção	(57.270)	58,2%	(14.442)	55,7%	(1.826)	57,7%	(41.002)	59,1%
Despesas de Selling	(9.355)	9,5%	(2.444)	9,4%	(304)	9,6%	(6.606)	9,5%
Contingência	(1.210)	1,2%	(318)	1,2%	(39)	1,2%	(853)	1,2%
IR e CSLL	(531)	0,5%	(200)	0,8%	(24)	0,8%	(306)	0,4%
Lucro Imobiliário	19.734	20,0%	5.725	22,1%	642	20,3%	13.367	19,3%

DRE

R$ Mil - Valores Nominais - Compra	Solar do Bosque		Primeira Fase		Demais Fases	
	Nominal	%	Nominal	%	Nominal	%
Receita	132.291	100,0%	132.291	100,0%	-	100,0%
PIS/COFINS	(885)	0,7%	(885)	0,7%	0	0,0%
Custo Total	(84.782)	64,5%	(84.782)	64,5%	-	0,0%
Custo Terreno	(10.348)	7,9%	(10.348)	7,9%	-	0,0%
Custo Relacionados a Terreno	(1.296)	1,0%	(1.296)	1,0%	-	0,0%
Custos de Incorporação	(957)	0,7%	(957)	0,7%	-	0,0%
Custo de Construção	(72.181)	54,9%	(72.181)	54,9%	-	0,0%
Lucro Bruto Econômico	46.624	35,5%	46.624	35,5%	0	100,0%
Custo para Rateio	-	0,0%	-	0,0%	-	0,0%
Lucro Bruto Contábil	46.624	35,5%	46.624	35,5%	0	100,0%
Despesas de Selling	(10.343)	7,9%	(10.343)	7,9%	-	0,0%
Contingência	(3.043)	2,3%	(3.043)	2,3%	-	0,0%
Margem de Contribuição	33.238	25,3%	33.238	25,3%	0	100,0%
IR e CSLL	(724)	0,5%	(724)	0,6%	0	100,0%
Margem Líquida	32.514	24,7%	32.514	24,7%	0	200,0%

R$ Mil - VPL - Compra	Solar do Bosque		Primeira Fase		Demais Fases	
	VP	%	VP	%	VP	%
Receitas	98.463	100,0%	98.463	100,0%	-	100,0%
PIS/COFINS	(649)	0,7%	(649)	0,7%	-	#DIV/0!
Custos e Despesas Totais	(78.080)	79,3%	(78.080)	79,3%	-	#DIV/0!
Custo Terreno	(7.558)	7,7%	(7.558)	7,7%	-	#DIV/0!
Custo Relacionados a Terreno	(1.342)	1,4%	(1.342)	1,4%	-	#DIV/0!
Custos de Incorporação	(814)	0,8%	(814)	0,8%	-	#DIV/0!
Custo de Construção	(57.270)	58,2%	(57.270)	58,2%	-	#DIV/0!
Despesas de Selling	(9.355)	9,5%	(9.355)	9,5%	-	#DIV/0!
Contingência	(1.210)	1,2%	(1.210)	1,2%	-	#DIV/0!
IR e CSLL	(531)	0,5%	(531)	0,5%	-	#DIV/0!
Lucro Imobiliário	19.734	20,0%	19.734	20,0%	-	#DIV/0!
AVM	-		-		-	

Comparativo

Comparativo dos Estudos - Consolidado	Escritura	BP - 2025	Atual	Atual vs BP - 2025	Δ%
Data Estudo:	abril-25	setembro-24	junho-25	9 Meses	N/A
Lançamento:	junho-25	julho-25	junho-25	-1 Meses	N/A
Uhs:	690	690	690	-	0,0%
Preço Nominal:	200.701	201.648	190.646	(11.003)	-5,5%
Preço Raso:	179.501	182.544	171.068	(11.477)	-6,3%
Preço Nominal Inflacionado:	212.093	221.651	193.864	(27.786)	-12,5%
Preço Raso Inflacionado:	189.709	200.677	173.970	(26.707)	-13,3%
Renda Média:	2.494	2.942	2.494	(448)	-15,2%
RET Médio:	0	1,3%	1,2%	-0,1 p.p.	-9,3%
% em RET 1%:	1	88,8%	92,9%	4,1 p.p.	4,7%
VSO:	27	27	53	27	100,0%
ITBI/Emol. Inf (Unit)[2]:	1.987	1.681	1.886	205	12,2%
Avaliação:	218.942	196.698	201.649	4.951	2,5%
Prazo construção F1:	15	13	18	5	38,5%
Prazo de Pró-Soluto F1:	20	18	23	5	27,8%
Custo Total Inf (Unit):	126.354	127.386	122.872	(4.514)	-3,5%
Custo Construção (Unit):	94.218	85.953	95.208	9.255	10,8%
Fração de construção:	47%	42,6%	49,7%	7,0 p.p.	16,5%
INCC Folha Rosto:	1.178,39	1.126,92	1.191,33	64	5,7%
Custo Terreno Inf:	11.278.836	12.073.856	10.348.319	(1.725.537)	-14,3%
Custo Relacionados a Terreno (Unit):	1.718	6.579	1.879	(4.700)	-71,4%
Fração do Terreno[1]:	8,0% / 54,9%	8,0% / 50,6%	8,0% / 57,9%	0,0 p.p.	0,0%
Custo de Incorp. por uh:	2.413	1.010	1.386	376	37,2%
ITBI/Emol. Inf (Total)[2]:	1.371.244	1.160.224	1.301.340	141.116	12,2%
Custo do Ciclo (Unit):	13.146	13.207	12.487	(721)	-5,5%
Lucro Imobiliário:	22,4%	25,4%	20,0%	-5,4 p.p.	-21,2%
LI Marginal:	22,9%	25,7%	21,1%	-4,6 p.p.	-17,8%
Exposição de caixa:	6,6%	8,7%	8,1%	-0,6 p.p.	-6,9%
TIR:	151,7%	139,8%	164,9%	25,1 p.p.	18,0%
Margem Bruta REF:	41,0%	43,1%	37,2%	-5,9 p.p.	-13,7%
Margem Bruta Econômica:	38,9%	41,3%	35,5%	-5,8 p.p.	-14,1%
Margem Rasa REF:	34,1%	37,2%	30,1%	-7,1 p.p.	-19,2%
Margem Rasa Econômica:	31,1%	34,7%	27,3%	-7,4 p.p.	-21,3%
Margem Contribuição Econômica:	28,7%	31,3%	25,3%	-6,0 p.p.	-19,2%
Payback Contingente (Régua 21 m):	17 m/ (-4 m)	15 m/ (-6 m)	16 m/ (-5 m)	1	6,7%
Payback Consolidado:	17	15 Meses	16 Meses	1 Meses	6,7%

[1] Valor do terreno contratual

[2] ITBI com taxa de Aceleração

Obrigado