Tenda

sua próxima conquista

Book de Escritura

Regional: RJ

Projeto: Porto Lima & Porto Seleta

Data Comitê: 20/02/2026

Questionamentos – Comitê Digital 09.02.2026

Nome	Porto Lima - Escritura	Observação - Porto Lima
Fabricio Quesiti Arrivabene	Aprovado	Ok
Renan Barbosa Sanches	Aprovado	ok
Amanda da Silva Bezerra	Aprovado	ok
Alejandro Octavio Abiusi	Aprovado	ok
Rodrigo Osmo	Discutir em comitê	(1) Queria uma avaliação no voice over, do jurídico, sobre o risco dos passivos do Sr. Letério virem a contaminar o terreno
Luiz Mauricio de Garcia Paula	Aprovado	ok
Andre Luis Menegazzo Padilha	Aprovado	ok
Alexandre Regis de Oliveira	Aprovado	ok

Resposta Jurídico

Opinamos pelo **prosseguimento da escritura de compra do imóvel**, com a **ressalva** de que ainda existem certidões pendentes que devem ser apresentadas pelo vendedor e analisadas pela Cia antes da lavratura da referida escritura. A seguir, o **histórico** do Imóvel e a **análise jurídica**.

CADEIA DOMINIAL:

2007

Aquisição do Imóvel por Letério

Vendedores: *José de Barros Silva e outros*
Compradores: *Leterio Rubio Giannone e Renata M. Pança Gianonne*

2013

Registro Escritura de Promessa de Venda e Compra (PVC)

Promitentes Vendedores: *Letério Rubio Giannone e Renata Mangini*
Promissária Compradora: *Posto Mané Garrincha de Botafogo Ltda*

2022

Registro Escritura de Compra e Venda

Promitentes Vendedores: *Letério Rubio Giannone e Renata Mangini*
Promissária Compradora: *Posto Mané Garrincha de Botafogo Ltda*

2026

(...) Escritura de Compra e Venda (Tenda)

Histórico do Imóvel: O negócio entre o antecessor Sr. Letério e o Posto Mané Garrincha iniciou com a celebração de PVC em 2013.

Contingências Econômicas do Sr. Letério: Na data da PVC, o Sr. Letério, como pessoa física, não possuía dívidas registradas em seu nome. As obrigações existentes estavam vinculadas apenas às suas pessoas jurídicas e somavam cerca de R$ 2 MM. Esse valor é muito inferior ao passivo atualmente apurado, que alcança aproximadamente R$ 276 MM.

Probabilidade de materialização de questionamentos: Desde o registro da PVC, passou-se longo período sem qualquer medida constritiva ou iniciativa de credores para desconsiderar a personalidade jurídica das empresas devedoras e atingir o patrimônio pessoal do Sr. Letério. Esse tempo decorrido, somado à ausência de indícios de confusão patrimonial e ao fato de que as empresas estão em recuperação judicial com plano homologado e em cumprimento, sustenta a avaliação de que o risco de questionamento por alegação de fraude contra credores é ***Remoto.*** Esta análise, no entanto, não é um juízo de valor jurídico, mas sim probabilístico.

Análise Jurídica: Na remota hipótese de questionamento que busque alcançar o Imóvel, a defesa sustentará que a PVC foi registrada e consolidou o direito real desde 2013, tornando a situação oponível a terceiros*. Nesse cenário, o êxito da defesa é ***Provável***. A tese contrária estaria apoiada em entendimento minoritário segundo o qual, perante terceiros, a alienação somente teria ocorrido com o registro da escritura definitiva em 2022.

* Art. 1.417 (Código Civil): *"Mediante promessa de compra e venda, em que se não pactuou arrependimento,* ***celebrada por instrumento público ou particular, e registrada no Cartório de Registro de Imóveis, adquire o promitente comprador direito real à aquisição do imóvel****".*

One Page – Porto Lima

[1]

Cidade	Rio de Janeiro	Mancha de demanda	RJ - RZO3/4 - Campo Grande
Regional	RJ	Cluster MPR	2 - Amarelo
Cenário de Aprovação	Aprovação	Tipo de Aprovação	Consolidado
Fase Anterior	N/A		
Tipo de Comitê	Escritura	Versão da VF	Versão 1.0: Fev

[2]

Unidades (Fases)	907 (2)	CA Máx | Proj	3,0 | 1,6
Unidades com Vaga (%)	104 (11%)	Escritura | Lançamento	mar/26 | mar/26
Unidades com Varandas (%)	0 (0%)	Tipologia	F2 - Concreto

[3]

Valor Líquido do Terreno (% VGV)	8.500 (4,4%)	Un. Perm. Fís (% Ter)	0 (0,0%)
Cash (Correção)	8.500 (IPCA)	%VGV Perm Fin Líquida (% Ter)	0,0% (0,0%)
Valor R$/m²	371	VAR (%VGV)	1334 (0,7%)

[4]

Custo Construção (%VGV)	85.372 (44,3%)	Indireto Unit.	18.505
Prazo da Obra (meses)	12	Torre Unit.	43.749
Custo Total Unit. (LPU):	94.126 (99)	Infra Unit.	18.327
Início de Obra	set-26	Fundação Unit.	5.633

[5]

Preço Nominal Unit.	212.375	VSO	35
Preço Raso Unit.	187.804	Referência	Vision
Avaliação Unit.	202.491	Renda (% em RET 1%)	2.581 (72,1%)

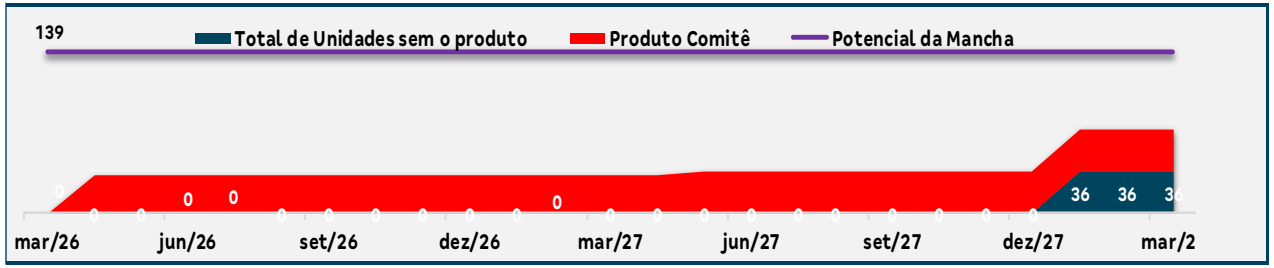

LI (Régua):	25,3% (22,0%)	Margem Bruta Econômica:	43,3%
LI Marginal:	26,6%	Margem Rasa Econômica:	35,0%
Margem Bruta REF:	45,2%	Margem Contribuição Econômica:	32,6%
Margem Rasa REF:	38,1%	Exposição (% VGV):	19.167 (9,6%)
TIR:	101,9%	VGV Total:	192.624
Payback Contingente (21 m) :	16 m/ (-5 m)	Ger. Caixa 12 meses (R$):	(17.445)
Payback Consolidado:	16	Ger. Caixa 24 meses (R$):	6.490

Destaques

[1] Imóvel fica localizado na mancha RZO3/4, faz divisa com os condomínios já lançados Porto Barão (300 uh's) e Porto Valência (480 uh's), próximo à Av. Brasil (principal via de acesso entre a Zona Central e Zona Oeste) e à Est. Do Mendanha (uma das principais vias de acesso de Campo Grande).

[2] O lançamento do projeto proposto é sequencial ao Porto Valência, com os condomínios Porto Lima I (434 uh's) e Porto Seleta (473 uh's), totalizando 907 uh's desenvolvidas de forma sequencial. O Porto Seleta ainda não entrou na esteira de Getec, o projeto foi parametrizado com o AP

[3] Condição do négocio: R$ 8,5 MM em cash (Fração de 4,4%), com sinal pago de R$ 350 mil em out/23 e novo sinal de R$ 350 mil pago em mai/25 e o saldo restante de R$ 7,8 MM a ser pago em 42 parcelas corrigidas pelo índice IPCA a partir da assinatura da ECV.

[4] Projeto contará com urbanização da via lateral projetada, garantindo testada e acesso para o condomínio II, devido a longa extensão dessa urbanização o custo II está maior que a média.

[5] Preço vision com avaliação atual do Porto Valência (R$ 214 mil com vaga e R$ 201 mil sem vaga). A excelente perfomance do Porto Valência mostra a solidez destes projetos (Jan/26: VSO: 73 PM Nominal: R$ 206.975 PM Raso: R$ 188.127.
Adicional de selling considerado em VF de -0,37%.

- Pareceres
- Análise da Mancha e Implantação
- Prospecção
- Operações
- Inteligência de Mercado
- Financeiro

Farol Pareceres – Porto Lima

Área	Riscos Associados	Parecer	Criticidade
Jurídico	Due Diligence concluída em Jan/24 e renovada em Abr/25 e Jan/26. Sob o aspecto dominial, a matrícula está regular, com cadeia ininterrupta e escritura definitiva registrada em favor da atual Vendedora (Posto Mané Garrincha). Ocorre, no entanto, que o proprietário anterior (Sr. Letério) vendeu o imóvel para a Vendedora através de PVC em 2013, quando possuía passivo de R$ 2 MM e não havia insolvência verificável, mas apenas lavrando efetivamente a EVC em 2022, período em que passou a registrar passivo de R$ 259 MM. Do ponto de vista ***probabilístico***, a ***chance de ocorrência*** de questionamento por eventual credor com alegação de fraude na aquisição é ***Remota***, considerando o tempo já transcorrido sem qualquer impugnação até a data presente. Do ponto de vista de ***prognóstico jurídico*** (*avaliação da qualidade do direito envolvido*, caso o retrorreferido evento aconteça) é de que é ***Possível*** defender legalmente que a PVC, de 2013, pelas suas características específicas, foi o ato jurídico de efetiva transferência de propriedade, dificultando eventuais alegações de fraude. Quanto ao ***risco de contingências econômicas dos antecessores***, vale frisar: ***(i)*** estão pendentes de envio para análise os extratos de débitos fiscais da Vendedora e seus sócios para fins de análise final conclusiva; e, ***(ii)*** a apuração de passivos do cônjuge da sócia, casado em regime de comunhão total, não foi realizada diante da probabilidade ***Remota*** de *ocorrência* de desconsideração societária em cadeia que alcance a Vendedora. **Conclusão:** opinamos pelo prosseguimento da escritura, ok com ressalvas, condicionada à apresentação e análise de certidões fiscais atualizadas ainda pendentes.	Ok com ressalvas	
Legalização	Projeto Legal aprovado e Licença de Obras expedida. Desmembramento em fase final de aprovação, pendente assinatura de termos de urbanização e recuo, já validados tecnicamente. Custo relativo ao pagamento de pecúnia para doação de lote previsto na viabilidade. Licenciamento Ambiental encontra-se em fase final para emissão da Licença de Instalação. Licença de Recuperação Ambiental emitida. O laudo ambiental aponta a presença de benzeno em concentrações baixas e sem indícios de risco à saúde, o que deverá ser comprovado após a realização de duas campanhas de monitoramento ambiental em fev/26 e jul/26	Ok com ressalvas	
Produto	Sem comentários.	Ok	
GETEC	2º campanha de sondagem sendo realizada no cond. 1 com data de finalização 26/01. Cond. 2 desenvolvido com AP, ainda não iniciou na esteira.	Ok com ressalvas	
Logística	Obrigatório uso de parte do condomínio 2 como área de apoio operacional, sem essa área não é possível realizar a obra.	Ok com ressalvas	
Contratação	NA	Ok	
Inteligência de mercado	Preço Vision como factível	Ok	
Comercial/Ciclo	Ciclo Financeiro avalia o Preço Vision como **factível.**	Ok	
Estudos Econômicos	Ok, sem riscos associados.	Ok	

Pareceres

Análise da Mancha e Implantação

Prospecção

Operações

Inteligência de Mercado

Financeiro

Mancha de Demanda

MANCHAS DE DEMANDA

- RZO 1/6 – Rio de Janeiro Oeste

Lançamento

1. Jardim Margarida | Peônia
2. Parque Iris | Hortênsia | Orquídea
3. Porto Barão | P. Valencia
4. Reserva Carioca

LandBank

5. Vista Senna
6. Porto Lima
7. Belo Oeste

Cluster MPR – (Comitê)
Cluster 1 - Vermelho

Região
Capital

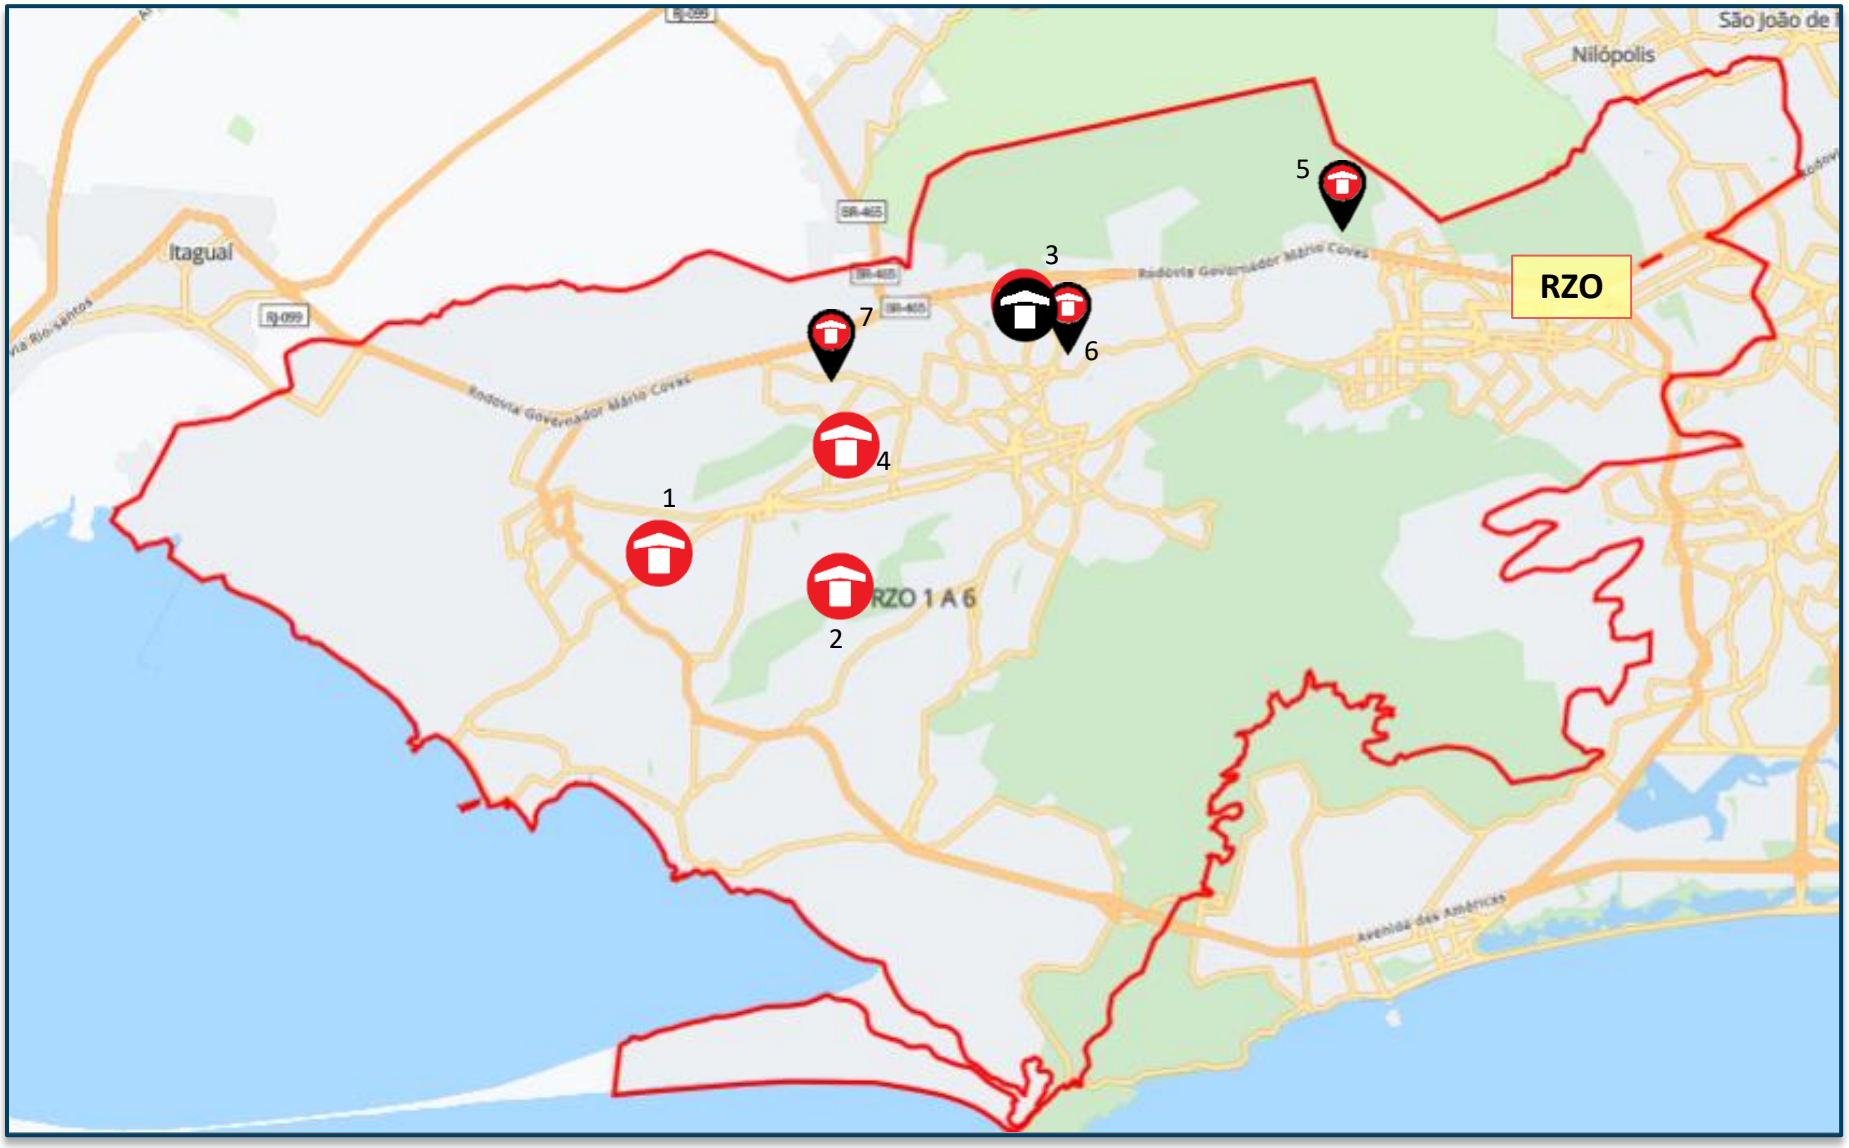

Lançados LandBank Comitê

PRODUTO

Empreendimento Porto Lima
Escritura

	Informações Gerais	
Terreno	**Área terreno**	23.010,36m²
	Menor poligonal	22.905,483m²
	App/fna	Sim
	Reserva de calçada/ melhoramento viário	Sim
	Área liquida	22.905,483m²
	Zoneamento	ZUPI C AP5
	Ca máximo	3,0
	Ca básico	1,0
	Ca projetado	Cond.01: 1,62 Cond.02: 1,64
	Gabarito máximo	T+4
Geral	**Total uh**	Cond.01: 434 Cond.02: 473 Total: 907
	Total de vagas	Cond.01: 54 (12,44%) Cond.02: 53 (11,21%) Total: 107 (11,80%)

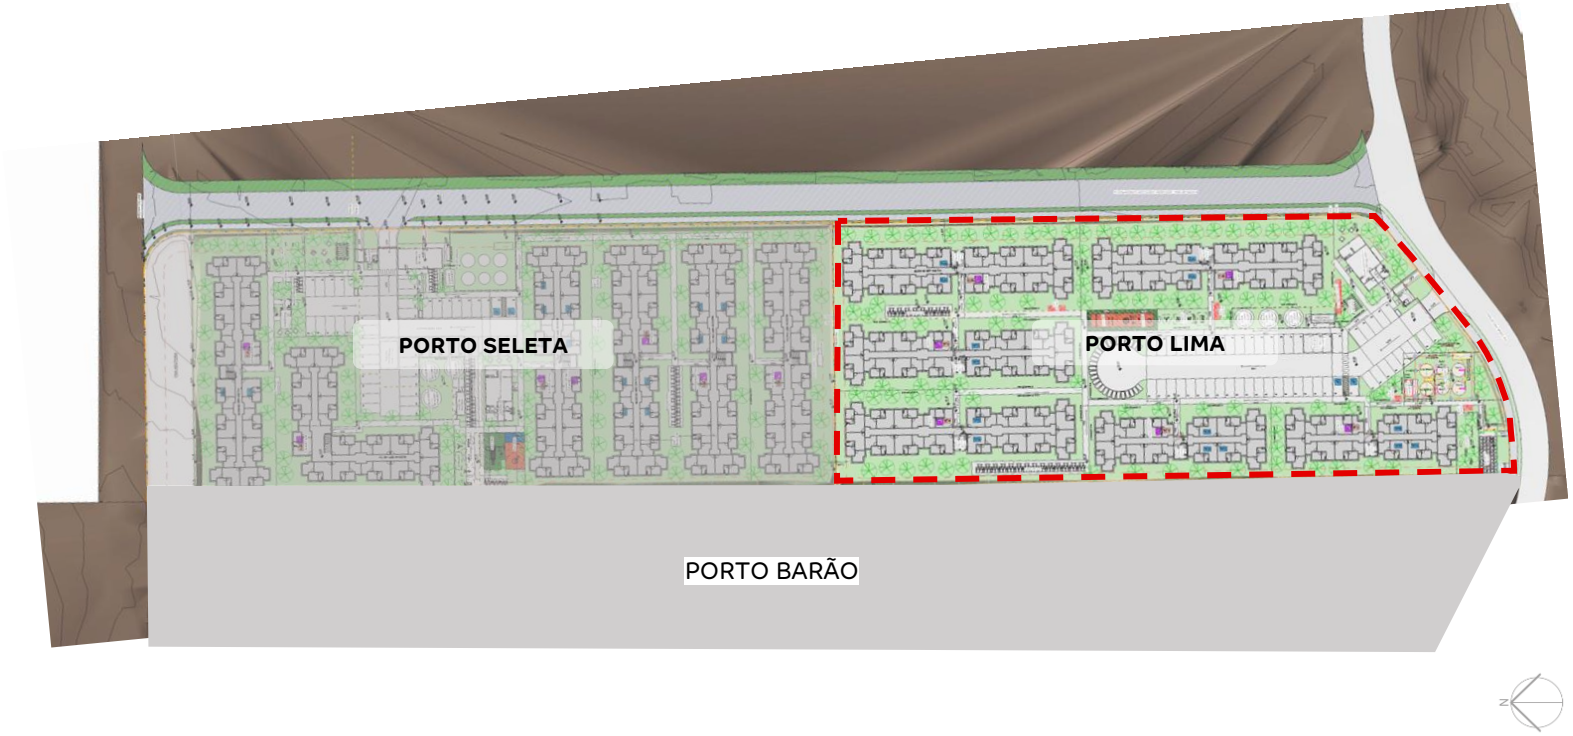

9

PRODUTO

Empreendimento Porto Lima
Escritura

Informações Gerais – Condomínio 01		
Terreno	**Área terreno**	10.951,31m²
	Menor poligonal	10.876,565 m²
	App/fna	Sim - 61,139m²
	Reserva de calçada/ melhoramento viário	Sim
	Área liquida	10.815,426
Diretrizes Urbanísticas	**Zoneamento**	ZUPI C AP5
	Ca máximo	3,0
	Ca básico	1,0
	Ca projetado	1,64
Geral	**Total uh**	434
	Total de vagas exigido	-
	Total de vagas projetado	54 vagas de carro e 30 vagas de moto
Tipologia	**Tipologia**	Modular sem elevador
	Gabarito máximo	T+4 (LC 97)
	Gabarito projetado	T+4 (LC 97)
	Lâmina	02 - 12PP | 04 – 16PP
	Área privativa	33,98m² ~ 34,12m²
Condomínio	**Unidade pcd**	14 U.A
	Unidade lazer|técnica	06
	Torre	06
	Fase	Única
Lazer	**Lazer Interno**	01- Espaço Teen, 02- Espaço Saúde, 03-Espaço Fitness, 04- Espaço Office, 05- Brinquedoteca, 06- Sport Bar
	Lazer Externo	07- Play Kids, 08- Mini Quadra Descoberta, 09- Play Pet, 10- Salão de Festas com Coworking, 11- Fitness Externo

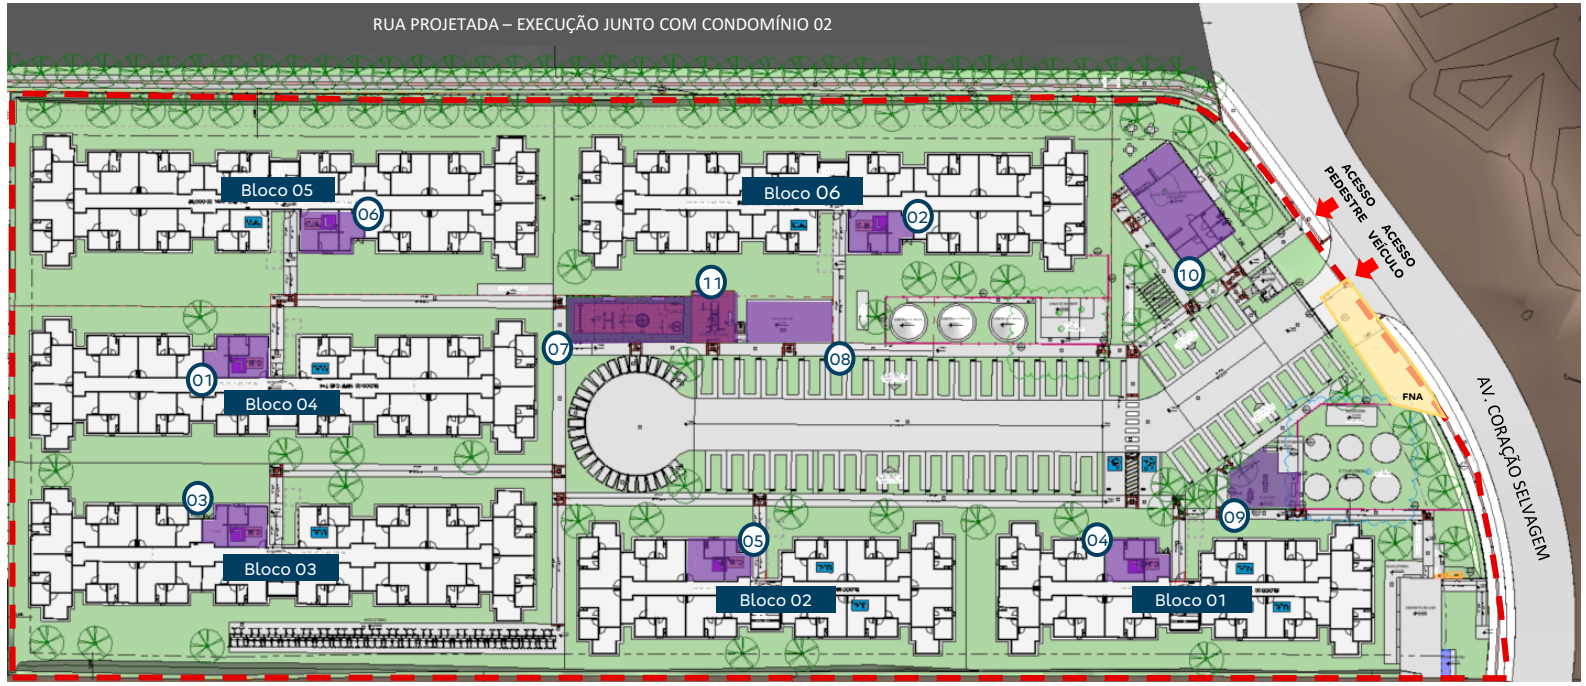

PRODUTO

Empreendimento Porto Lima
Escritura

	Descrição	Criticidade	Observação
Usabilidade	Acesso Empreendimento		
	Percurso do pedestre até torre		
Diferencial produto	Faixa de renda	2	
	Prime	Não	
	Super condomínio	Não	
	Atributos Infra	-	
	Atributos Torre	Não	
	Edifício Garagem	Não	

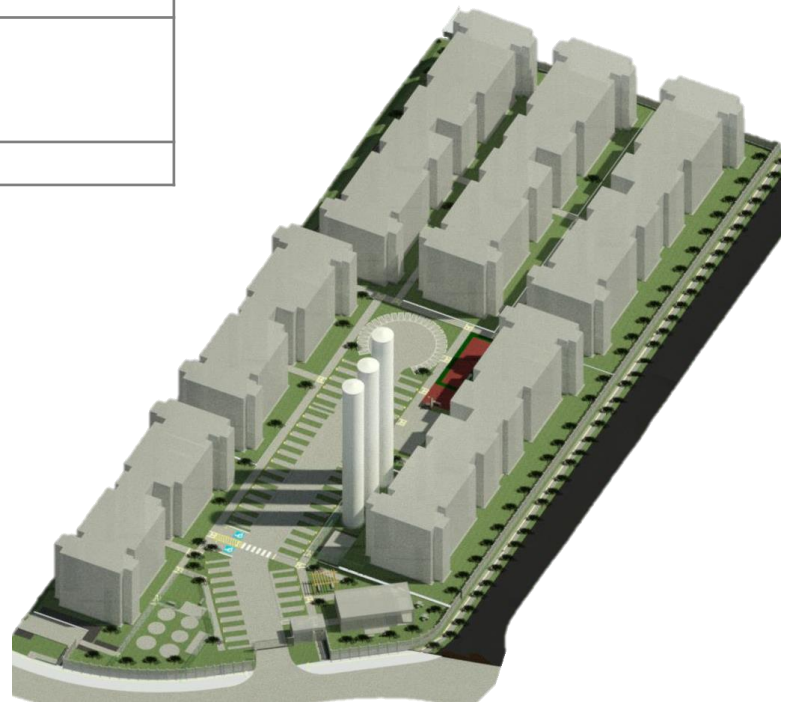

PRODUTO

Empreendimento Porto Lima
Escritura

Fase única: 434UH (Sendo 14 U.A) - 54 vagas de carro (Sendo 02 PCD) – 30 vagas de moto				
Módulo	**Blocos**	**UH**	**Vagas**	**Parecer**
Módulo 01	03 Blocos (T+4)	197 UH (Sendo 08 U.A)	54 vagas de carro (Sendo 02 PCD) e 30 vagas de moto	Dos Lazeres, estão contemplados no módulo 01 o Espaço Fitness, Brinquedoteca, Espaço Office, Play Kids, Fitness Externo, Mini Quadra Descoberta, Play Pet e Salão de Festas com Coworking. Demais lazeres que não estão contemplados neste módulo, necessário inclusão dessa informação no RI e material de vendas.
Módulo 02	03 Blocos (T+4)	237 UH (Sendo 06 U.A)	-	Dos Lazeres, estão contemplados no módulo 02 o Espaço Teen, Sport Bar e Espaço Saúde.

RUA PROJETADA

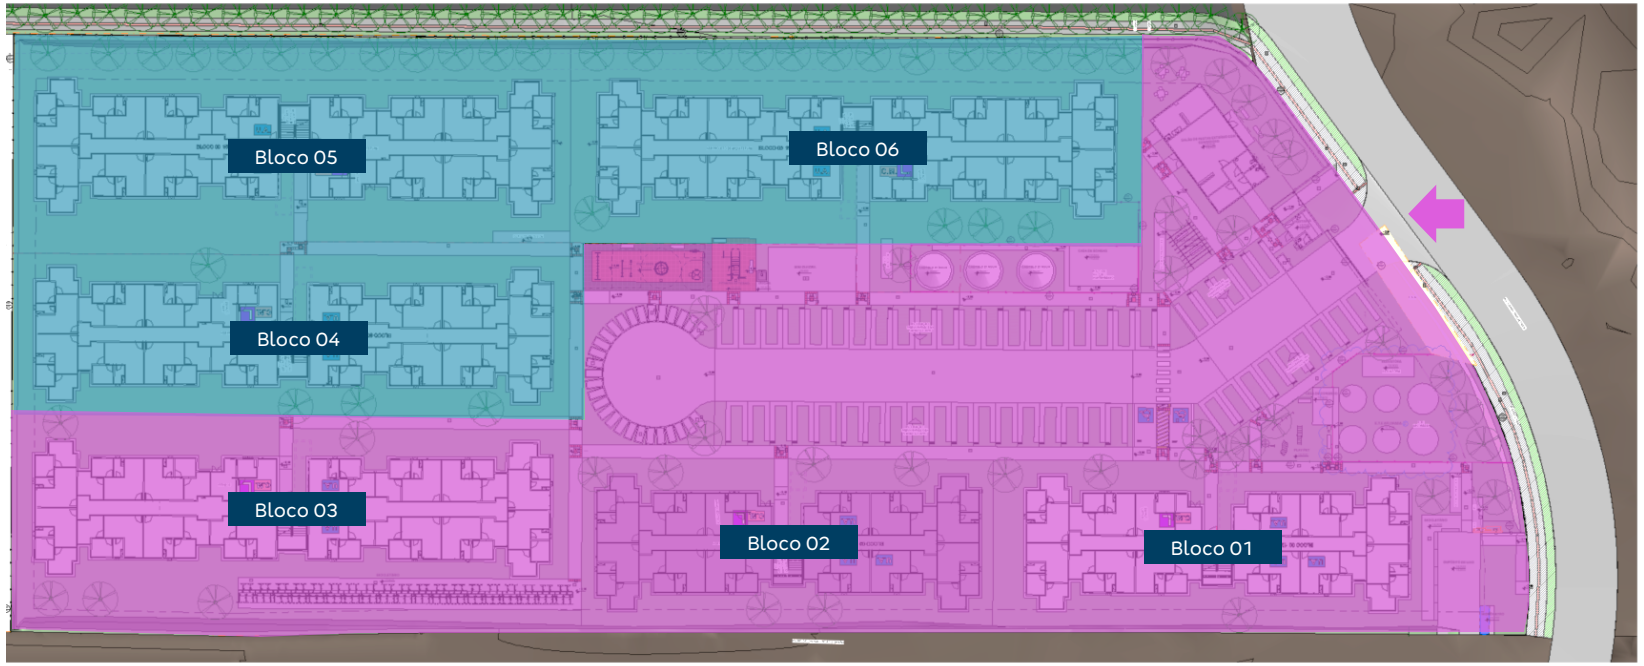

12

Pareceres

Análise da Mancha e Implantação

Prospecção

Operações

Inteligência de Mercado

Financeiro

Condições do Negócio

➢ **VALOR DO NEGÓCIO**

Condição atual: Pagamento em cash > R$ 8.500.000.00

- R$ 8.500.000 representados pela fração de 4,4% do VGV.
- R$ 350.000,00 (sinal), pago em 31/10/23.
- R$ 350.000,00 (novo sinal), pago em 12/05/25.
- Saldo de R$ 7.800.000 a ser pago em 42 parcelas no valor de R$ 185.714,29, cada, corrigidas pelo índice IPCA a partir da assinatura da ECV.
- R$ 78.718,70 pelos débitos de IPTU de 2023, 2024 e 2025 pagos pela Tenda (a fundo perdido).

➢ **PRAZOS CONTRATUAIS**

- PCV assinada em 16/03/22 com vencimento em 16/09/23. Termo aditivo assinado em 30/10/23 prorrogando prazo em 18 meses (mar/25), contra o pagamento do sinal realizado no mesmo ato.
- Novo Termo aditivo assinado em 08/04/25 prorrogando prazo em 12 meses (mar/26) mediante o pagamento de um novo sinal em mai/25. Totalizando 48 meses de vinculo

➢ **GARANTIAS**

- Para Vendedores: aval CONSTRUTORA TENDA;
- Para Tenda: n/a.

➢ **CORRETAGEM**

- 5% do valor da ECV em favor da BELA COPACABANA IMÓVEIS EIRELI, sendo um adiantamento de R$ 35.000,00 pagos em 29/11/23. Restante a ser pago em até 30 dias após a assinatura da ECV.

- Pareceres
- Análise da Mancha e Implantação
- Prospecção
- Operações
- Inteligência de Mercado
- Financeiro

Custo de Construção

	PORTO LIMA REV01 COND. 1 - FASE ÚNICA	PORTO LIMA REV01 COND. 2 - FASE ÚNICA	PORTO LIMA REV01 CONSOLIDADO ENTRE COND. FASE ÚNICA	PORTO LIMA CEN04 | REV06.1 CONSOLIDADO	LVS PORTO BARAO
Torres	12	12	12	12	15
Unidades Construídas	440	480	440 | 480	280 | 160 | 320 | 160	300
Unidades Vendidas	434	473	434 | 473	276 | 158 | 315 | 158	
Total Unidades Vendidas			907	907	
Condomínios (qta.)	2	2	2	2	
Cidade	Rio de Janeiro	Rio de Janeiro	Rio de Janeiro	Rio de Janeiro	Rio de Janeiro
Produto / Selo	F2 MODULAR	F2 MODULAR	F2 MODULAR	F2 MODULAR	F2
Tipologia	4 Torre | T+4 | 16PP	5 Torre | T+4 | 16PP	09 Torre | T+4 | 16PP	09 Torre | T+4 | 16PP	T+04 | 4PP
Tipologia	2 Torre | T+4 | 12PP	1 Torre | T+04 | 16PP (L)	2 Torre | T+4 | 12PP	2 Torre | T+4 | 12PP	
Tipologia			1 Torre | T+04 | 16PP (L)	1 Torre | T+04 | 16PP (L)	
Tipologia					
Tipologia					
Tipologia					
Projeto Infra	AP	AP	AP	AP	
Projeto Torre	AP	AP	AP	AP	
Mês Base	janeiro-26	janeiro-26	janeiro-26	abril-25	março-23
Incc	1.225,633	1.225,633	1.225,633	1.178,386	1.056,418
LVS	novembro-25	novembro-25	novembro-25	fevereiro-25	novembro-25
Base de Preço	LPU 99	LPU 99	LPU 99	LPU 89	LPU 65
Takt	2+2	2+2	2+2	2+2	
Prazo (mês)	12	13	12 | 13	11 | 9 | 12 | 9	12
CUSTO TOTAL I	R$ / UND R$ 90.206	R$ / UND R$ 89.929	R$ / UND R$ 90.061	R$ / UND R$ 88.561	R$ / UND R$ 90.750
Indireto	R$ 18.882	R$ 18.158	R$ 18.505	R$ 21.077	R$ 17.622
Torre	R$ 43.674	R$ 43.817	R$ 43.749	R$ 42.190	R$ 41.585
Infra	R$ 18.615	R$ 18.063	R$ 18.327	R$ 16.524	R$ 22.203
Fundação	R$ 5.696	R$ 5.597	R$ 5.644	R$ 5.010	R$ 4.697
EEE	R$ 150	R$ 137	R$ 143	R$ 248	R$ 329
ETE	R$ 1.368	R$ 1.255	R$ 1.309	R$ 1.134	R$ 1.505
Contenção	R$ 85		R$ 41		R$ 5
Terraplenagem	R$ 1.736	R$ 2.901	R$ 2.343	R$ 2.378	R$ 2.804
CUSTO TOTAL II	R$ 4.033	R$ 4.033	R$ 4.033	R$ 2.365	R$ 4.383
Urbanização	R$ 1.721	R$ 1.721	R$ 1.721	R$ 1.553	R$ 3.547
Drenagem	R$ 591	R$ 591	R$ 591	R$ 521	
Extensão de Rede Elétrica	R$ 364	R$ 364	R$ 364	R$ 34	
Extensão de Rede Hidráulica	R$ 1.357	R$ 1.357	R$ 1.357	R$ 256	R$ 836
CUSTO TOTAL III					
Incorridos					
CUSTO TOTAL IV					
Aprendizado					
CUSTO TOTAL V				R$ 3.646	
Atualização por INCC				R$ 3.646	
CUSTO TOTAL I+II	R$ 94.239	R$ 93.962	R$ 94.094	R$ 90.925	R$ 95.133
CUSTO TOTAL I AO IV	R$ 94.239	R$ 93.962	R$ 94.094	R$ 94.571	R$ 95.133

Custo de Construção

	PORTO LIMA REV01 CONSOLIDADO FASEADO	PORTO LIMA CEN04 | REV06.1 CONSOLIDADO
Torres	12	12
Unidades Construídas	280 | 160 | 320 | 160	280 | 160 | 320 | 160
Unidades Vendidas	276 | 158 | 315 | 158	276 | 158 | 315 | 158
Total Unidades Vendidas	907	907
Condomínios (qta.)	2	2
Cidade	Rio de Janeiro	Rio de Janeiro
Produto / Selo	F2 MODULAR	F2 MODULAR
Tipologia	09 Torre | T+4 | 16PP	09 Torre | T+4 | 16PP
Tipologia	2 Torre | T+4 | 12PP	2 Torre | T+4 | 12PP
Tipologia	1 Torre | T+04 | 16PP (L)	1 Torre | T+04 | 16PP (L)
Projeto Infra	AP	AP
Projeto Torre	AP	AP
Mês Base	janeiro-26	abril-25
Incc	1225,633	1178,386
LVS	novembro-25	fevereiro-25
Indiretos	novembro-25	fevereiro-25
Base de Preço	LPU 99	LPU 89
Takt	2+2	2+2
Prazo (mês)	11 | 9 | 12 | 09	11 | 9 | 12 | 9

CUSTO TOTAL I	R$ / UND R$ 94.452	R$ / UND R$ 88.561	DIF R$ 5.892
Indireto	R$ 22.621	R$ 21.077	R$ 1.544
Torre	R$ 43.567	R$ 42.190	R$ 1.378
Infra	R$ 18.698	R$ 16.524	R$ 2.174
Fundação	R$ 5.654	R$ 5.010	R$ 643
EEE	R$ 143	R$ 248	-R$ 105
ETE	R$ 1.309	R$ 1.134	R$ 175
Contenção	R$ 41	R$ 0	R$ 41
Terrapplenagem	R$ 2.420	R$ 2.378	R$ 42
CUSTO TOTAL II	R$ 4.033	R$ 2.365	R$ 1.668
Urbanização	R$ 1.721	R$ 1.553	R$ 168
Drenagem	R$ 591	R$ 521	R$ 70
Extensão de Rede Eletrica	R$ 364	R$ 34	R$ 330
Extensão de Rede Hidráulica	R$ 1.357	R$ 256	R$ 1.101
CUSTO TOTAL III	R$ 0	R$ 0	R$ 0
Incorridos	R$ 0	R$ 0	R$ 0
CUSTO TOTAL IV	R$ 0	R$ 0	R$ 0
Aprendizado	R$ 0	R$ 0	R$ 0
CUSTO TOTAL V	R$ 0	R$ 3.646	-R$ 3.646
Atualização por INCC	R$ 0	R$ 3.646	-R$ 3.646
CUSTO TOTAL	R$ 98.485	R$ 94.571	R$ 3.915

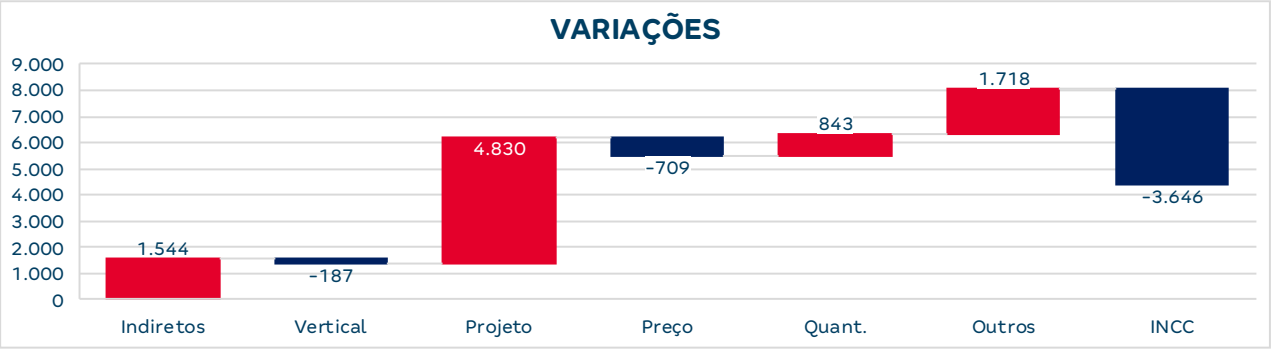

INDIRETOS
+1.710 | G11 Serviços Técnicos
-163 | G12 Gastos Gerais
+274 | G13 Pessoal Permanente
-208 | G14 Administração

VERTICAL
-187 | Retroalimentação

PROJETO
+1.101 | Extensão de rede de Hidráulica de 350m
+330 | Extensão de rede elétrica – Posteamento
+222 | Drenagem
+2.143 | Reserv. Metálico (1 castelo ⌀6,5m h40m – 3 castelos ⌀3,82m h 32,52m)
+190 | Muro
+643 | Fundação
+131 | Estrutura de concretp

PREÇO
-773 | Esq de Aluminio Torre
+175 | E.T.E.

QUANTIDADE
+1.012 | Telhado

OUTROS
+1.408 | Inst. Torre (SPK)
-237 | Inst. Infra
+207 | Louças e metais (melhoria de produto)
+500 | Pintura (melhoria de produto)

INCC
-3.646| Atualização de INCC

Custo de Construção

	PORTO LIMA REV01 CONSOLIDADO ENTRE COND. FASE ÚNICA	PORTO LIMA CEN04 | REV06.1 CONSOLIDADO
Torres	12	12
Unidades Construídas	280 | 160 | 320 | 160	280 | 160 | 320 | 160
Unidades Vendidas	276 | 158 | 315 | 158	276 | 158 | 315 | 158
Total Unidades Vendidas	907	907
Condomínios (qta.)	2	2
Cidade	Rio de Janeiro	Rio de Janeiro
Produto / Selo	F2 MODULAR	F2 MODULAR
Tipologia	09 Torre | T+4 | 16PP	09 Torre | T+4 | 16PP
Tipologia	2 Torre | T+4 | 12PP	2 Torre | T+4 | 12PP
Tipologia	1 Torre | T+04 | 16PP (L)	1 Torre | T+04 | 16PP (L)
Projeto Infra	AP	AP
Projeto Torre	AP	AP
Mês Base	janeiro-26	abril-25
Incc	1225,633	1178,386
LVS	novembro-25	fevereiro-25
Indiretos	novembro-25	fevereiro-25
Base de Preço	LPU 98	LPU 89
Takt	2+2	2+2
Prazo (mês)	12 | 13	11 | 9 | 12 | 9

CUSTO TOTAL I	R$ / UND R$ 90.061	R$ / UND R$ 88.561	DIF R$ 1.501
Indireto	R$ 18.505	R$ 21.077	-R$ 2.572
Torre	R$ 43.749	R$ 42.190	R$ 1.559
Infra	R$ 18.327	R$ 16.524	R$ 1.803
Fundação	R$ 5.644	R$ 5.010	R$ 634
EEE	R$ 143	R$ 248	-R$ 105
ETE	R$ 1.309	R$ 1.134	R$ 175
Contenção	R$ 41	R$ 0	R$ 41
Terrapplenagem	R$ 2.343	R$ 2.378	-R$ 34
CUSTO TOTAL II	R$ 4.033	R$ 2.365	R$ 1.668
Urbanização	R$ 1.721	R$ 1.553	R$ 168
Drenagem	R$ 591	R$ 521	R$ 70
Extensão de Rede Eletrica	R$ 364	R$ 34	R$ 330
Extensão de Rede Hidráulica	R$ 1.357	R$ 256	R$ 1.101
CUSTO TOTAL III	R$ 0	R$ 0	R$ 0
Incorridos	R$ 0	R$ 0	R$ 0
CUSTO TOTAL IV	R$ 0	R$ 0	R$ 0
Aprendizado	R$ 0	R$ 0	R$ 0
CUSTO TOTAL V	R$ 0	R$ 3.646	-R$ 3.646
Atualização por INCC	R$ 0	R$ 3.646	-R$ 3.646
CUSTO TOTAL	R$ 94.094	R$ 94.571	-R$ 476

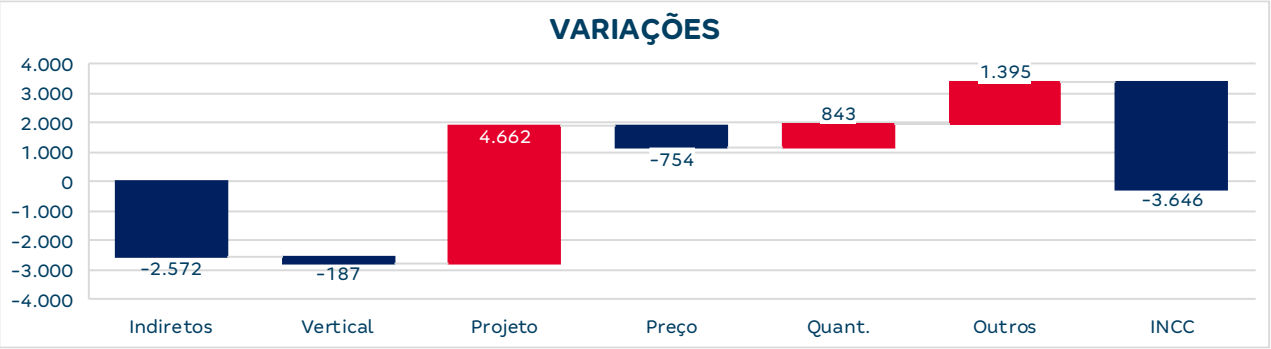

INDIRETOS
+1.555 | G11 Serviços Técnicos
-256 | G12 Gastos Gerais
+263 | G13 Pessoal Permanente
-1.767 | G14 Administração
-1.947 | G15 Implantação do Canteiro

VERTICAL
-187 | Retroalimentação

PROJETO
+1.101 | Extensão de rede de Hidráulica de 350m
+330 | Extensão de rede elétrica – Posteamento
+184 | Drenagem
+2.063 | Reserv. Metálico (1 castelo ⌀6,5m h40m – 3 castelos ⌀3,82m h 32,52m)
+189 | Muro
+634 | Fundação
+131 | Estrutura de concreto

PREÇO
-773 | Esq de Aluminio Torre
+175 | E.T.E.

QUANTIDADE
+1.012 | Telhado

OUTROS
+1.074 | Inst. Torre
-493 | Inst. Infra
+95 | Revest. Ceramico (melhoria de produto)
+207 | Louças e metais (melhoria de produto)
+500 | Pintura (melhoria de produto)

INCC
-3.646| Atualização de INCC

Operações

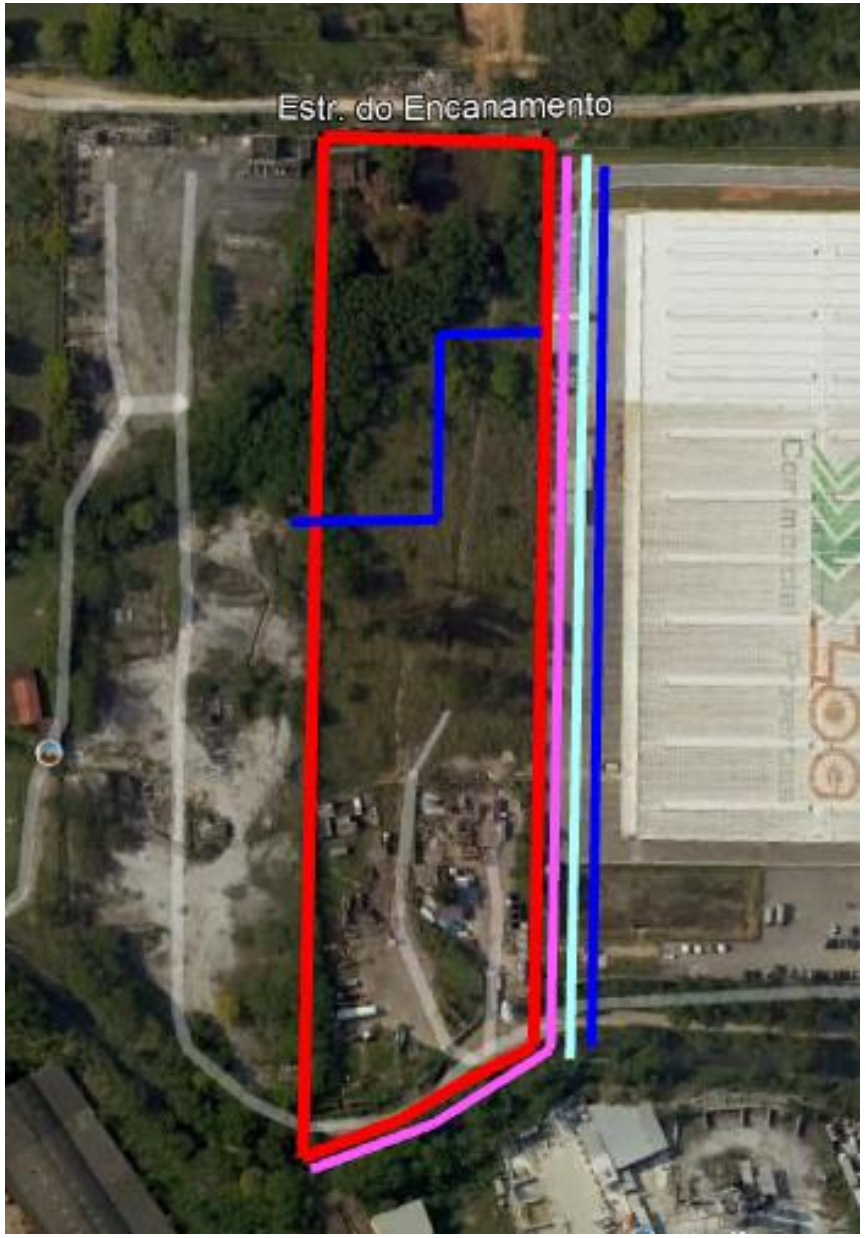

SISTEMA DE ABASTECIMENTO DE ÁGUA
Considerado extensão de 350m no cond. 02

SISTEMA DE ESGOTAMENTO SANITÁRIO
Viabilidade existente. Considerado ETE. Considerado custo de extensão de rede de esgoto no cond. 02.

SISTEMA DE DRENAGEM
Considerado extensão de 97 no cond. 02 FNA.

SISTEMA DE ABASTECIMENTO DE GÁS
Abastecimento por GLP.

SISTEMA DE ABASTECIMENTO ELÉTRICO
Existe viabilidade técnica. Considerado extensão de posteamento na rua nova a ser projetada.

TERRENO

URBANIZAÇÃO
Considerado rua de acesso ao Condomínio 2 (pavimentação, calçada e grama) e calçada na testada do Condomínio 1.

Operações

Matriz Risco Concessionária	
Água	Nível 1
Esgoto	Nível 1
Drenagem	Nível 2
Elétrica	Nível 3
Gás	NA
Urbanização	Nível 3

LEGENDA		
Nível	Tipo	Status
1	Com Diretriz	Conclusiva
2		Conclusiva com projeto aprovado
3		Conclusiva sem projeto aprovado
4		Não Conclusiva
5	Sem Diretriz	-
NA	-	Não aplicável

Água:
- Viabilidade Cond. 01 emitida em 23/09/2025, com validade de 24 meses. Viabilidade para 434u.h.
- Viabilidade Cond. 02 emitida em 23/09/2025, com validade de 24 meses. Viabilidade para 473u.h.

Esgoto:
- Viabilidade Cond. 01 emitida em 04/07/2022, Viabilidade para 500u.h.
- Viabilidade Cond. 02 emitida em 02/12/2025, Viabilidade para 473u.h.

Drenagem:
- DPEP existente. Considerado extensão projeto aprovado.

Elétrica:
- Viabilidade Cond. 01e 2 emitida em 27/06/2025, para 442 u.h com validade de 60 dias.

Gás:
- Empreendimento com GLP.

Urbanização:
- Considerado rua de acesso ao Condomínio 2 (pavimentação, calçada e grama) e calçada na testada do Condomínio 1. Enviado a PAA existente para esse terreno.

Fundação:
- Sendo Realizada 2ª campanha de sondagem contemplando 11 furos.
- Considerada Radier e Estaca Hélice, com diâmetros de 40 e 50 e profundidade de 9 m.

Logística

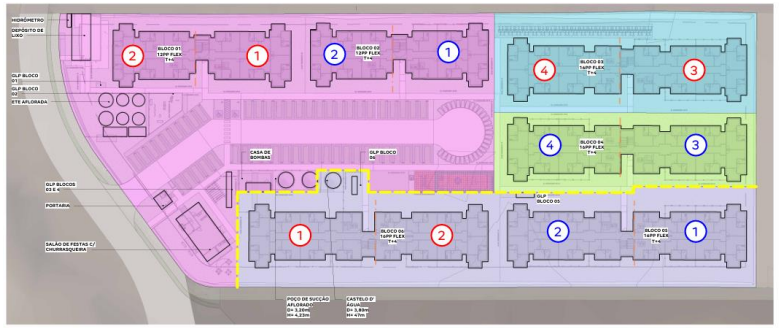

MODULAÇÃO E TOMBAMENTO
1 : 500

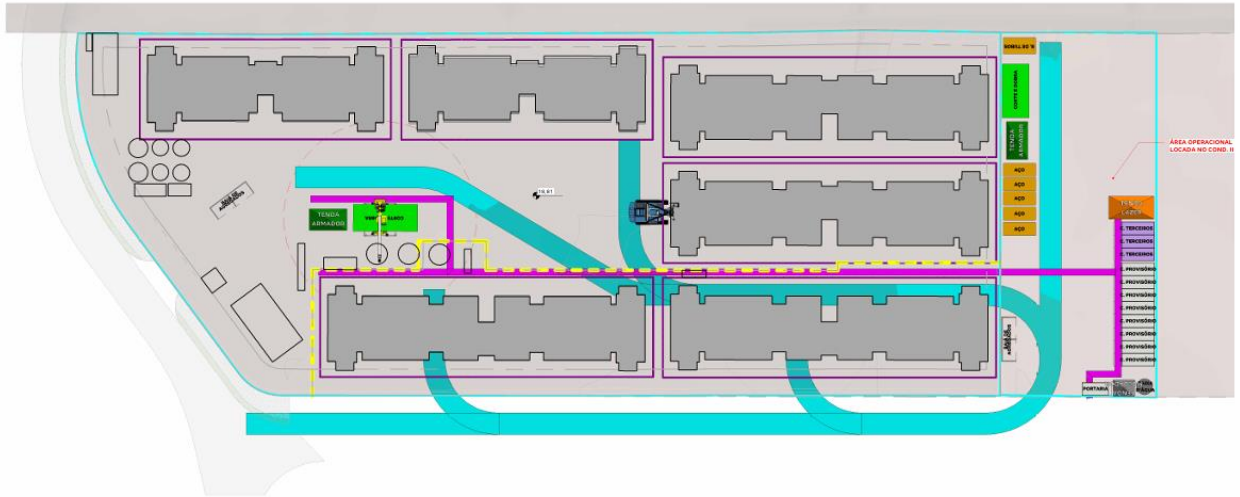

PRÉ FORMA
1 : 500

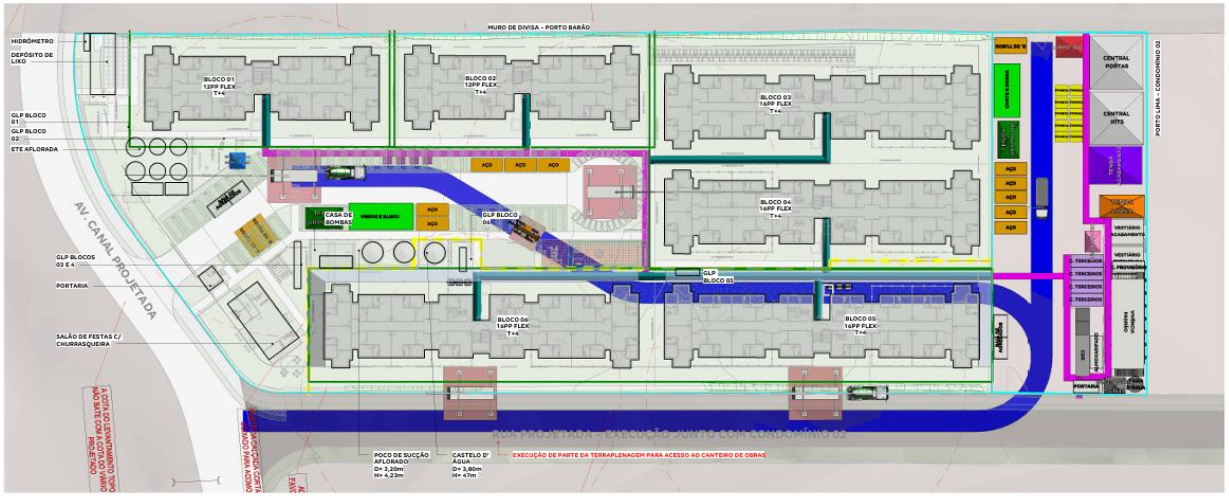

ESTRUTURA E ACABAMENTO
1 : 500

VIVÊNCIA - CONTAINERS

DESCRIÇÃO	QUANTIDADE	TAMANHO MÓDULOS	MOBILIZAÇÃO	DESMOBILIZAÇÃO	PRÉ FORMA	ESTRUTURA	ACAB.	FASE
CONTAINER ALMOXARIFADO (LOG)	1 MÓDULO DE CONTAINER	2,41 X 6,10 m	1 MOBILIZAÇÃO	1 DESMOBILIZAÇÃO	-	TODO PERÍODO	TODO PERÍODO	FASE 01 E 02
CONTAINER PORTARIA (LOG)	CONSIDERAR 1 MÓDULO COM SANITÁRIO E CATRACA	2,41 X 4,90 m	1 MOBILIZAÇÃO	1 DESMOBILIZAÇÃO	TODO PERÍODO	** AJUSTAR	** AJUSTAR	FASE 01 E 02
CONTAINER PROVISÓRIO (LOG)	CONSIDERAR 8 MÓDULOS DE CONTAINER	2,41 X 6,10 m	1 MOBILIZAÇÃO	1 DESMOBILIZAÇÃO	TODO PERÍODO	-	-	FASE 01 E 02
CONTAINER VESTIÁRIO ACABAMENTO (LOG)	CONSIDERAR 2 MÓDULOS DE CONTAINER	2,41 X 6,10 m	1 MOBILIZAÇÃO	1 DESMOBILIZAÇÃO	-	-	TODO PERÍODO	FASE 01 E 02
CONTAINER VESTIÁRIO ESTRUTURA (LOG)	CONSIDERAR 2 MÓDULOS DE CONTAINER (EQUIPE VERTICAL)	2,41 X 6,10 m	1 MOBILIZAÇÃO	1 DESMOBILIZAÇÃO	-	TODO PERÍODO	-	FASE 01 E 02
CONTAINER VIVÊNCIA PADRÃO (LOG)	CONSIDERAR 14 MÓDULOS COM 2 ESCADAS (7 MÓDULOS NO PAV. T E 7 MÓDULOS NO PAV SUPERIOR)	2,41 X 6,10 m	1 MOBILIZAÇÃO	1 DESMOBILIZAÇÃO	-	TODO PERÍODO	TODO PERÍODO	FASE 01 E 02

TENDAS_PERÍODOS

DESCRIÇÃO	QUANTIDADE	LARGURA	COMPRIMENTO	PRÉ FORMA	ESTRUTURA	ACABAMENTO	FASE
GAIOLA DE DESMOLDANTE (LOG)	1	4,00	6,00	-	TODO PERÍODO	-	FASE 01 E 02
GAIOLA DE INFLAMÁVEIS (LOG)	1	3,00	4,00	-	TODO PERÍODO	TODO PERÍODO	FASE 01 E 02
TENDA ACABAMENTO (LOG)	1	9,98	7,07	-	TODO PERÍODO	TODO PERÍODO	FASE 01 E 02
TENDA ARMADOR (LOG)	2	4,00	7,00	TODO PERÍODO	TODO PERÍODO	-	FASE 01 E 02
TENDA BANHEIRO QUÍMICO E BEBEDOURO (LOG)	1	3,00	3,00	-	TODO PERÍODO	TODO PERÍODO	FASE 01 E 02
TENDA CENTRAL DE KITS (LOG)	1	10,00	10,00	-	TODO PERÍODO	TODO PERÍODO	FASE 01 E 02
TENDA CENTRAL DE PORTAS (LOG)	1	10,00	10,00	-	TODO PERÍODO	TODO PERÍODO	FASE 01 E 02
TENDA LAZER (LOG)	1	4,26	8,37	-	TODO PERÍODO	TODO PERÍODO	FASE 01 E 02
TENDA MOLDADOR (LOG)	1	3,00	4,00	TODO PERÍODO	TODO PERÍODO	-	FASE 01 E 02

EQUIPAMENTOS E MAQUINÁRIOS

EQUIPAMENTO	QUANTIDADE	MOBILIZAÇÃO	DESMOBILIZAÇÃO	PRÉ FORMA	ESTRUTURA	ACABAMENTO	FASE
BETONEIRA (LOG)	VARIÁVEL	-	-	TODO PERÍODO	TODO PERÍODO	-	FASE 01 E 02
BOMBA LANÇA (LOG)	VARIÁVEL	-	-	TODO PERÍODO	TODO PERÍODO	-	FASE 01 E 02
CAMINHÃO MUNCK (LOG)	1 EQUIPAMENTO PARA CADA FASE	1 MOBILIZAÇÃO	1 DESMOBILIZAÇÃO	-	CONSIDERAR MEIO PERÍODO DE ESTRUTURA	-	FASE 01 E 02
GUINDASTE (LOG)	1 EQUIPAMENTO PARA IÇAMENTO DOS CASTELOS	1 MOBILIZAÇÃO	1 DESMOBILIZAÇÃO	-	-	-	FASE 01 E 02
PERFURATRIZ (LOG)	1 EQUIPAMENTO PARA CADA FASE	1 MOBILIZAÇÃO	1 DESMOBILIZAÇÃO	CONSIDERAR PERÍODO DE ESTACA CONFORME PROJETO.	-	-	FASE 01 E 02
SKYTRAK (LOG)	1 EQUIPAMENTO PARA CADA FASE	1 MOBILIZAÇÃO	1 DESMOBILIZAÇÃO	-	TODO PERÍODO	CONSIDERAR 15 DIAS DO PERÍODO DE ACABAMENTO	FASE 01 E 02

Logística

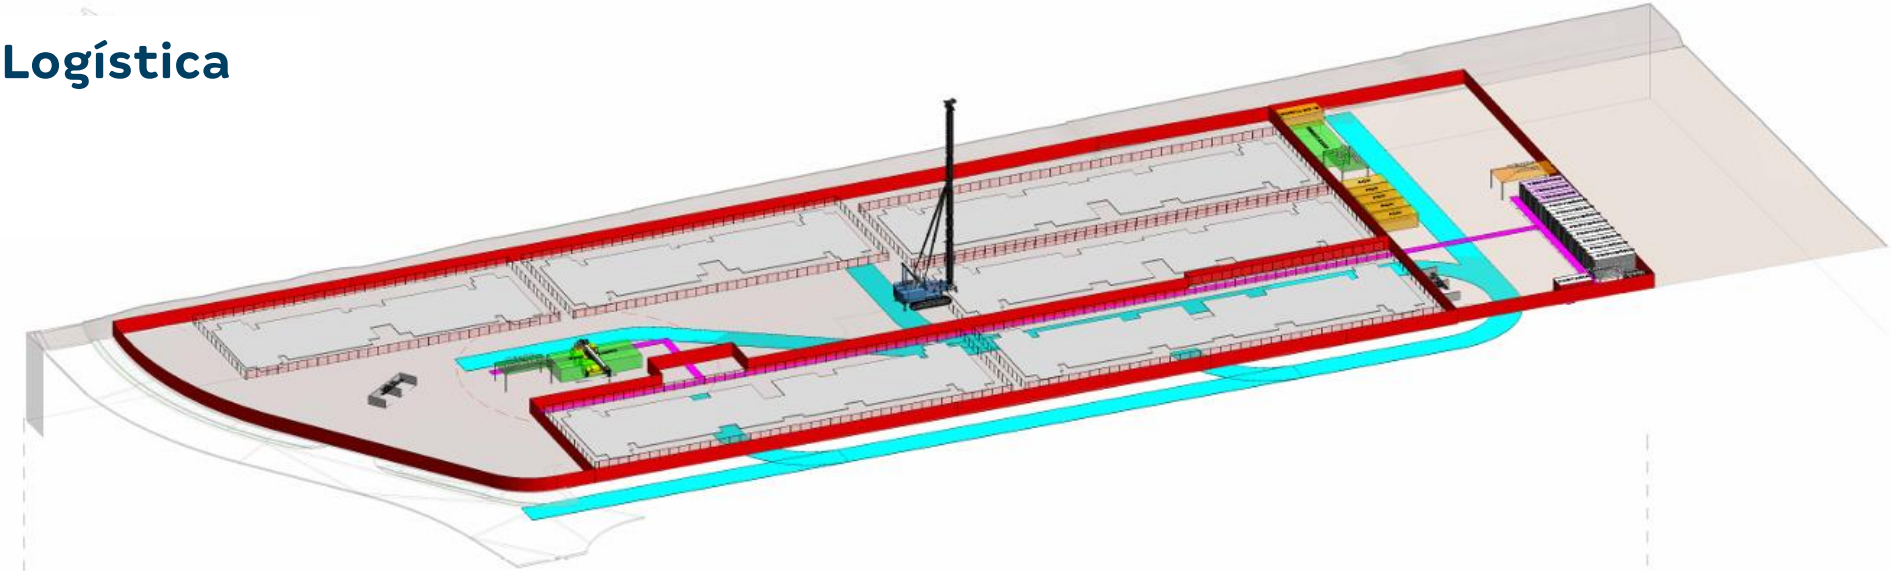

VISTA 3D - PRÉ FORMA

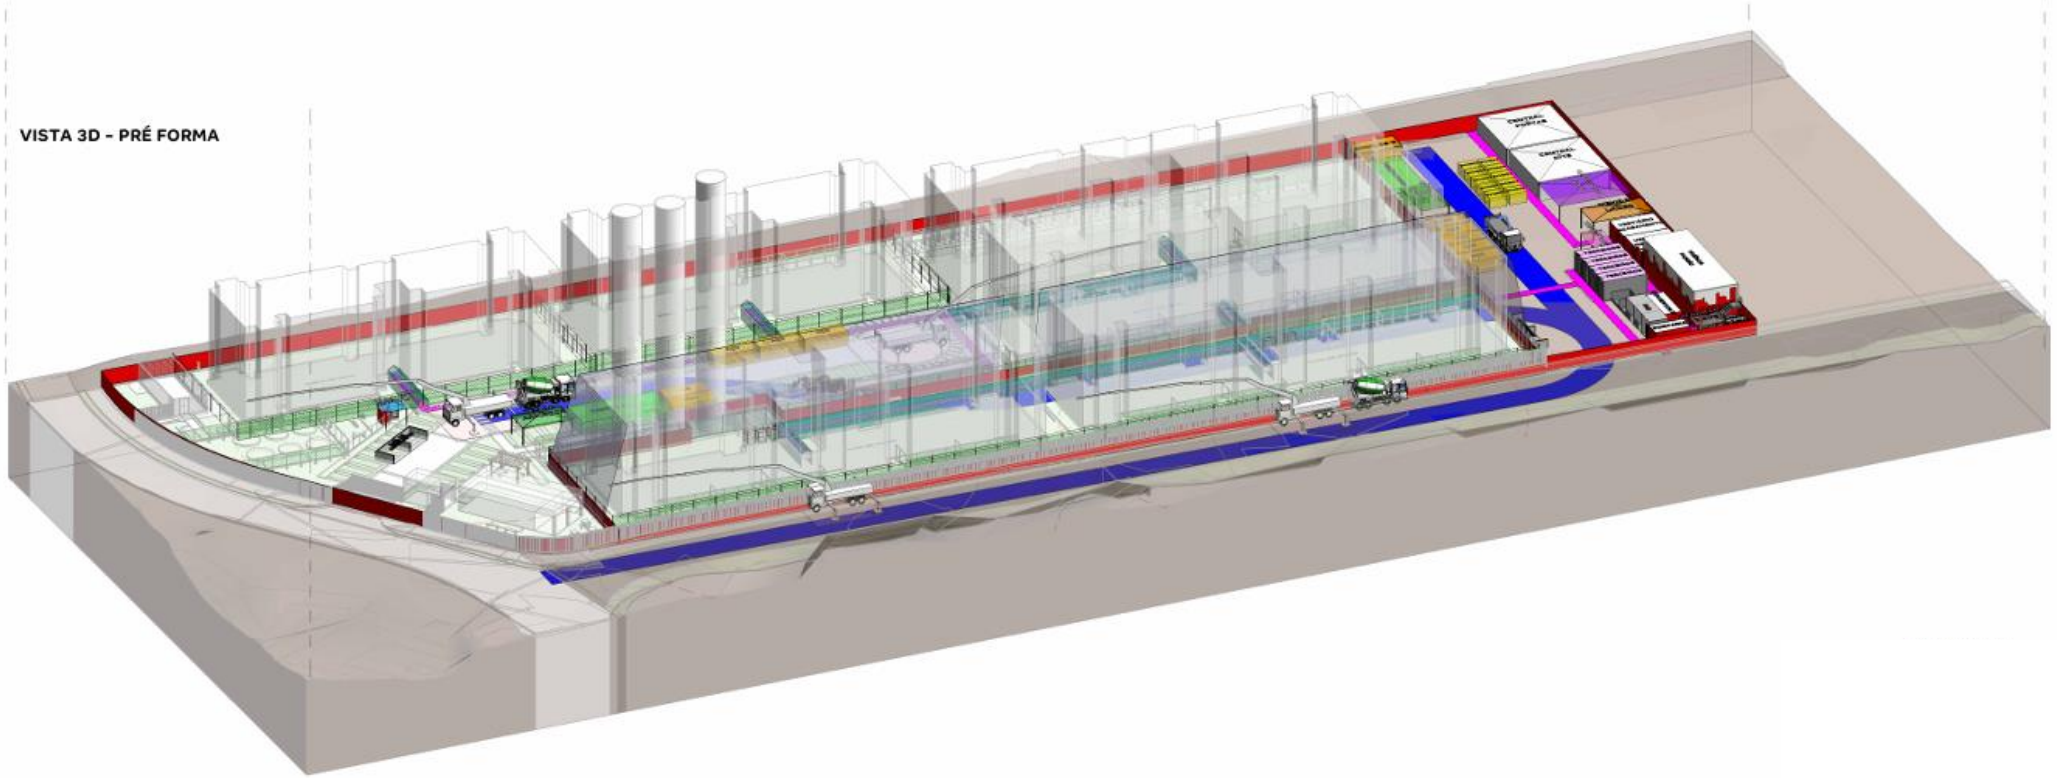

VISTA 3D - ESTRUTURA E ACABAMENTO

Logística

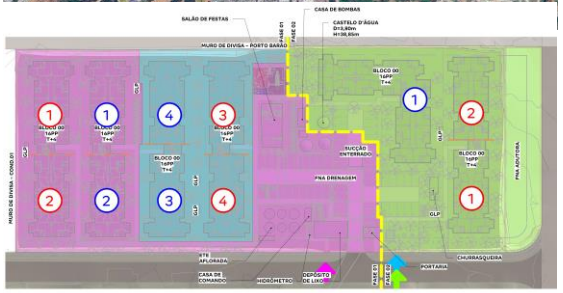

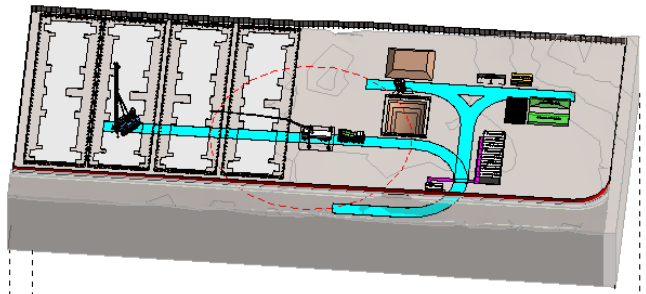

VISTA 3D - PRE FORMA-F1

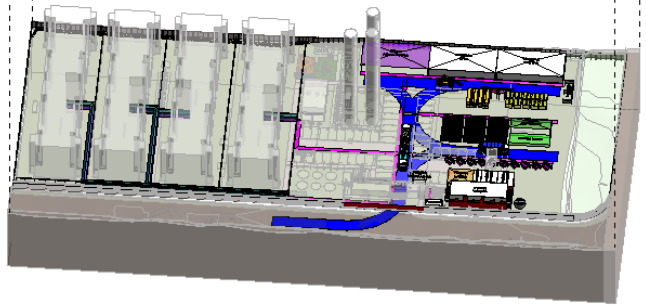

VISTA 3D - ESTRUTURA E ACABAMENTO-F1

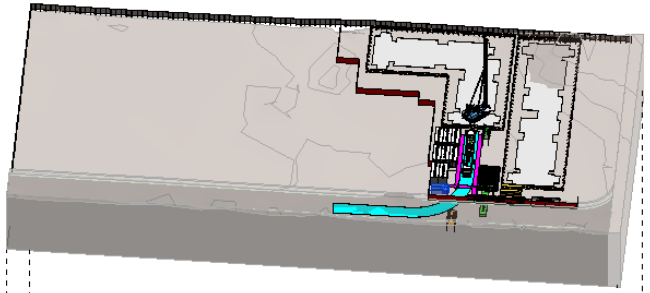

VISTA 3D - PRE FORMA-F2

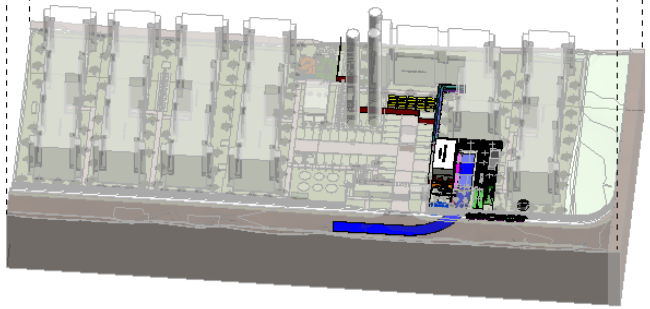

VISTA 3D - ESTRUTURA E ACABAMENTO-F2

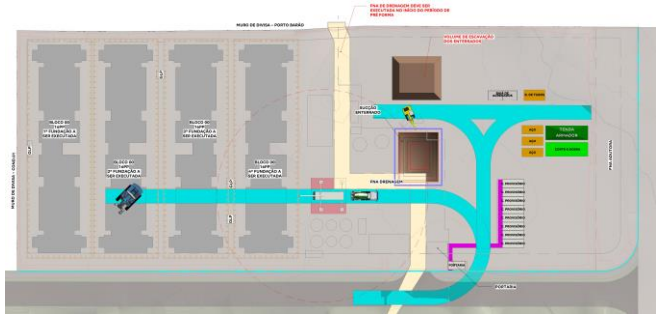

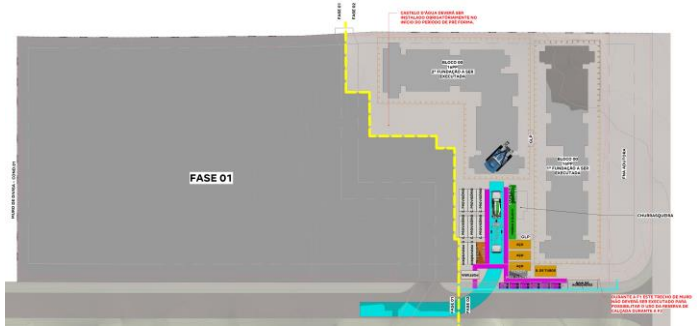

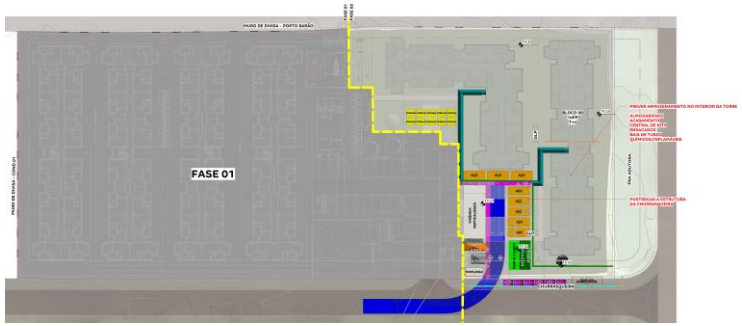

VIVENCIA - CONTAINERS									
DESCRIÇÃO	QUANTIDADE	TAMANHO MÓDULOS	MOBILIZAÇÃO	DESMOBILIZAÇÃO	PRÉ FORMA	ESTRUTURA	ACAB.	FASE	CÓDIGO ORÇAMENTO
CONTAINER ALMOXARIFADO (LOG)	1 MÓDULO DE CONTAINER	2,41 X 6,10 m	1 MOBILIZAÇÃO	1 DESMOBILIZAÇÃO	-	TODO PERÍODO	TODO PERÍODO	F1	
CONTAINER PORTARIA (LOG)	CONSIDERAR 1 MÓDULO COM SANITÁRIO E CATRACA	2,41 X 4,90 m	1 MOBILIZAÇÃO	1 DESMOBILIZAÇÃO	TODO PERÍODO	TODO PERÍODO	TODO PERÍODO	F1	
CONTAINER PORTARIA (LOG)	CONSIDERAR 1 MÓDULO COM SANITÁRIO E CATRACA	2,41 X 4,90 m	1 MOBILIZAÇÃO	1 DESMOBILIZAÇÃO	TODO PERÍODO	TODO PERÍODO	TODO PERÍODO	F2	
CONTAINER PROVISÓRIO (LOG)	CONSIDERAR 8 MÓDULOS DE CONTAINER	2,41 X 6,10 m	1 MOBILIZAÇÃO	1 DESMOBILIZAÇÃO	TODO PERÍODO	-	-	F1	
CONTAINER PROVISÓRIO (LOG)	CONSIDERAR 8 MÓDULOS DE CONTAINER	2,41 X 6,10 m	1 MOBILIZAÇÃO	1 DESMOBILIZAÇÃO	TODO PERÍODO	-	-	F2	
CONTAINER VESTIÁRIO ACABAMENTO (LOG)	CONSIDERAR 2 MÓDULOS DE CONTAINER	2,41 X 6,10 m	1 MOBILIZAÇÃO	1 DESMOBILIZAÇÃO	-	-	TODO PERÍODO	F1	
CONTAINER VESTIÁRIO ESTRUTURA (LOG)	CONSIDERAR 2 MÓDULOS DE CONTAINER (EQUIPE VERTICAL)	2,41 X 6,10 m	1 MOBILIZAÇÃO	1 DESMOBILIZAÇÃO	-	TODO PERÍODO	-	F1	
CONTAINER VIVÊNCIA PADRÃO (LOG)	CONSIDERAR 14 MÓDULOS COM 2 ESCADAS (7 MÓDULOS NO PAV. T E 7 MÓDULOS NO PAV SUPERIOR)	2,41 X 6,10 m	1 MOBILIZAÇÃO	1 DESMOBILIZAÇÃO	-	TODO PERÍODO	TODO PERÍODO	F1	
CONTAINER VIVÊNCIA VERTICALIZADA (LOG)	CONSIDERAR 17 MÓDULOS DE CONTAINERS E 1 ESCADA PARA ACESSO (SENDO 6 NO PAV T., 6 NO PAV 1 E 5 NO ULTIMO PAV.)	2,41 X 6,10 m	1 MOBILIZAÇÃO	1 DESMOBILIZAÇÃO	-	TODO PERÍODO	TODO PERÍODO	F2	

TENDAS_PERIODOS								
DESCRIÇÃO	QUANTIDADE	LARGURA	COMPRIMENTO	PRÉ FORMA	ESTRUTURA	ACABAMENTO	FASE	CÓDIGO ORÇAMENTO
GAIOLA DE DESMOLDANTE (LOG)	1	2,00	2,00	-	TODO PERÍODO	-	F1/F2	
GAIOLA DE INFLAMÁVEIS (LOG)	1	2,00	2,00	-	TODO PERÍODO	TODO PERÍODO	F1/F2	
TENDA ACABAMENTO (LOG)	1	10,00	20,00	-	TODO PERÍODO	TODO PERÍODO	F1	
TENDA ARMADOR (LOG)	4	<varia>	<varia>	TODO PERÍODO	TODO PERÍODO	-	F1/F2	
TENDA CENTRAL DE KITS (LOG)	1	10,00	20,00	-	TODO PERÍODO	TODO PERÍODO	F1	
TENDA CENTRAL DE PORTÃS (LOG)	1	10,00	20,00	-	TODO PERÍODO	TODO PERÍODO	F1	
TENDA LAZER (LOG)	3	<varia>	<varia>	-	TODO PERÍODO	TODO PERÍODO	F1/F2	
TENDA MOLDADOR (LOG)	3	<varia>	<varia>	TODO PERÍODO	TODO PERÍODO	-	F1/F2	

LOG_EQUIPAMENTOS E MAQUINÁRIOS								
EQUIPAMENTO	QUANTIDADE	MOBILIZAÇÃO	DESMOBILIZAÇÃO	PRÉ FORMA	ESTRUTURA	ACABAMENTO	FASE	CÓDIGO ORÇAMENTO
BETONEIRA (LOG)	VARIAVEL	-	-	TODO PERÍODO	TODO PERÍODO	-	F1/F2	
BOMBA ESTACIONÁRIA PADRÃO (LOG)_R01	1 EQUIPAMENTO	-	-	-	TODO PERÍODO	-	F1/F2	
BOMBA LANÇA (LOG)	VARIAVEL	-	-	TODO PERÍODO	TODO PERÍODO	-	F1	
ESCAVADEIRA (LOG)							F1/F2	
PERFURATRIZ (LOG)	1 EQUIPAMENTO	1 MOBILIZAÇÃO	1 DESMOBILIZAÇÃO	CONSIDERAR PERÍODO DE ESTACA CONFORME PROJETO.	-	-	F1/F2	
SKYTRAK (LOG)	1 EQUIPAMENTO	1 MOBILIZAÇÃO	1 DESMOBILIZAÇÃO	-	TODO PERÍODO	CONSIDERAR 15 DIAS DO PERÍODO DE ACABAMENTO	F1/F2	

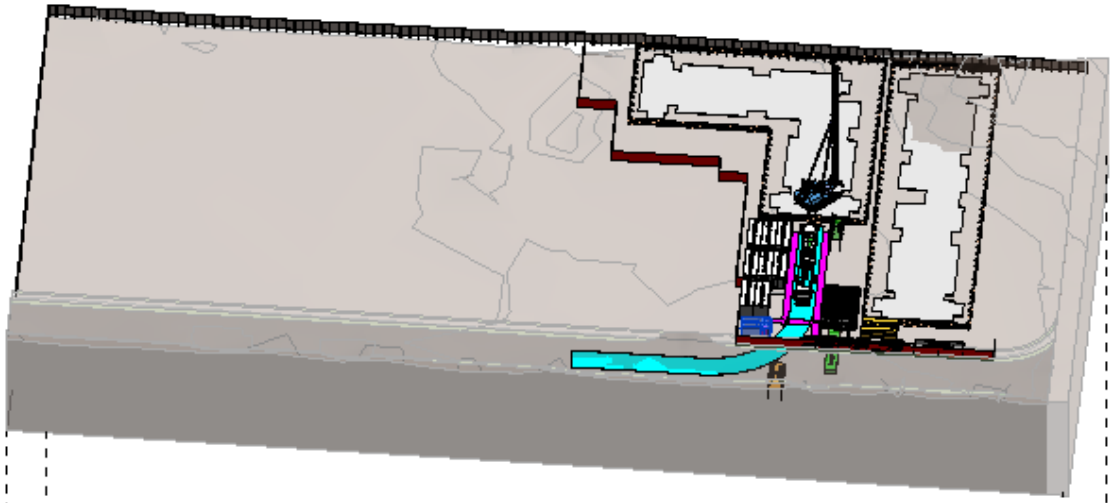

VISTA 3D - PRE FORMA-F2

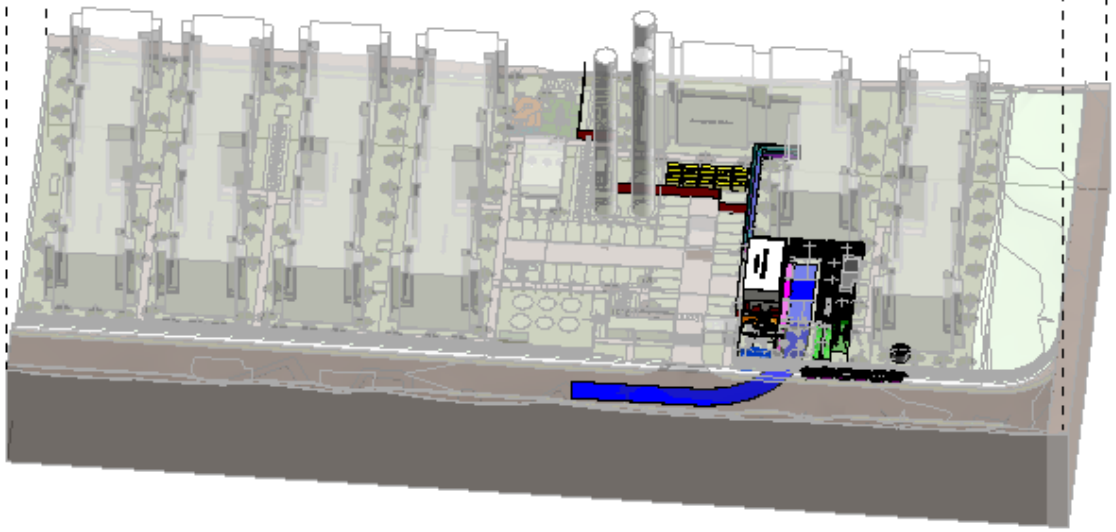

VISTA 3D - ESTRUTURA E ACABAMENTO-F2

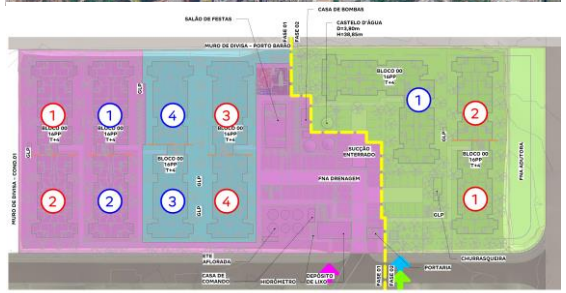

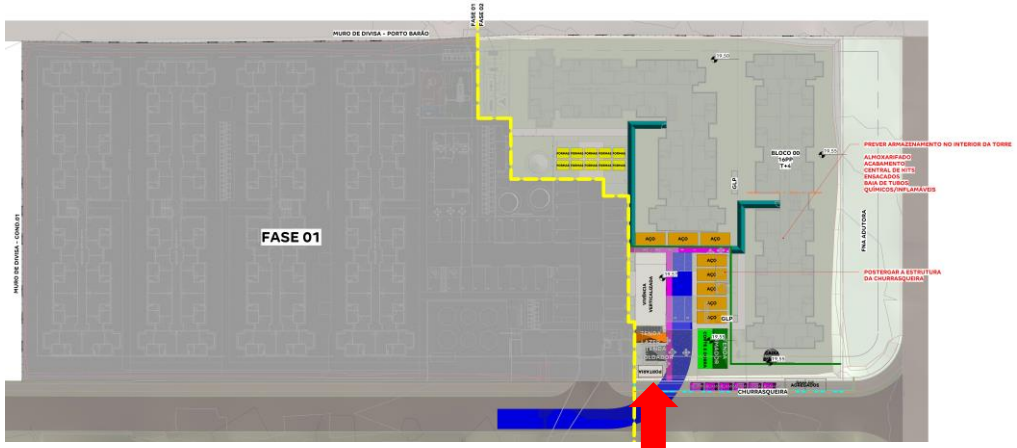

OBS.: 01

➢ OBS. 01	DEVIDO AO ESPAÇO OPERACIONAL LIMITADO, PREVER CUSTOS COM VIVÊNCIA VERTICALIZADA NA FASE 02.
➢ OBS. 02	FNA DE DRENAGEM DEVERÁ SER EXECUTADA NO INÍCIO DO PERÍODO DE PRÉ FORMA.

Pareceres

Análise da Mancha e Implantação

Prospecção

Operações

Inteligência de Mercado

Financeiro

Demanda e Distribuição da Mancha

Potencial de Demanda			Lançados		Lanç + Landbank	
Mancha	CÓD.	Shr.	ANO	MÊS	ANO	MÊS
Rio de Janeiro Oeste 1/6	RZO 1/6	40%	1.664	139	1.997	166

Faixas MCMV	Empreendimento	Renda	Lançamento	mar/26	abr/26	mai/26	jun/26	jul/26	ago/26	set/26	out/26	nov/26	dez/26	jan/27	fev/27	mar/27	abr/27	mai/27	jun/27	jul/27	ago/27	set/27	out/27	nov/27	dez/27
Faixa 1	**Porto Lima**	**2.584**	**mar-26**		**33**	**33**	**33**	**33**	**33**	**33**	**33**	**33**	**33**	**33**	**33**	**33**	**33**								
Faixa 1	**Porto Seleta**	**2.584**	**abr-27**															**36**	**36**	**36**	**36**	**36**	**36**	**36**	**36**
Total de Vendas Lançados				**0**	**0**	**0**	**0**	**0**	**0**	**0**	**0**	**0**	**0**	**0**	**0**	**0**	**0**	**0**	**0**	**0**	**0**	**0**	**0**	**0**	**0**
Total de Vendas Lançados + Landbank				**0**	**33**	**33**	**33**	**33**	**33**	**33**	**33**	**33**	**33**	**33**	**33**	**33**	**33**	**36**	**36**	**36**	**36**	**36**	**36**	**36**	**36**
Total Mancha | Faixa 1					*100%*	*100%*	*100%*	*100%*	*100%*	*100%*	*100%*	*100%*	*100%*	*100%*	*100%*	*100%*	*100%*	*100%*	*100%*	*100%*	*100%*	*100%*	*100%*	*100%*	*100%*
Total Mancha | Faixa 2					*0%*	*0%*	*0%*	*0%*	*0%*	*0%*	*0%*	*0%*	*0%*	*0%*	*0%*	*0%*	*0%*	*0%*	*0%*	*0%*	*0%*	*0%*	*0%*	*0%*	*0%*
Total Mancha | Faixa 3					*0%*	*0%*	*0%*	*0%*	*0%*	*0%*	*0%*	*0%*	*0%*	*0%*	*0%*	*0%*	*0%*	*0%*	*0%*	*0%*	*0%*	*0%*	*0%*	*0%*	*0%*

Parecer de I.M sobre a mancha:

O projeto analisado em comitê está em linha com o potencial teórico de demanda calculado para a mancha. (Total Lançados)

Canibalização:

Sem Risco de Canibalização

Porto Lima | Mapa Concorrência

		Porto Lima	Varandas Mendanha
		TENDA	Engefic
	Distância Tenda (km)		1,61
Região 1 Km	População	7.329	23.945
	Dens. Demográfica	2.347	7.671
	Renda (R$)	5.265	6.834
	Classe Social	C1 (de R$ 3.1K a 5.4K)	B2 (de R$ 5.4K a 9.8K)
	PEA Dia	6.772	12.122
Quantitativo	Lançamento	mar/26	jul/25
	Unidades	434	320
	Estoque	434	106
	VSO	33	36
	Stockout	13	3
Qualitativo	Condomínios	1	1
	Torres	6	6
	Gabarito	T+4	T+4
	Plantas (m²)	34,1m²	44,6m² - 70,1m²
	Tipologia	2 Dorms	2 Dorms
	Opções	Não	Garden
	Varanda	Não	Sim
	Vagas	12%	Rotativa
	Lazer	Bicicletário, Playpet, playkids, praça de chegada, mini quadra, espaço ducha, salão de festas com churrasqueira gourmet, fitness externo, 6 unidades de lazer interno com sugestão de Mini market	Mini Market, Bicicletário, Piscina, Churrasqueira, Salão de Festas, Espaço Conveniência, Quadra, Espaço Fitness, Brinquedoteca, Playground, Pet Place

Farol Renda
Acima de 300
Entre 0 e 300
Abaixo de 0

Diagnóstico Concorrência

- A concorrência possui target de preço e renda acima ao previsto para o Porto Lima.

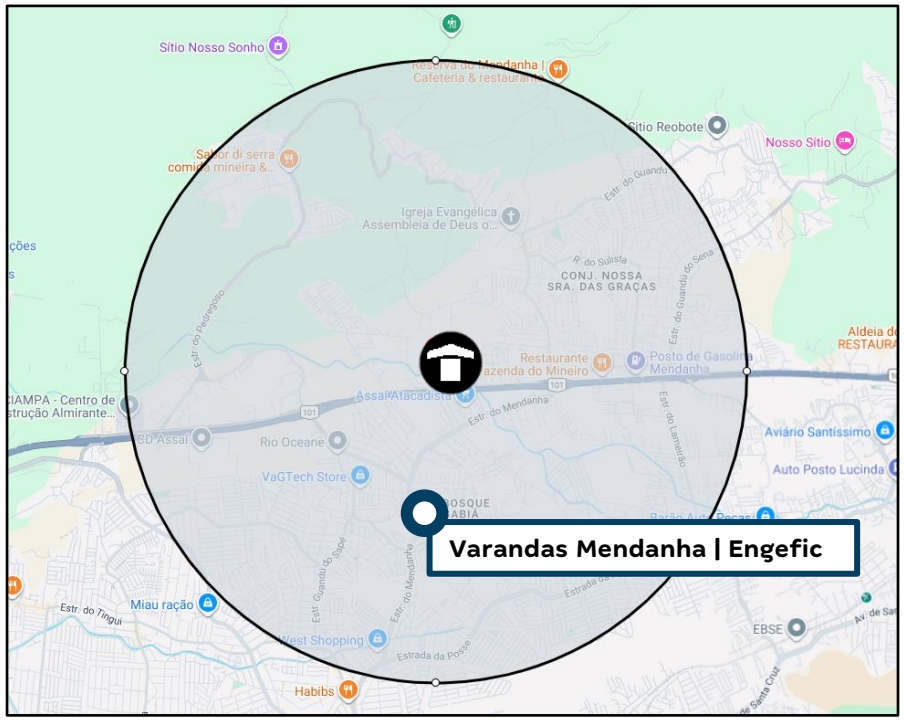

-	Porto Lima					Varandas Mendanha					
Tipologias	Avaliação	Preço Nominal	CEF	Renda	% Unidades	Avaliação	Preço Nominal	CEF	Renda	Dif	Farol
Uh tipo	201.000	211.999	171.315	2.521	88%	264.000	244.000	211.200	5.171	2.650	●
Vg Carro	214.000	224.989	177.262	3.043	12%	-	-	-	-	-	-

Informações Viabilidade

Projeto:	Porto Lima			
Tipo:	Uh tipo		Uh tipo	
Método	**Ref - Porto Valencia**		**Vision**	
Avaliação	201.000		201.000	
Renda Inicial (VF)	2.544		2.521	
Renda Final*	-		-	
% RET1	75%		75%	
Tipo:	**VF**	**R$**	**VF**	**R$**
Ato	0,45	1.149	0,53	1.355
FGTS	0,09	226	0,57	1.452
Financiamento	95,00%	146.873	95,53%	146.587
Subsídio	132,39%	25.776	115,22%	23.277
Prazo de Pró-soluto	17	17	17	17
Pró-Soluto	79,51%	12.495	94,78%	14.759
Preço Raso (RS)	186.519	186.519	187.429	187.429
TCD	85,38%	21.895	96,68%	24.569
VSO	29	29	29	29
Preço de Venda	**206.448**	**206.448**	**209.999**	**209.999**
Elasticidade	0,952%	0,952%	0,952%	0,952%
Preço de Venda Final	**208.414**	**208.414**	**211.999**	**211.999**
Preço Raso (R$)	**186.519**		**187.429**	
% de Raso	**89,49%**		**88,41%**	
BP25 - Não Inflacionado	**-**		**-**	
BP25 - Inflacionado	**-**		**-**	

Informações Viabilidade

Projeto:	Porto Lima			
Tipo:	**Vg Carro**		**Vg Carro**	
Método	**Ref - Porto Valencia**		**Vision**	
Avaliação	214.000		214.000	
Renda Inicial (VF)	3.144		3.043	
Renda Final*	-		-	
% RET1	50%		50%	
Tipo:	**VF**	**R$**	**VF**	**R$**
Ato	0,56	1.790	0,72	2.213
FGTS	1,10	3.488	1,03	3.153
Financiamento	94,71%	161.665	97,29%	166.048
Subsídio	236,03%	14.603	104,67%	8.061
Prazo de Pró-soluto	17	17	17	17
Pró-Soluto	102,00%	19.805	102,90%	19.341
Preço Raso (RS)	201.352	201.352	198.816	198.816
TCD	58,37%	18.494	85,33%	26.173
VSO	4	4	4	4
Preço de Venda	**217.772**	**217.772**	**222.867**	**222.867**
Elasticidade	0,952%	0,952%	0,952%	0,952%
Preço de Venda Final	**219.846**	**219.846**	**224.989**	**224.989**
Preço Raso (R$)	**201.352**		**198.816**	
% de Raso	**91,59%**		**88,37%**	
BP25 - Não Inflacionado	**-**		**-**	
BP25 - Inflacionado	**-**		**-**	

Análise de Preço

Informações Viabilidade

Projeto:	Porto Lima
Tipo:	**Faixa 2**
Método	**Vision**
Avaliação	202.558
Renda Inicial (VF)	2.584
Renda Final*	-

Tipo:	VF	R$
Ato	0,55	1.458
FGTS	0,63	1.656
Financiamento	95,74%	148.918
Subsídio	113,96%	21.454
Prazo de Pró-soluto	17	17
Pró-Soluto	95,76%	15.308
Preço Raso (RS)	188.794	188.794
TCD	95,32%	24.761
VSO	33	33
Preço de Venda	**211.521**	**211.521**
Elasticidade	0,952%	0,952%
Preço de Venda Final	**213.555**	**213.555**
Preço Raso (R$)	**188.794**	
% de Raso	**88,41%**	
Raso Todas as Fases	**187.792**	
Nominal Todas as Fases	**212.360**	

1

Análise de Riscos	Farol IM
IM avalia o Preço Vision como **factível**.	

1) I.M está de acordo com o preço Vision, considerando que o empreendimento está inserido em uma região de renda média baixa, com oferta limitada de polos de serviços. Ainda assim, conta com um importante diferencial de mobilidade, o fácil acesso à Avenida Brasil, via que conecta o bairro aos principais pontos de interesse da cidade.

O Porto Lima tem como referência direta o Porto Valência. Nesse contexto, o preço estimado pelo Vision se mostra adequado, pois posiciona as unidades em linha com o patamar praticado por esse empreendimento de referência.

Adicionalmente, o projeto mantém um posicionamento de preço acessível, sendo o mais competitivo frente aos concorrentes diretos da região.

	Preço Real					Preço Normalizado (17m)	
	Avaliação	Preço Raso	Renda Mediana	VSO	PSOL	Δ PSOL	Preço Raso
Porto Valência F1	202.950	173.121	2.549	35	4	13.858	186.979
Parque Hortência	196.150	183.660	2.412	25	17	0	183.660
Porto Lima	202.558	188.794	2.584	33	17	-	188.794

Resumo de Preços

Vision

Nome Fase	Tipologia	Renda	Ato	FGTS	Cond.	Subsídio	PSOL	TCD	VSO	Nom. Pré	Avali.	Elast.	Nom. Pós	Raso Pós	PSOL (m)	RET1
Porto Seleta	Uh tipo	2.521	0,53	0,57	95,5%	115,2%	93,4%	95,3%	32,46	210.859	201.000	-0,4762%	209.854	185.633	18	75%
Porto Seleta	Vg Carro	3.043	0,72	1,03	97,3%	104,7%	101,4%	84,1%	3,923	223.994	214.000	-0,4762%	222.927	197.124	18	50%

Análise de Preço – Parecer Ciclo

Informações Viabilidade

Projeto:	Porto Lima
Tipo:	**Faixa 2**
Método	**Vision**
Avaliação	202.558
Renda Inicial (VF)	2.584
Renda Final*	-

Tipo:	VF	R$
Ato	0,55	1.458
FGTS	0,63	1.656
Financiamento	95,74%	148.918
Subsídio	113,96%	21.454
Prazo de Pró-soluto	17	17
Pró-Soluto	95,76%	15.308
Preço Raso (RS)	188.794	188.794
TCD	95,32%	24.761
VSO	33	33
Preço de Venda	**211.521**	**211.521**
Elasticidade	0,952%	0,952%
Preço de Venda Final	**213.555**	**213.555**

1

Preço Raso (R$)	**188.794**
% de Raso	**88,41%**
Raso Todas as Fases	**187.792**
Nominal Todas as Fases	**212.360**

Análise de Riscos	Farol IM
Ciclo avalia o Preço Vision como **factível**.	

- Pareceres
- Análise da Mancha e Implantação
- Prospecção
- Operações
- Inteligência de Mercado
- Financeiro

Informações Gerais – Consolidado

Porto Lima + Porto Seleta – RJ – Rio de Janeiro Capital

Datas e Prazos

	Compra	Lançamento	Início Obra	Término Obra	LÇTO até IO	IO até TO	Chaves	LÇTO até Chaves
Consolidado	out-23							
Porto Lima s/ vaga		mar-26	set-26	set-27	6 meses	12 meses	mar-29	36 meses
Porto Lima c/ vaga		mar-26	set-26	set-27	6 meses	12 meses	mar-29	36 meses
Porto Seleta s/ vaga		abr-27	out-27	nov-28	6 meses	13 meses	abr-30	36 meses
Porto Seleta c/ vaga		abr-27	out-27	nov-28	6 meses	13 meses	abr-30	36 meses

Terreno e Incorridos

TOTAL (R$ + Perm.):	8,50 MM	**Incorrido Terreno:**	0,70 MM	**Área do Terreno (100%):**	23.010 m²
Cash:	8,50 MM	**Nº de Parcelas Cash :**	44	**Custo de terreno m²:**	369,4
Permuta Financeira:	0,00 MM (0,00%)			**VaR 26 (R$ mil):**	1.334
Permuta Física:	0,00 MM (0,00%)			**VaR 27 (R$ mil):**	0
Ato / %VGV:	4,25 MM / 2,2%			**Incorrido de Construção:**	0,03 MM

Área Líquida do Terreno:	22.905 m²
Custo de terreno m² Área Líquida:	371,1
Fração Terreno/Terreno + Custo Obra (%VGV):	4,4% / 48,7%
CA Máx/Proj.	3,0 / 1,6
Incorridos de Incorporação:	0,74 MM

Vendas

Fases	Nº Pavimentos	Preço Raso Unit.	Qtde	Preço Unit.	Aval. CEF	Cond. Parcela	% Pró-soluto	% TCD
Porto Lima s/ vaga	T+4	187.429	381	211.999	201.000	95,5%	94,8%	96,7%
Porto Lima c/ vaga	T+4	198.816	53	224.989	214.000	97,3%	102,9%	85,3%
Porto Seleta s/ vaga	T+4	185.633	422	209.854	201.000	95,5%	93,4%	95,3%
Porto Seleta c/ vaga	T+4	197.124	51	222.927	214.000	97,3%	101,4%	84,1%

Unidades Totais:	907	**Preço Médio:**	212.375	**Renda Média:**	2.581	**ITBI+Emol. Unit. Médio:**	3.661
Unidades Tenda:	907	**Avaliação Média:**	202.491	**Ato:**	1.430 (0,55 Salários)	**Custo do Ciclo Unit.:**	14.772
VSO:	34,8846153846154 U	**VGV Total:**	192.623.724	**FGTS:**	1.607 (0,62 Salários)	**Preço Raso Médio:**	187.804
RET Médio:	1,8%	**VGV Tenda:**	192.623.724	**% em RET 1%:**	72%	**Adc. Tx. de Aceleração Médio:**	600

Construção

Custo Total Unit.:	94.126	**Eventuais:**	2,00%	**Área priv (m²):**	34,10	**Gape / Mês Unit.:**	9,42

Resultado

LI (R$):	**35.893.202**	**LI:**	**25,30%**	**Exposição de Caixa (R$):**	**19.166.815**	**Margem Bruta Econômica:**	**43,35%**
TIR:	**101,93%**	**LI Aprovação:**	**22,00%**	**Ger. Caixa 12 meses (R$):**	**(17.444.728)**	**Margem Bruta REF:**	**45,23%**
Exposição de Caixa:	**9,64%**	**Δ LI:**	**3,30%**	**Ger. Caixa 24 meses (R$):**	**6.490.131**	**Margem Rasa Econômica:**	**35,01%**
Payback Contingente (21 m):	**16 m/ (-5 m)**	**LI Marginal:**	**26,61%**	**Ger. Caixa Marginal (R$):**	**63.961.218**	**Margem Rasa REF:**	**38,07%**
Payback Consolidado:	**16 meses**					**Margem de Contribuição Econômica:**	**32,60%**

DRE Consolidado

R$ Mil - Valores Nominais - Compra	Porto Lima + Porto Seleta		Porto Lima s/ vaga		Porto Lima c/ vaga		Porto Seleta s/ vaga		Porto Seleta c/ vaga	
	Nominal	%	Nominal	%	Nominal	%	Nominal	%	Nominal	%
Receita	198.725	100,0%	81.115	100,0%	11.905	100,0%	93.816	100,0%	11.888	100,0%
PIS/COFINS	(2.003)	1,0%	(778)	1,0%	(163)	1,4%	(900)	1,0%	(163)	1,4%
Custo Total	(111.448)	56,7%	(45.701)	56,9%	(6.378)	54,3%	(52.946)	57,0%	(6.422)	54,8%
Custo Terreno	(9.188)	4,7%	(3.860)	4,8%	(537)	4,6%	(4.275)	4,6%	(517)	4,4%
Custo Relacionados a Terreno	(1.032)	0,5%	(430)	0,5%	(60)	0,5%	(484)	0,5%	(59)	0,5%
Custos de Incorporação	(6.346)	3,2%	(2.584)	3,2%	(380)	3,2%	(2.996)	3,2%	(386)	3,3%
Custo de Construção	(94.881)	48,2%	(38.828)	48,3%	(5.401)	46,0%	(45.191)	48,6%	(5.461)	46,6%
Lucro Bruto Econômico	85.274	43,3%	34.636	43,1%	5.365	45,7%	39.970	43,0%	5.303	45,2%
Custo para Rateio	-	0,0%	-	0,0%	-	0,0%	-	0,0%	-	0,0%
Lucro Bruto Contábil	85.274	43,3%	34.636	43,1%	5.365	45,7%	39.970	43,0%	5.303	45,2%
Despesas de Selling	(17.771)	9,0%	(7.228)	9,0%	(1.076)	9,2%	(8.378)	9,0%	(1.088)	9,3%
Contingência	(3.368)	1,7%	(1.375)	1,7%	(202)	1,7%	(1.590)	1,7%	(201)	1,7%
Margem de Contribuição	64.135	32,6%	26.033	32,4%	4.087	34,8%	30.002	32,3%	4.013	34,2%
IR e CSLL	(1.639)	0,8%	(636)	0,8%	(133)	1,1%	(736)	0,8%	(133)	1,1%
Margem Líquida	62.496	31,8%	25.397	31,6%	3.953	33,7%	29.266	31,5%	3.880	33,1%
Lucro Bruto REF Unit.	100.538	45,2%	96.889	44,9%	110.181	48,1%	100.769	44,7%	115.872	48,2%
Lucro Raso REF Unit.	74.854	38,1%	71.915	37,7%	83.583	41,3%	74.812	37,6%	88.088	41,5%

R$ Mil - VPL - Compra	Porto Lima + Porto Seleta		Porto Lima s/ vaga		Porto Lima c/ vaga		Porto Seleta s/ vaga		Porto Seleta c/ vaga	
	VP	%	VP	%	VP	%	VP	%	VP	%
Receitas	141.893	100,0%	63.441	100,0%	9.281	100,0%	61.520	100,0%	7.651	100,0%
PIS/COFINS	(1.411)	1,0%	(600)	0,9%	(125)	1,4%	(582)	0,9%	(103)	1,4%
Custos e Despesas Totais	(104.589)	73,7%	(46.345)	73,1%	(6.569)	70,8%	(46.027)	74,8%	(5.648)	73,8%
Custo Terreno	(7.336)	5,2%	(3.082)	4,9%	(429)	4,6%	(3.413)	5,5%	(413)	5,4%
Custo Relacionados a Terreno	(1.114)	0,8%	(464)	0,7%	(65)	0,7%	(522)	0,8%	(63)	0,8%
Custos de Incorporação	(5.601)	3,9%	(2.441)	3,8%	(359)	3,9%	(2.482)	4,0%	(319)	4,2%
Custo de Construção	(73.360)	51,7%	(32.740)	51,6%	(4.554)	49,1%	(32.176)	52,3%	(3.889)	50,8%
Despesas de Selling	(14.598)	10,3%	(6.488)	10,2%	(966)	10,4%	(6.342)	10,3%	(802)	10,5%
Contingência	(1.426)	1,0%	(639)	1,0%	(94)	1,0%	(615)	1,0%	(78)	1,0%
IR e CSLL	(1.154)	0,8%	(491)	0,8%	(103)	1,1%	(476)	0,8%	(85)	1,1%
Lucro Imobiliário	35.893	25,3%	16.497	26,0%	2.586	27,9%	14.911	24,2%	1.899	24,8%

DRE Fase

R$ Mil - Valores Nominais - Compra	Porto Lima + Porto Seleta		Primeira Fase		Demais Fases	
	Nominal	%	Nominal	%	Nominal	%
Receita	198.725	100,0%	93.021	100,0%	105.704	100,0%
PIS/COFINS	(2.003)	1,0%	(941)	1,0%	(1.062)	1,0%
Custo Total	(111.448)	56,7%	(52.079)	56,6%	(59.369)	56,7%
Custo Terreno	(9.188)	4,7%	(4.397)	4,8%	(4.792)	4,6%
Custo Relacionados a Terreno	(1.032)	0,5%	(490)	0,5%	(543)	0,5%
Custos de Incorporação	(6.346)	3,2%	(2.964)	3,2%	(3.382)	3,2%
Custo de Construção	(94.881)	48,2%	(44.229)	48,0%	(50.652)	48,4%
Lucro Bruto Econômico	85.274	43,3%	40.001	43,4%	45.273	43,3%
Custo para Rateio	-	0,0%	-	0,0%	-	0,0%
Lucro Bruto Contábil	85.274	43,3%	40.001	43,4%	45.273	43,3%
Despesas de Selling	(17.771)	9,0%	(8.305)	9,0%	(9.466)	9,0%
Contingência	(3.368)	1,7%	(1.576)	1,7%	(1.791)	1,7%
Margem de Contribuição	64.135	32,6%	30.120	32,7%	34.015	32,5%
IR e CSLL	(1.639)	0,8%	(770)	0,8%	(869)	0,8%
Margem Líquida	62.496	31,8%	29.350	31,9%	33.146	31,7%
Lucro Bruto REF Unit.	100.538	45,2%	98.512	45,3%		
Lucro Raso REF Unit.	74.854	38,1%	73.340	38,2%		

R$ Mil - VPL - Compra	Porto Lima + Porto Seleta		Primeira Fase		Demais Fases	
	VP	%	VP	%	VP	%
Receitas	141.893	100,0%	72.722	100,0%	69.171	100,0%
PIS/COFINS	(1.411)	1,0%	(725)	1,0%	(685)	1,0%
Custos e Despesas Totais	(104.589)	73,7%	(52.914)	72,8%	(51.675)	74,7%
Custo Terreno	(7.336)	5,2%	(3.510)	4,8%	(3.826)	5,5%
Custo Relacionados a Terreno	(1.114)	0,8%	(529)	0,7%	(585)	0,8%
Custos de Incorporação	(5.601)	3,9%	(2.800)	3,9%	(2.801)	4,0%
Custo de Construção	(73.360)	51,7%	(37.295)	51,3%	(36.065)	52,1%
Despesas de Selling	(14.598)	10,3%	(7.454)	10,2%	(7.144)	10,3%
Contingência	(1.426)	1,0%	(733)	1,0%	(693)	1,0%
IR e CSLL	(1.154)	0,8%	(594)	0,8%	(561)	0,8%
Lucro Imobiliário	35.893	25,3%	19.083	26,2%	16.810	24,3%

Comparativo

Comparativo dos Estudos - Consolidado	Anterior	Atual	Atual vs Anterior	Δ%
Data Estudo:	abril-25	fevereiro-26	10 Meses	N/A
Lançamento:	abril-26	março-26	-1 Meses	N/A
Uhs:	907	907	-	0,0%
Preço Nominal:	198.196	212.375	14.179	7,2%
Preço Raso:	176.933	187.804	10.871	6,1%
Preço Nominal Inflacionado:	231.901	222.303	(9.599)	-4,1%
Preço Raso Inflacionado:	207.056	196.618	(10.438)	-5,0%
Renda Média:	2.541	2.581	40	1,6%
RET Médio:	1,84%	1,84%	0,0 p.p.	0,0%
% em RET 1%:	72,13%	72,13%	0,0 p.p.	0,0%
VSO:	17	35	18	102,2%
ITBI/Emol. Inf (Unit)[2]:	5.090	4.399	(691)	-13,6%
Avaliação:	202.491	202.491	-	0,0%
Prazo construção F1:	11	12	1	9,1%
Prazo de Pró-Soluto F1:	16	17	1	6,3%
Custo Total Inf (Unit):	131.016	122.875	(8.141)	-6,2%
Custo Construção (Unit):	91.013	94.126	3.113	3,4%
Custo Construção Corrigido:	90.657	94.126	3.469	3,8%
Fração de construção:	45,7%	44,3%	-1,4 p.p.	-3,1%
INCC Folha Rosto:	1.178,39	1.228,16	50	4,2%
Custo Terreno Inf:	8.578.719	9.188.291	609.572	7,1%
Custo Relacionados a Terreno (Unit):	1.256	1.138	(118)	-9,4%
Fração do Terreno[1]:	4,8% / 50,7%	4,4% / 48,7%	-0,4 p.p.	-8,3%
Custo de Incorp. por uh:	8.394	6.996	(1.398)	-16,6%
ITBI/Emol. Inf (Total)[2]:	4.616.778	3.990.031	(626.747)	-13,6%
Custo do Ciclo (Unit):	13.666	14.772	1.105	8,1%
LI Resiliência:	7,8%	7,8%	0,0 p.p.	-0,2%
Lucro Imobiliário:	20,5%	25,3%	4,8 p.p.	23,2%
LI Marginal:	N/A	26,6%	N/A	
Exposição de caixa:	8,1%	9,6%	1,6 p.p.	19,7%
TIR:	65,7%	101,9%	36,3 p.p.	55,2%
Margem Bruta REF:	44,1%	45,2%	1,2 p.p.	2,7%
Margem Bruta Econômica:	41,8%	43,3%	1,5 p.p.	3,7%
Margem Rasa REF:	37,3%	38,1%	0,7 p.p.	1,9%
Margem Rasa Econômica:	34,3%	35,0%	0,7 p.p.	2,1%
Margem Contribuição Econômica:	29,9%	32,6%	2,7 p.p.	8,9%
Payback Contingente (Régua 21 m):	17 m/ (-4 m)	16 m/ (-5 m)	-1	
Payback Consolidado:	17 Meses	16 Meses	-1 Meses	-5,9%

[1] Valor do terreno contratual
[2] ITBI com taxa de Aceleração

Obrigado